CONSTRUCCIONES II · UNM

NUDOS

PRÁCTICA EN CLASE · HORMIGÓN PREMOLDEADO DE GRANDES LUCES


Nudos pertenecientes al proyecto del trabajo práctico, dibujados en forma proporcionada a escala 1:20, con referencias que incluyen función, denominación y especificación técnica de los materiales.

ÍNDICE DE LÁMINAS (A4)

01	Carátula · consigna · índice	1:100	**10**	Nudo 3 · planilla (cont.)	—
02	Nudo 1 · Cubierta · opaco	1:20	**11**	Nudo 4 · Entrepiso · vidriado	1:20
03	Nudo 1 · planilla	—	**12**	Nudo 4 · planilla	—
04	Nudo 1 · planilla (cont.)	—	**13**	Nudo 4 · planilla (cont.)	—
05	Nudo 2 · Cubierta · vidriado	1:20	**14**	Nudo 5 · Piso + fundación · opaco	1:20
06	Nudo 2 · planilla	—	**15**	Nudo 5 · planilla	—
07	Nudo 2 · planilla (cont.)	—	**16**	Nudo 6 · Piso + fundación · vidriado	1:20
08	Nudo 3 · Entrepiso · opaco	1:20	**17**	Nudo 6 · planilla	—
09	Nudo 3 · planilla	—			

CORTE INTEGRAL
CERRAMIENTO OPACO

CORTE INTEGRAL
CERRAMIENTO VIDRIADO

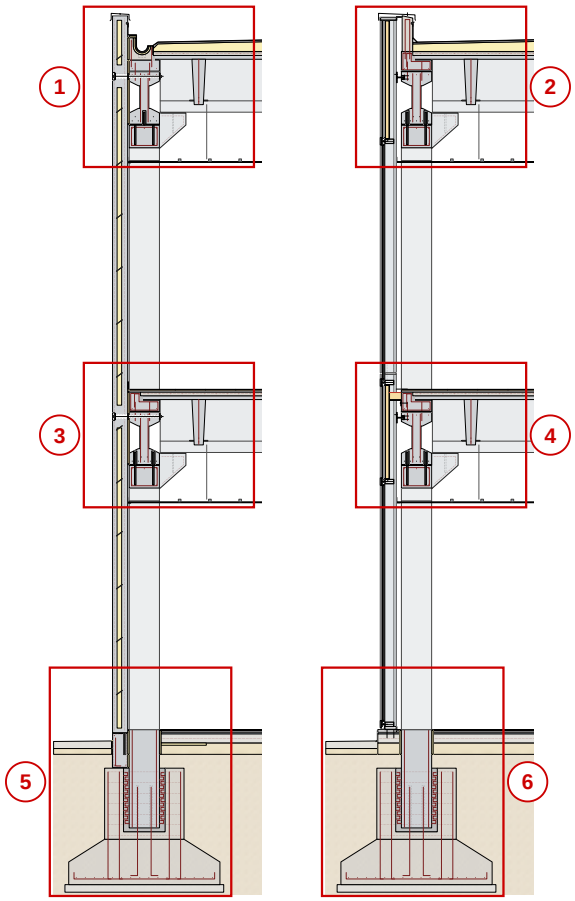

Cortes integrales esquemáticos esc. 1:100
en rojo: encuadre de cada nudo

SISTEMA CONSTRUCTIVO

Estructura de hormigón premoldeado de grandes luces (sistema Pi): columnas 40x40 c/ ménsulas, vigas VL doble T pretensadas en fachada, vigas VP T invertida interiores y losas TT h 0,65 con capa de compresión in situ. Bases aisladas de H°A in situ con cuello (anclaje mecánico húmedo).

CERRAMIENTOS

Opaco: panel sándwich premoldeado de H°A (6 + EPS 6 + 8 cm) fijado a la VL con bulón pasante y apoyado en viga portapanel.
Vidriado: muro cortina stick de aluminio con DVH y spandrel, colgado de la estructura c/ grapas.

CONVENCIONES

- H° premoldeado (cortado)
- H° pobre / contrapiso
- Lana mineral
- Vidrio
- H°A in situ
- EPS / H° liviano c/ EPS
- Terreno natural
- Aluminio

PRÁCTICA EN CLASE · NUDOS Carátula, consigna e índice; ubicación de los nudos en los cortes integrales	DOCENTE: Arq. Tucci y Arq. Cardozo ALUMNA: Candelaria Vitale GRUPO: 13	**CONSTRUCCIONES II · UNM** CÁTEDRA: ARQ. TUCCI FECHA: 22/10/2026	LÁMINA **01/17** **ESC. 1:100**