
# NUDO 1 — CUBIERTA CON CERRAMIENTO EXTERIOR OPACO

Corte vertical por la zona de apoyo de la viga VL · ESCALA 1:20

*Panel sándwich premoldeado H°A como parapeto · canaleta H°A in situ · VL + viga de borde + losa TT*

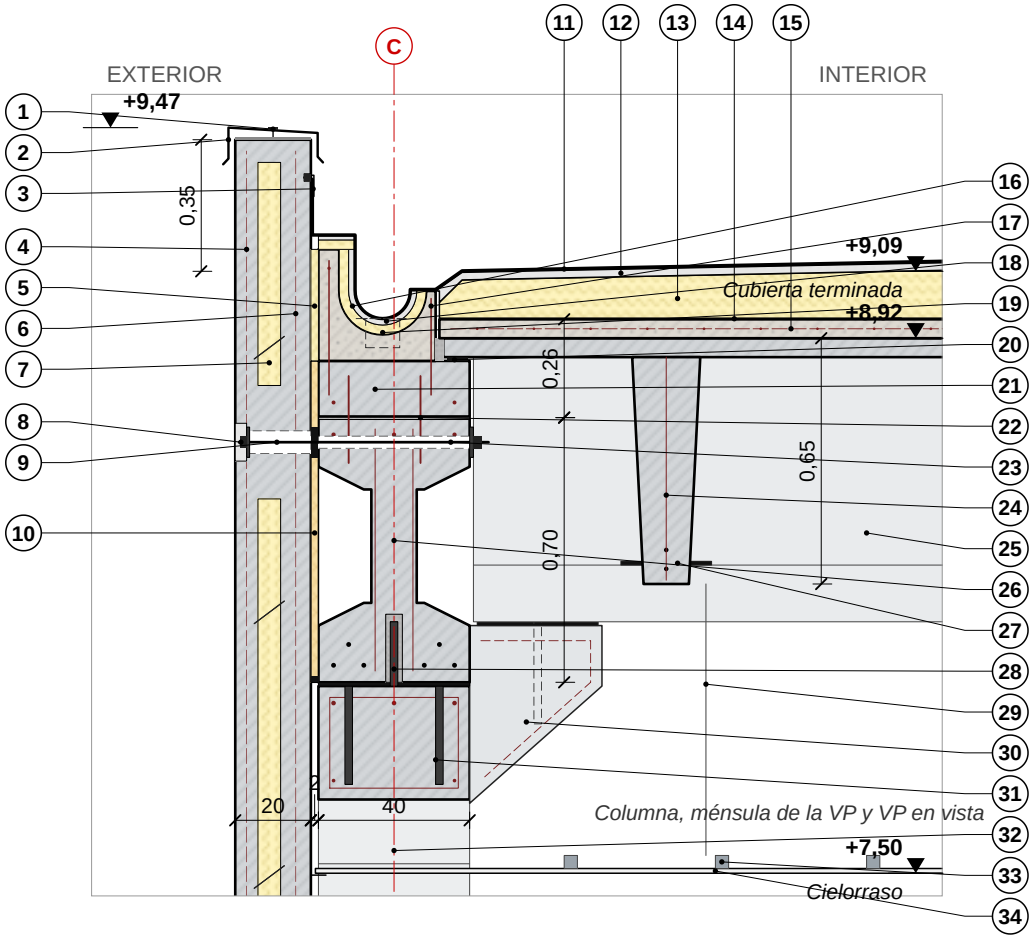


**REFERENCIAS** *denominación · especificación técnica y función en la planilla siguiente*

**1** Fijación de la cupertina
**2** Cupertina
**3** Babeta
**4** Panel sándwich premoldeado
**5** Junta panel / canaleta
**6** Hojas de hormigón del panel
**7** Núcleo aislante del panel
**8** Rehundido del anclaje
**9** Agujero ovalado + vaina
**10** Junta panel / estructura
**11** Membrana hidrófuga
**12** Carpeta de asiento
**13** Contrapiso de pendiente (aislante)
**14** Barrera de vapor
**15** Capa de compresión
**16** Aislación de la canaleta
**17** Estribos salientes
**18** Canaleta de desagüe
**19** Embudo de desagüe (oculto)
**20** Apoyo del ala del TT
**21** Viga de borde
**22** Junta VL / viga de borde
**23** Bulón pasante (fija panel)
**24** Losa premoldeada TT
**25** Viga VP principal (en vista)
**26** Viga VL perimetral
**27** Apoyo nervio TT / VP
**28** Neopreno + perno VL / ménsula
**29** Velas de cuelgue
**30** Apoyo de la VP (en vista)
**31** Ménsula corta de columna
**32** Columna premoldeada (en vista)
**33** Estructura del cielorraso
**34** Cielorraso suspendido

**ESCALA GRÁFICA 1:20**

0 — 0,50 — 1,00 m

*Cotas en m (secciones en cm) · niveles en m s/ N.P.T. P. Baja ±0,00*

*Hormigón premoldeado de grandes luces (sistema Pi) · mismo edificio del TP*

| | | | |
|---|---|---|---|
| **PRÁCTICA EN CLASE · NUDOS**<br>Nudo 1: Cubierta con cerramiento exterior opaco - corte 1:20 | DOCENTE: Arq. Tucci y Arq. Cardozo<br>ALUMNA: Candelaria Vitale<br>GRUPO: 13 | **CONSTRUCCIONES II · UNM**<br>CÁTEDRA: ARQ. TUCCI<br>FECHA: 22/10/2026 | LÁMINA **02/17**<br>**ESC. 1:20** |