
NUDO 2 — CUBIERTA CON CERRAMIENTO EXTERIOR VIDRIADO

Corte vertical por la zona de apoyo de la viga VL · ESCALA 1:20

Muro cortina stick (aluminio + DVH) colgado de la estructura · zócalo H°A in situ · VL + viga L + losa TT

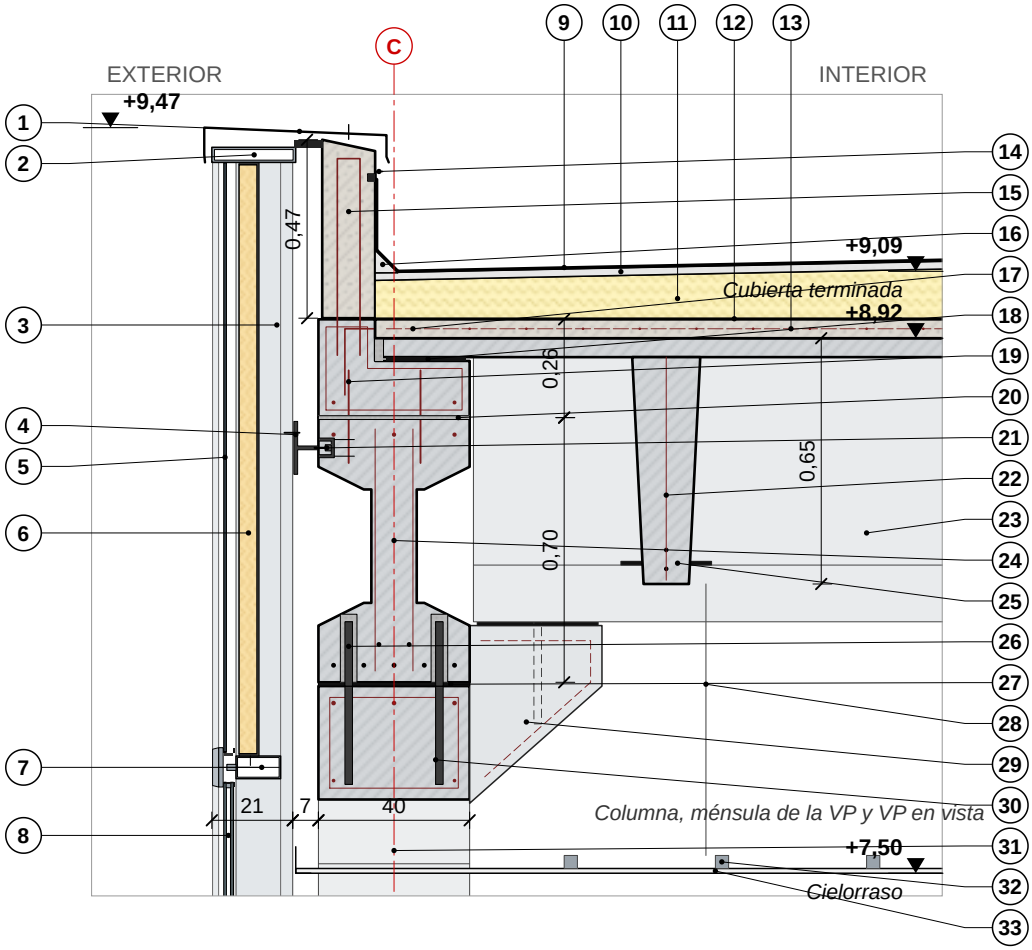

REFERENCIAS *denominación · especificación técnica y función en la planilla siguiente*

1 Cupertina
2 Perfil de cierre superior del muro cortina
3 Montante (mullion)
4 Grapa de anclaje
5 Spandrel
6 Bandeja aislante
7 Travesaño + presor + tapa
8 Doble vidriado hermético (DVH)
9 Membrana hidrófuga
10 Carpeta de asiento
11 Contrapiso de pendiente (aislante)
12 Barrera de vapor
13 Capa de compresión
14 Babeta
15 Zócalo / parapeto superior
16 Media caña
17 Estribos salientes
18 Apoyo del ala del TT
19 Viga L de borde
20 Junta VL / viga de borde
21 Riel de anclaje embutido
22 Losa premoldeada TT
23 Viga VP principal (en vista)
24 Viga VL perimetral
25 Apoyo nervio TT / VP
26 Pernos de vinculación VL
27 Apoyo elastomérico de la VL
28 Velas de cuelgue
29 Apoyo de la VP (en vista)
30 Ménsula corta de columna
31 Columna premoldeada (en vista)
32 Estructura del cielorraso
33 Cielorraso suspendido

ESCALA GRÁFICA 1:20

0 — 0,50 — 1,00 m

Cotas en m (secciones en cm) · niveles en m s/ N.P.T. P. Baja ±0,00

Hormigón premoldeado de grandes luces (sistema Pi) · mismo edificio del TP

PRÁCTICA EN CLASE · NUDOS Nudo 2: Cubierta con cerramiento exterior vidriado - corte 1:20	DOCENTE: Arq. Tucci y Arq. Cardozo ALUMNA: Candelaria Vitale GRUPO: 13	**CONSTRUCCIONES II · UNM** CÁTEDRA: ARQ. TUCCI FECHA: 22/10/2026	LÁMINA **05/17** **ESC. 1:20**