
NUDO 4 — ENTREPISO CON CERRAMIENTO EXTERIOR VIDRIADO

Corte vertical por la zona de apoyo de la viga VL · ESCALA 1:20

Muro cortina stick: grapa al riel de la viga L, junta de dilatación y barrera cortafuego en el frente de losa

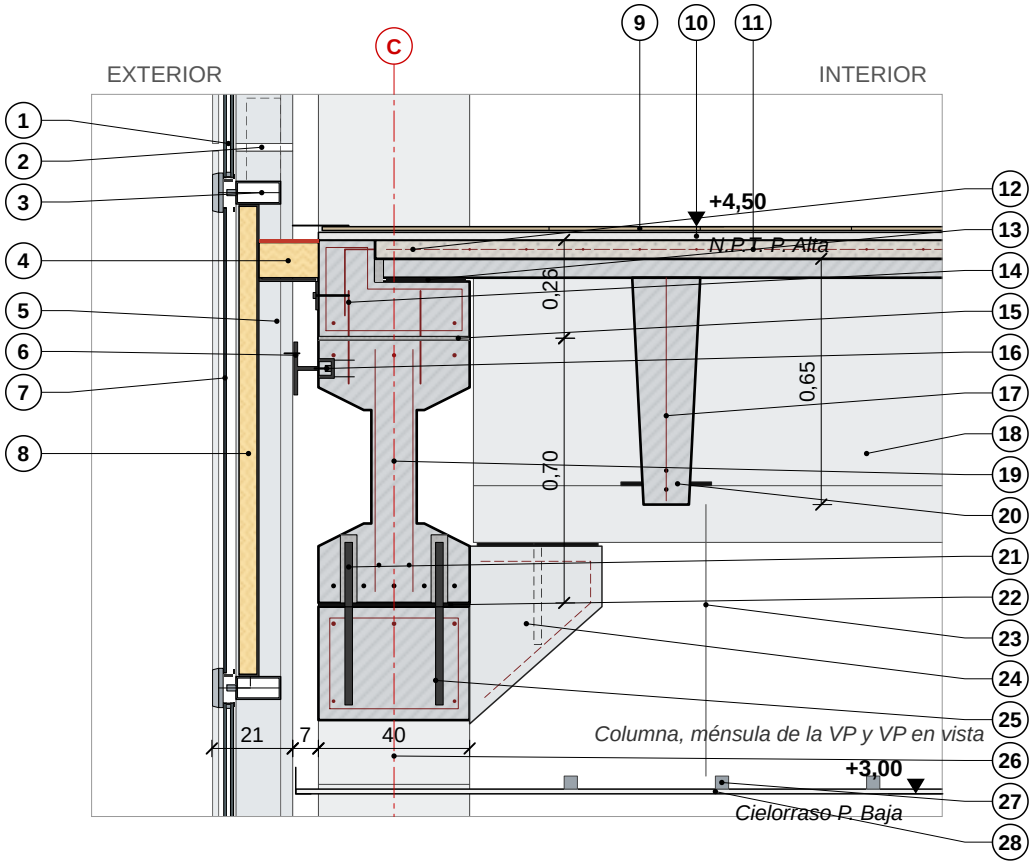

REFERENCIAS *denominación · especificación técnica y función en la planilla siguiente*

1 Doble vidriado hermético (DVH)
2 Junta de dilatación del montante
3 Travesaño + presor + tapa
4 Barrera cortafuego
5 Montante (mullion)
6 Grapa de anclaje
7 Spandrel
8 Bandeja aislante
9 Solado
10 Carpeta niveladora
11 Capa de compresión
12 Estribos salientes
13 Apoyo del ala del TT
14 Viga L de borde
15 Junta VL / viga de borde
16 Riel de anclaje embutido
17 Losa premoldeada TT
18 Viga VP principal (en vista)
19 Viga VL perimetral
20 Apoyo nervio TT / VP
21 Pernos de vinculación VL
22 Apoyo elastomérico de la VL
23 Velas de cuelgue
24 Apoyo de la VP (en vista)
25 Ménsula corta de columna
26 Columna premoldeada (en vista)
27 Estructura del cielorraso
28 Cielorraso suspendido

ESCALA GRÁFICA 1:20

0 — 0,50 — 1,00 m

Cotas en m (secciones en cm) · niveles en m s/ N.P.T. P. Baja ±0,00

Hormigón premoldeado de grandes luces (sistema Pi) · mismo edificio del TP

PRÁCTICA EN CLASE · NUDOS Nudo 4: Entrepiso con cerramiento exterior vidriado - corte 1:20	DOCENTE: Arq. Tucci y Arq. Cardozo ALUMNA: Candelaria Vitale GRUPO: 13	**CONSTRUCCIONES II · UNM** CÁTEDRA: ARQ. TUCCI FECHA: 22/10/2026	LÁMINA **11/17** **ESC. 1:20**