
NUDO 5

PISO SOBRE TERRENO NATURAL CON CERRAMIENTO EXTERIOR OPACO Y FUNDACIÓN

Corte vertical por la zona de apoyo de la viga VL · ESCALA 1:20

Panel apoyado en viga portapanel s/ cuello · base aislada H°A in situ c/ cuello (anclaje mecánico húmedo)

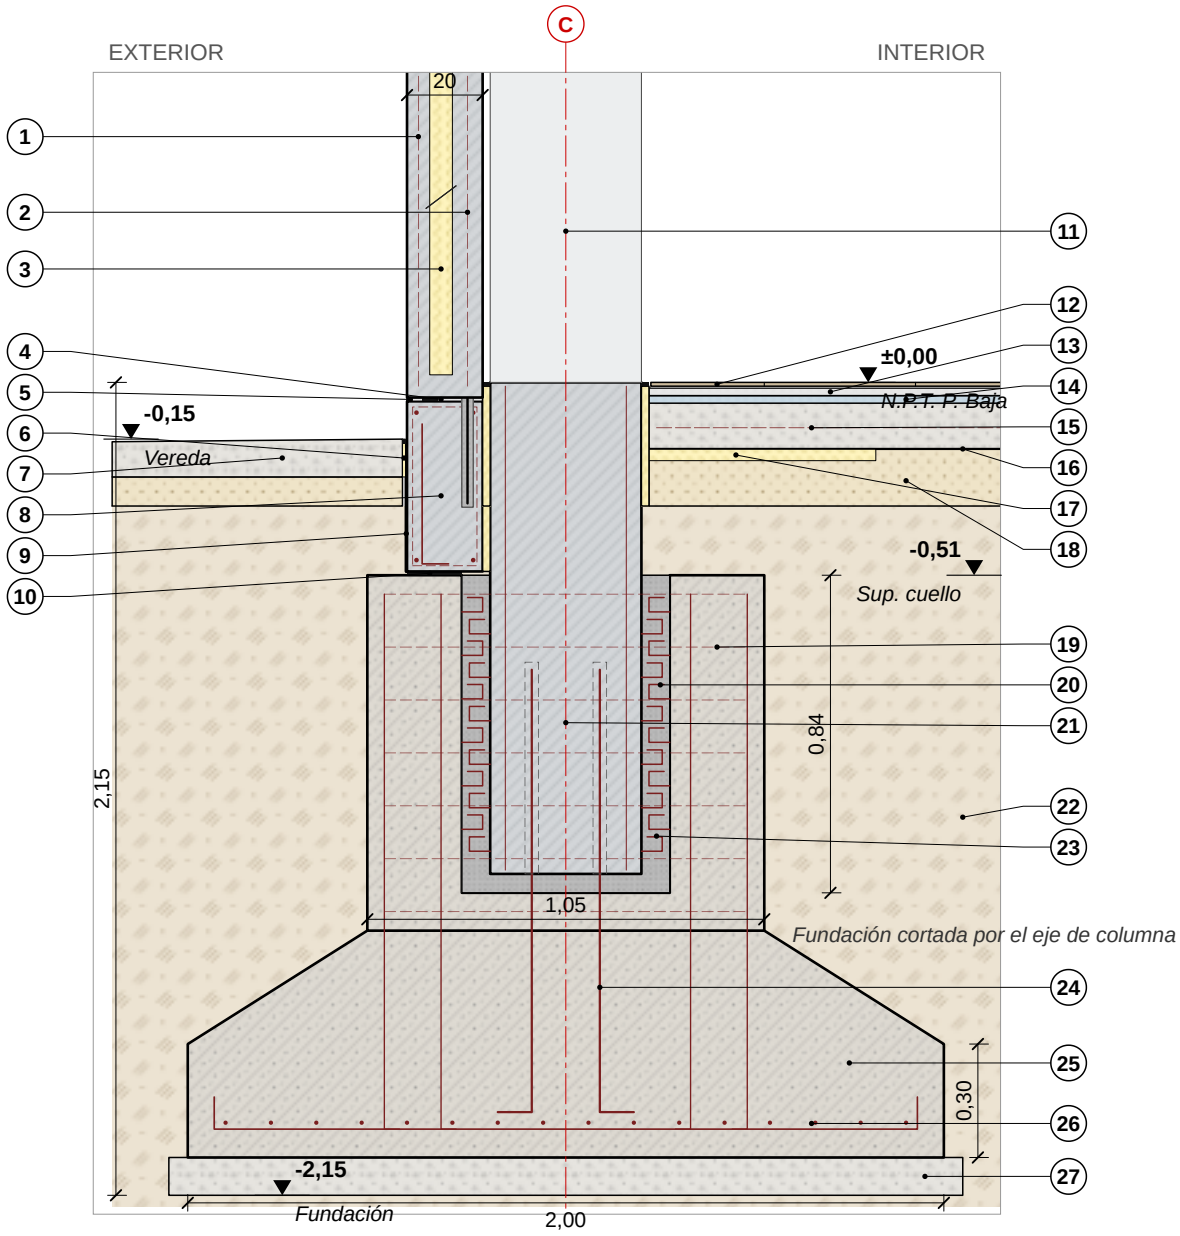

REFERENCIAS *denominación · especificación técnica y función en la planilla siguiente*

1 Panel sándwich premoldeado
2 Hojas de hormigón del panel
3 Núcleo aislante del panel
4 Asiento del panel
5 Sellado de junta horizontal
6 Junta vereda / viga
7 Vereda perimetral
8 Viga portapanel
9 Protección de caras enterradas
10 Apoyo de la viga portapanel
11 Columna premoldeada (en vista)
12 Solado
13 Carpeta niveladora
14 Carpeta hidrófuga
15 Contrapiso
16 Film de polietileno
17 Junta + faja perimetral EPS
18 Relleno compactado
19 Cuello (cáliz) de la base
20 Anclaje mecánico húmedo
21 Tronco de columna embutido
22 Terreno natural
23 Relleno de la unión
24 Armadura de vinculación
25 Base aislada
26 Armadura de la base
27 Hormigón de limpieza

ESCALA GRÁFICA 1:20

0 — 0,50 — 1,00 m

Cotas en m (secciones en cm) · niveles en m s/ N.P.T. P. Baja ±0,00

Hormigón premoldeado de grandes luces (sistema Pi) · mismo edificio del TP

PRÁCTICA EN CLASE · NUDOS Nudo 5: Piso sobre terreno natural con cerramiento exterior opaco y fundación - corte 1:20	DOCENTE: Arq. Tucci y Arq. Cardozo ALUMNA: Candelaria Vitale GRUPO: 13	**CONSTRUCCIONES II · UNM** CÁTEDRA: ARQ. TUCCI FECHA: 22/10/2026	LÁMINA **14/17** **ESC. 1:20**