
NUDO 6

PISO SOBRE TERRENO NATURAL CON CERRAMIENTO EXTERIOR VIDRIADO Y FUNDACIÓN

Corte vertical por la zona de apoyo de la viga VL · ESCALA 1:20

Muro cortina colgado del entrepiso con perfil guía deslizante · base aislada H°A in situ c/ cuello

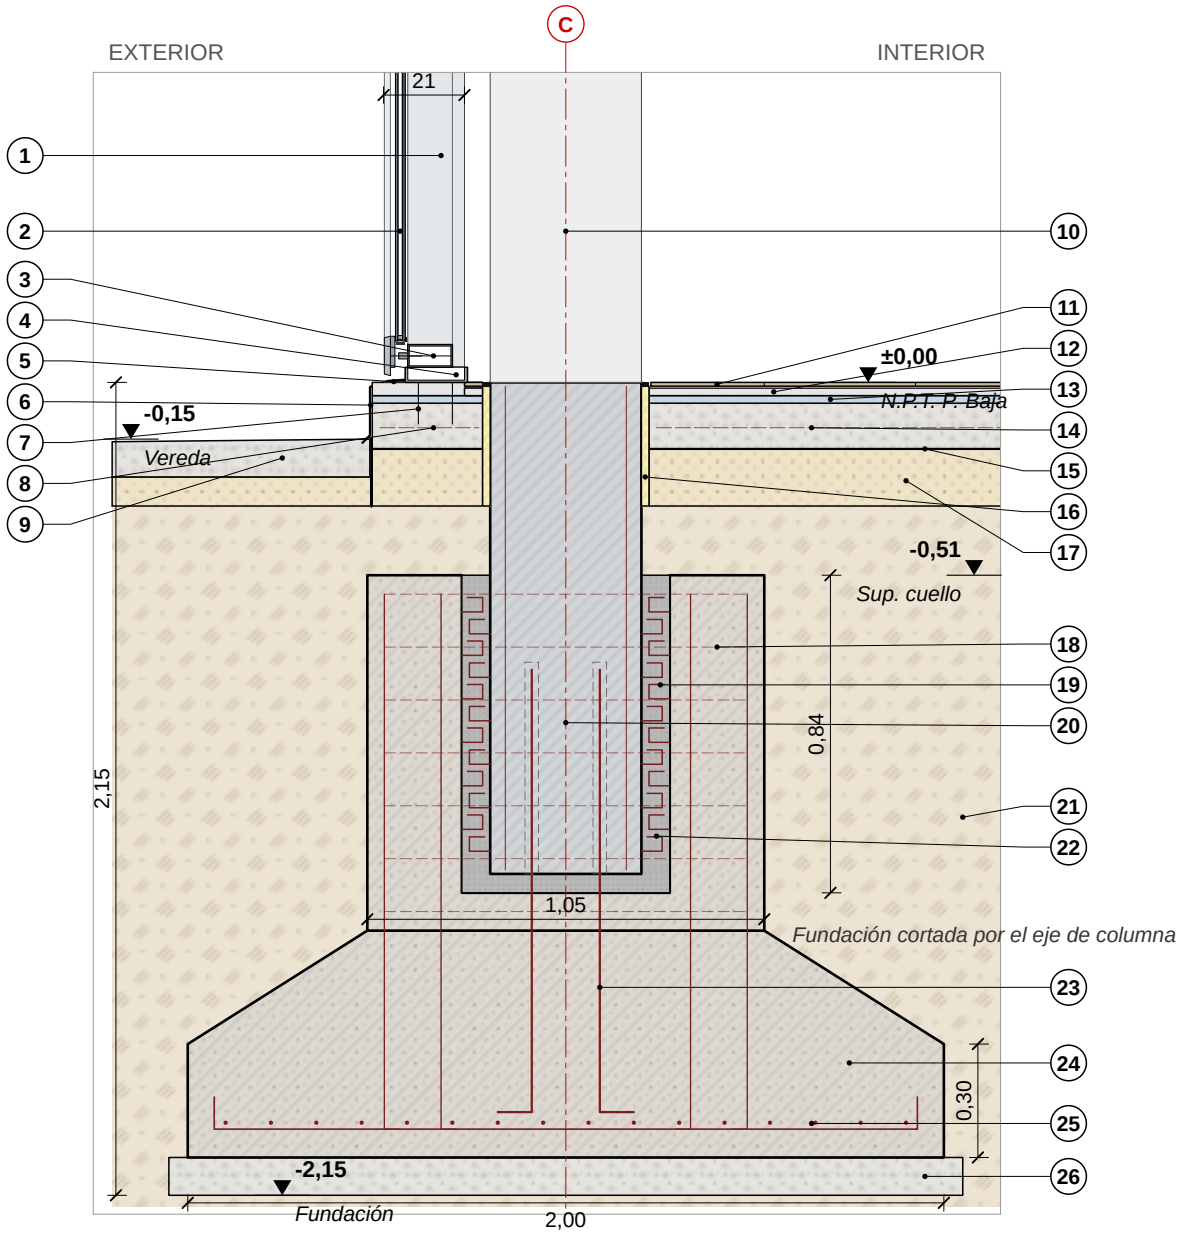

REFERENCIAS *denominación · especificación técnica y función en la planilla siguiente*

1 Montante de planta baja
2 Doble vidriado hermético (DVH)
3 Travesaño + presor + tapa
4 Perfil guía de arranque
5 Sellado perimetral
6 Babeta de arranque + aislación
7 Broca de fijación
8 Contrapiso armado de borde
9 Vereda perimetral
10 Columna premoldeada (en vista)
11 Solado
12 Carpeta niveladora
13 Carpeta hidrófuga
14 Contrapiso
15 Film de polietileno
16 Junta de dilatación piso / columna
17 Relleno compactado
18 Cuello (cáliz) de la base
19 Anclaje mecánico húmedo
20 Tronco de columna embutido
21 Terreno natural
22 Relleno de la unión
23 Armadura de vinculación
24 Base aislada
25 Armadura de la base
26 Hormigón de limpieza

ESCALA GRÁFICA 1:20

0 — 0,50 — 1,00 m

Cotas en m (secciones en cm) · niveles en m s/ N.P.T. P. Baja ±0,00

Hormigón premoldeado de grandes luces (sistema Pi) · mismo edificio del TP

PRÁCTICA EN CLASE · NUDOS Nudo 6: Piso sobre terreno natural con cerramiento exterior vidriado y fundación - corte 1:20	DOCENTE: Arq. Tucci y Arq. Cardozo ALUMNA: Candelaria Vitale GRUPO: 13	**CONSTRUCCIONES II · UNM** CÁTEDRA: ARQ. TUCCI FECHA: 22/10/2026	LÁMINA **16/17** **ESC. 1:20**