CONSTRUCCIONES II · UNM

NUDOS

PRÁCTICA EN CLASE · ESTRUCTURA DE ACERO


Nudos pertenecientes al proyecto del trabajo práctico, dibujados en forma proporcionada a escala 1:20, con referencias que incluyen función, denominación y especificación técnica de los materiales.

ÍNDICE DE LÁMINAS (A4)

01	Carátula · consigna · índice	1:100	**11**	Nudo 3 · planilla	—
02	Corte integral · opaco	1:50	**12**	Nudo 4 · Entrepiso · vidriado	1:20
03	Corte integral · vidriado	1:50	**13**	Nudo 4 · planilla	—
04	Nudo 1 · Cubierta · opaco	1:20	**14**	Nudo 5 · Piso + fundación · opaco	1:20
05	Nudo 1 · planilla	—	**15**	Nudo 5 · planilla	—
06	Nudo 1 · planilla (cont.)	—	**16**	Nudo 5 · planilla (cont.)	—
07	Nudo 2 · Cubierta · vidriado	1:20	**17**	Nudo 6 · Piso + fundación · vidriado	1:20
08	Nudo 2 · planilla	—	**18**	Nudo 6 · planilla	—
09	Nudo 2 · planilla (cont.)	—	**19**	Nudo 6 · planilla (cont.)	—
10	Nudo 3 · Entrepiso · opaco	1:20			

CORTE INTEGRAL
CERRAMIENTO OPACO

CORTE INTEGRAL
CERRAMIENTO VIDRIADO

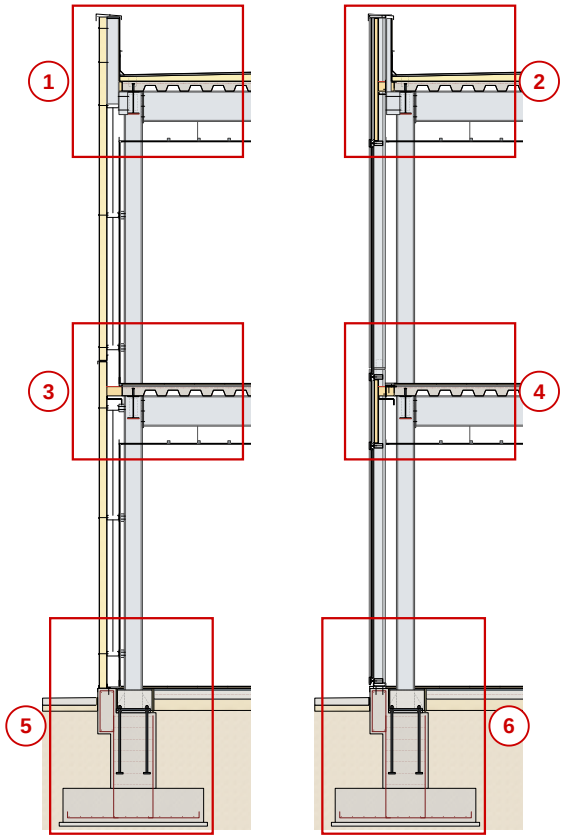

SISTEMA CONSTRUCTIVO

Estructura de perfiles laminados de acero F-24: columnas HEB 240, vigas principales IPE 400 c/ 2,50 m unidas a la columna c/ placa extrema y bulones M20 8.8, vigas de borde IPE 300 c/ doble ángulo. Losa colaborante (steel deck h 75 + H-25, e 13 cm) c/ conectores de corte. Bases: placa base c/ pernos de anclaje Ø24 y grout sobre cuello y zapata de H°A in situ. Antióxido + pintura intumescente F60.

CERRAMIENTOS

Opaco: panel sándwich metálico PIR 100 mm atornillado a correas C 160 galv. (c/ tensores) fijadas a las columnas.
Vidriado: muro cortina stick de aluminio c/ DVH y spandrel, colgado de la losa c/ grapas s/ placa embebida.

CONVENCIONES

- Acero cortado
- Acero en vista
- H°A in situ / losa
- H° pobre / contrapiso
- Espuma PIR (panel)
- H° liviano c/ EPS
- Lana mineral
- Terreno natural
- Vidrio
- Aluminio

Cortes integrales esquemáticos esc. 1:100
en rojo: encuadre de cada nudo

PRÁCTICA EN CLASE · NUDOS Carátula, consigna e índice; ubicación de los nudos en los cortes integrales	DOCENTE: Arq. Tucci y Arq. Cardozo ALUMNA: Candelaria Vitale GRUPO: 13	**CONSTRUCCIONES II · UNM** CÁTEDRA: ARQ. TUCCI FECHA: 22/10/2026	LÁMINA **01/19** **ESC. 1:100**