
CORTE INTEGRAL

ESTRUCTURA DE ACERO · CERRAMIENTO OPACO · ESCALA 1:50

Corte vertical entre columnas; fundación cortada por el eje de columna. Base de los 6 nudos 1:20.

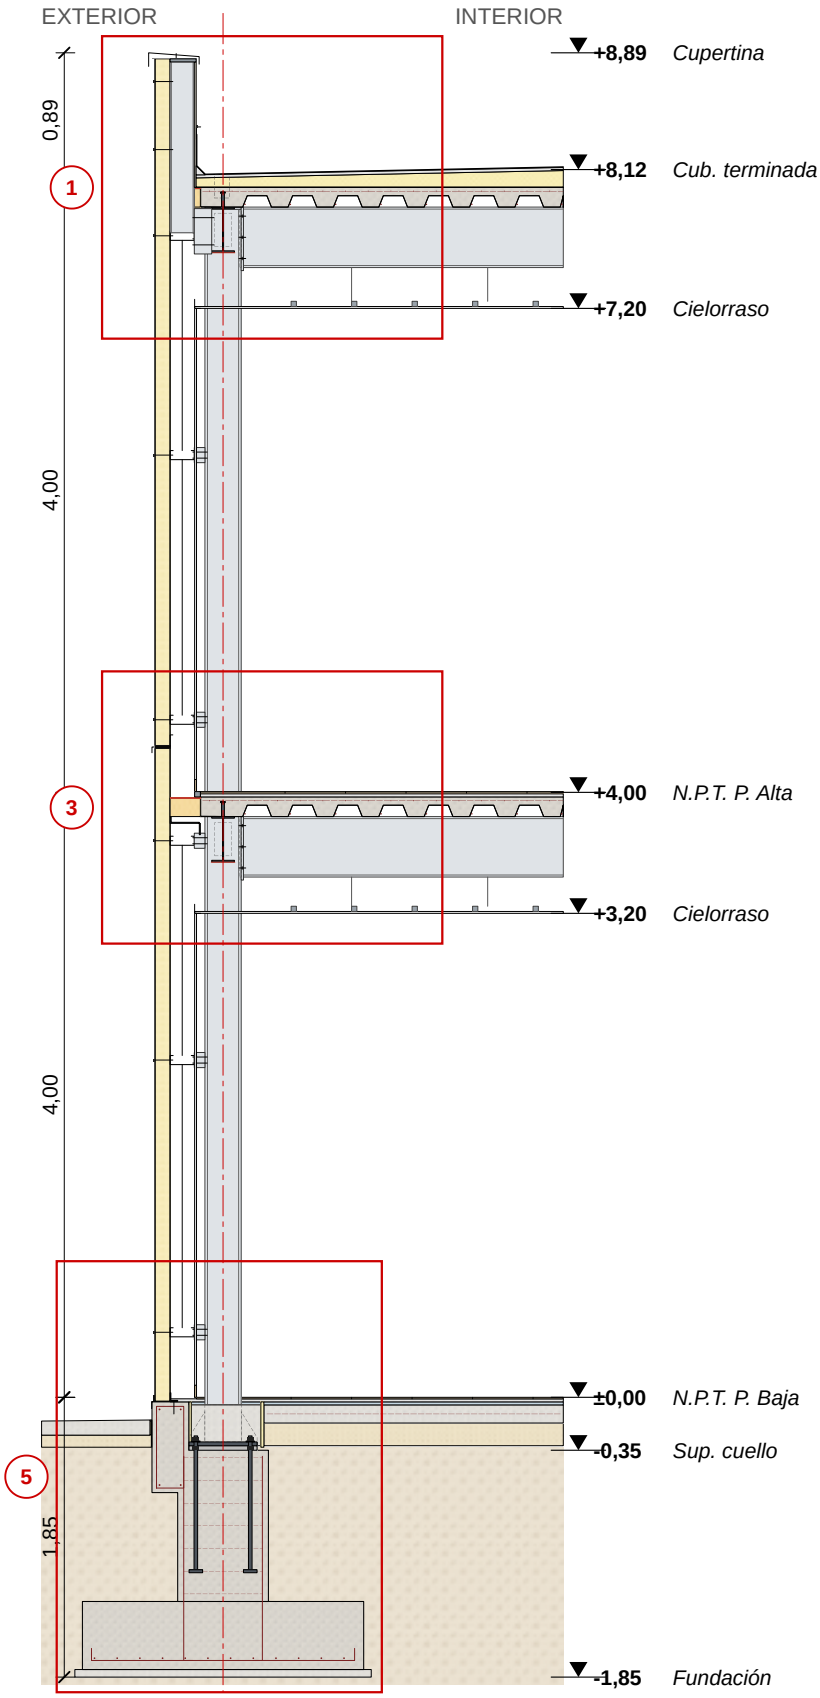

ESTRUCTURA
Columnas HEB 240 (F-24) c/ placa base 450x450x25, cartelas y 4 pernos de anclaje Ø24 + grout 30 mm, s/ cuello 60x60 y zapata 1,80x1,80x0,45 de H°A.
Vigas principales IPE 400 c/ 2,50 m (placa extrema 20 mm + 6 M20 8.8 al ala de la columna).
Vigas de borde IPE 300 (doble ángulo L 90x90x9 + M16 al alma de la columna).
Losa colaborante: chapa trapezoidal galv. h 75 e 0,9 + H-25, e = 13 cm, malla Q188, conectores Nelson Ø19 c/30.
Arriostramiento vertical en cruz (fuera del corte).
Antióxido + pintura intumescente F60.

CERRAMIENTO
Panel sándwich metálico PIR 100 vertical, atornillado a correas C 160x60x20x2,5 galv. c/ 1,45–1,80 m, fijadas c/ clips a las columnas; tensores Ø10 a media luz.
Revestimiento interior placa de yeso 12,5.
Parapeto c/ montantes UPN 160 c/ 1,25 m y placa cementicia.

CUBIERTA
Barrera de vapor, contrapiso liviano c/ EPS pend. 2 % al parapeto, carpeta y membrana c/ aluminio; embudo y caño de lluvia interior.

NUDOS (en rojo)
Nudo 1: Cubierta · opaco · esc. 1:20
Nudo 3: Entrepiso · opaco · esc. 1:20
Nudo 5: Piso + fundación · opaco · esc. 1:20

Cotas y niveles en m s/ N.P.T. P. Baja ±0,00

PRÁCTICA EN CLASE · NUDOS Corte integral opaco - esc. 1:50	DOCENTE: Arq. Tucci y Arq. Cardozo ALUMNA: Candelaria Vitale GRUPO: 13	**CONSTRUCCIONES II · UNM** CÁTEDRA: ARQ. TUCCI FECHA: 22/10/2026	LÁMINA **02/19** **ESC. 1:50**