
CORTE INTEGRAL

ESTRUCTURA DE ACERO · CERRAMIENTO VIDRIADO · ESCALA 1:50

Corte vertical entre columnas; fundación cortada por el eje de columna. Base de los 6 nudos 1:20.

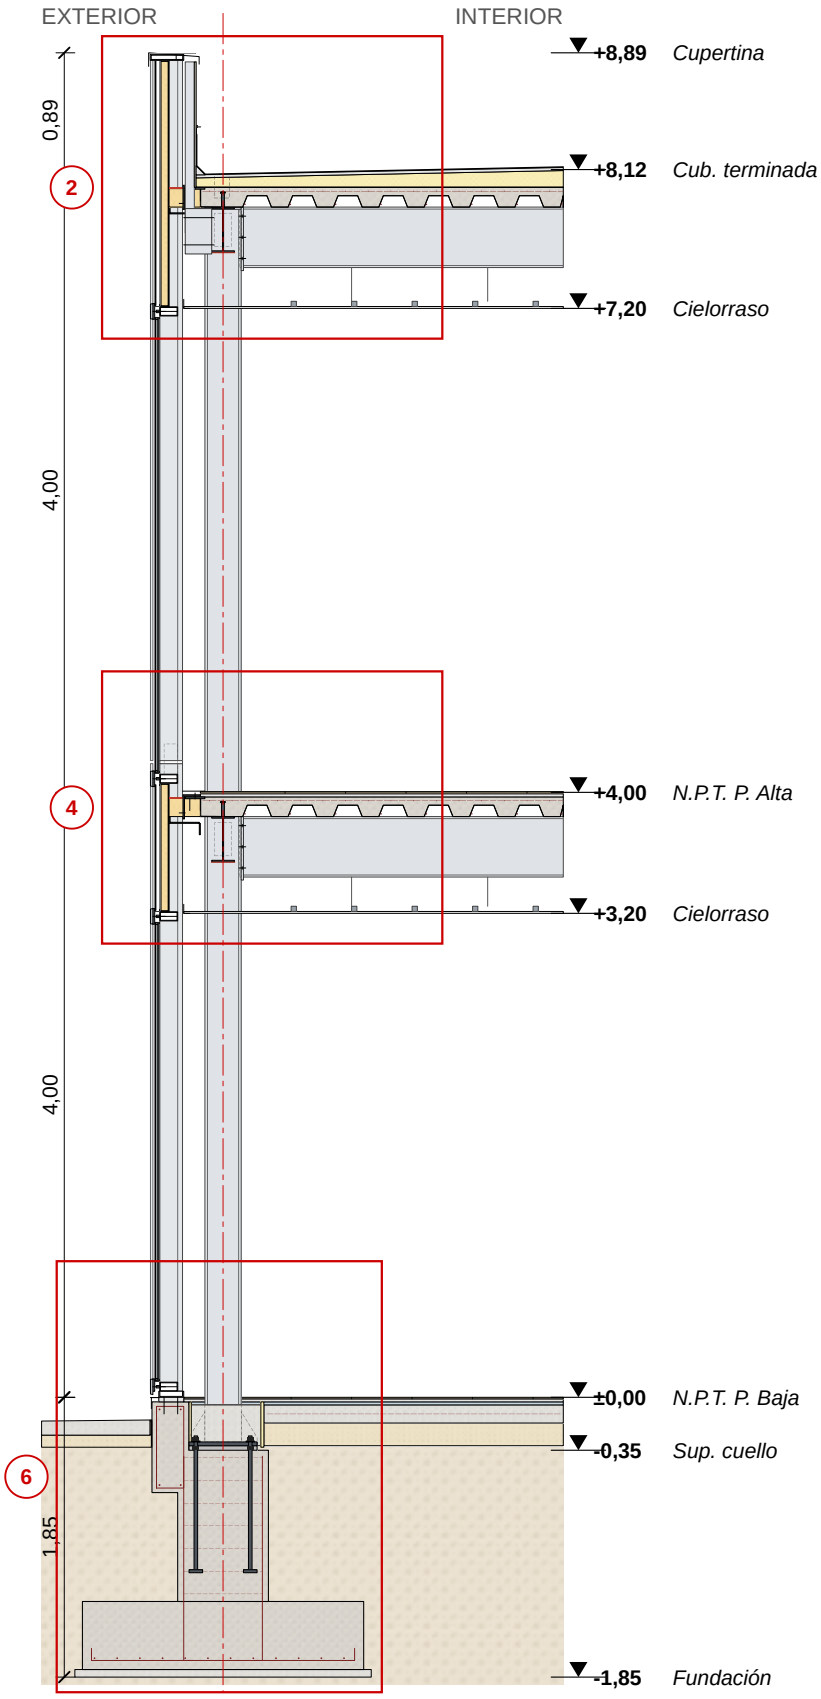

ESTRUCTURA

Columnas HEB 240 (F-24) c/ placa base 450x450x25, cartelas y 4 pernos de anclaje Ø24 + grout 30 mm, s/ cuello 60x60 y zapata 1,80x1,80x0,45 de H°A.
Vigas principales IPE 400 c/ 2,50 m (placa extrema 20 mm + 6 M20 8.8 al ala de la columna).
Vigas de borde IPE 300 (doble ángulo L 90x90x9 + M16 al alma de la columna).
Losa colaborante: chapa trapezoidal galv. h 75 e 0,9 + H-25, e = 13 cm, malla Q188, conectores Nelson Ø19 c/30.
Arriostramiento vertical en cruz (fuera del corte).
Antióxido + pintura intumescente F60.

CERRAMIENTO

Muro cortina stick de aluminio (montante 50x150) c/ DVH 6+12+3+3 y spandrel esmaltado c/ bandeja de lana.
Montantes colgados de cada losa c/ grapa regulable s/ placa embebida; junta de dilatación 20 mm c/ manguito; guía deslizante en PB.

CUBIERTA

Barrera de vapor, contrapiso liviano c/ EPS pend. 2 % al parapeto, carpeta y membrana c/ aluminio; embudo y caño de lluvia interior.

NUDOS (en rojo)

Nudo 2: Cubierta · vidriado · esc. 1:20
Nudo 4: Entrepiso · vidriado · esc. 1:20
Nudo 6: Piso + fundación · vidriado · esc. 1:20

Cotas y niveles en m s/ N.P.T. P. Baja ±0,00

PRÁCTICA EN CLASE · NUDOS Corte integral vidriado - esc. 1:50	DOCENTE: Arq. Tucci y Arq. Cardozo ALUMNA: Candelaria Vitale GRUPO: 13	**CONSTRUCCIONES II · UNM** CÁTEDRA: ARQ. TUCCI FECHA: 22/10/2026	LÁMINA **03/19** **ESC. 1:50**