
NUDO 1 CUBIERTA CON CERRAMIENTO EXTERIOR OPACO

Corte vertical entre columnas (columna y viga IPE 400 en vista) · ESCALA 1:20

Panel sándwich metálico PIR 100 s/ correas C 160 · parapeto c/ montantes UPN 160 · losa colaborante s/ IPE 400 / IPE 300

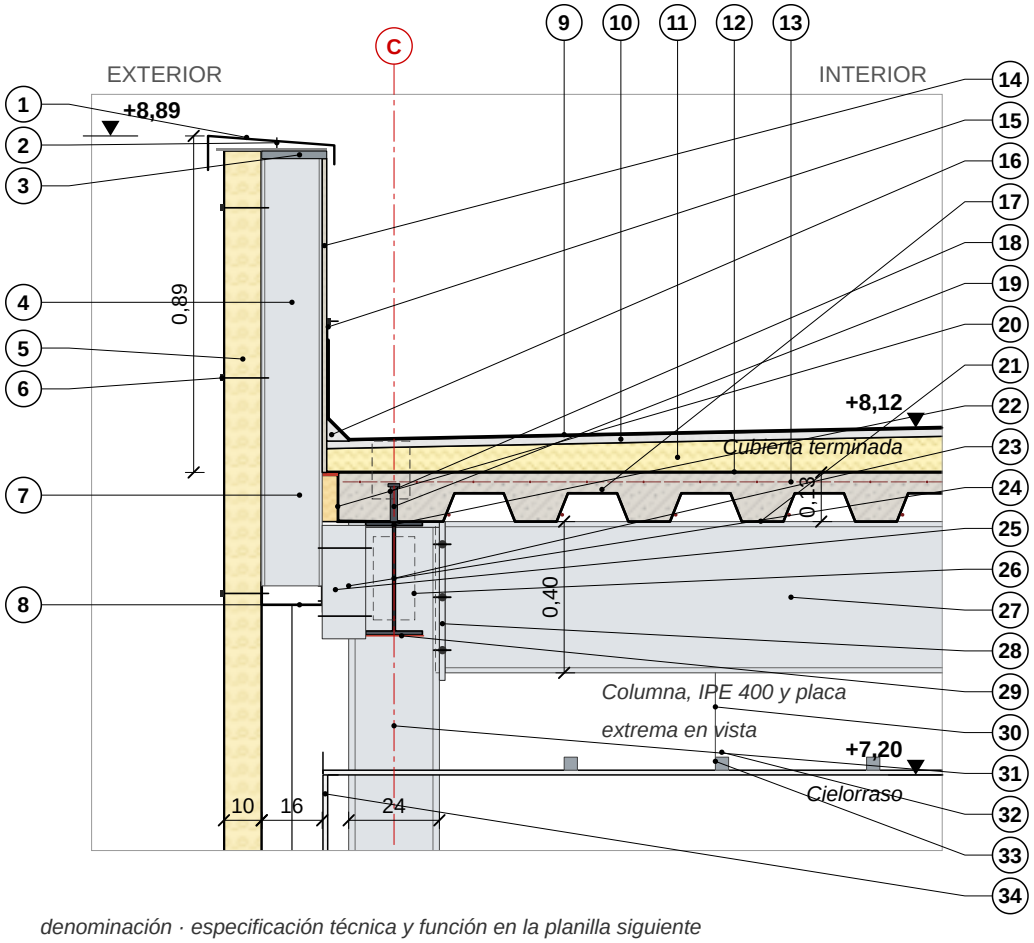

REFERENCIAS *denominación · especificación técnica y función en la planilla siguiente*

1 Cupertina
2 Fijación de la cupertina
3 Solera de coronamiento
4 Montante de parapeto UPN 160 (en vista)
5 Panel sándwich metálico
6 Fijación del panel
7 Barrera cortafuego de borde de losa
8 Correa de fachada
9 Membrana hidrófuga
10 Carpeta de asiento
11 Contrapiso de pendiente (aislante)
12 Barrera de vapor
13 Malla de repartición
14 Revestimiento interior del parapeto
15 Babeta
16 Media caña
17 Losa de hormigón
18 Embudo de desagüe (oculto)
19 Conector de corte
20 Frentín de borde (pour stop)
21 Chapa colaborante (steel deck)
22 Placa de cierre de columna
23 Viga de borde IPE 300
24 Ménsula de parapeto
25 Ángulo de clip
26 Unión viga de borde / columna (oculta)
27 Viga principal IPE 400 (en vista)
28 Unión viga principal / columna
29 Protección contra fuego y corrosión
30 Velas de cuelgue
31 Columna HEB 240 (en vista)
32 Estructura del cielorraso
33 Cielorraso suspendido
34 Revestimiento interior

ESCALA GRÁFICA 1:20

0 0,50 1,00 m

Cotas en m (secciones en cm) · niveles en m s/ N.P.T. P. Baja ±0,00

Estructura de acero (perfiles laminados) + losa colaborante · corte integral láms. 02–03

PRÁCTICA EN CLASE · NUDOS Nudo 1: Cubierta con cerramiento exterior opaco - corte 1:20	DOCENTE: Arq. Tucci y Arq. Cardozo ALUMNA: Candelaria Vitale GRUPO: 13	**CONSTRUCCIONES II · UNM** CÁTEDRA: ARQ. TUCCI FECHA: 22/10/2026	LÁMINA **04/19** **ESC. 1:20**