
NUDO 2 CUBIERTA CON CERRAMIENTO EXTERIOR VIDRIADO

Corte vertical entre columnas (columna y viga IPE 400 en vista) · ESCALA 1:20

Muro cortina stick (aluminio + DVH) colgado c/ grapas s/ placa embebida · parapeto c/ montantes tubo · losa colaborante

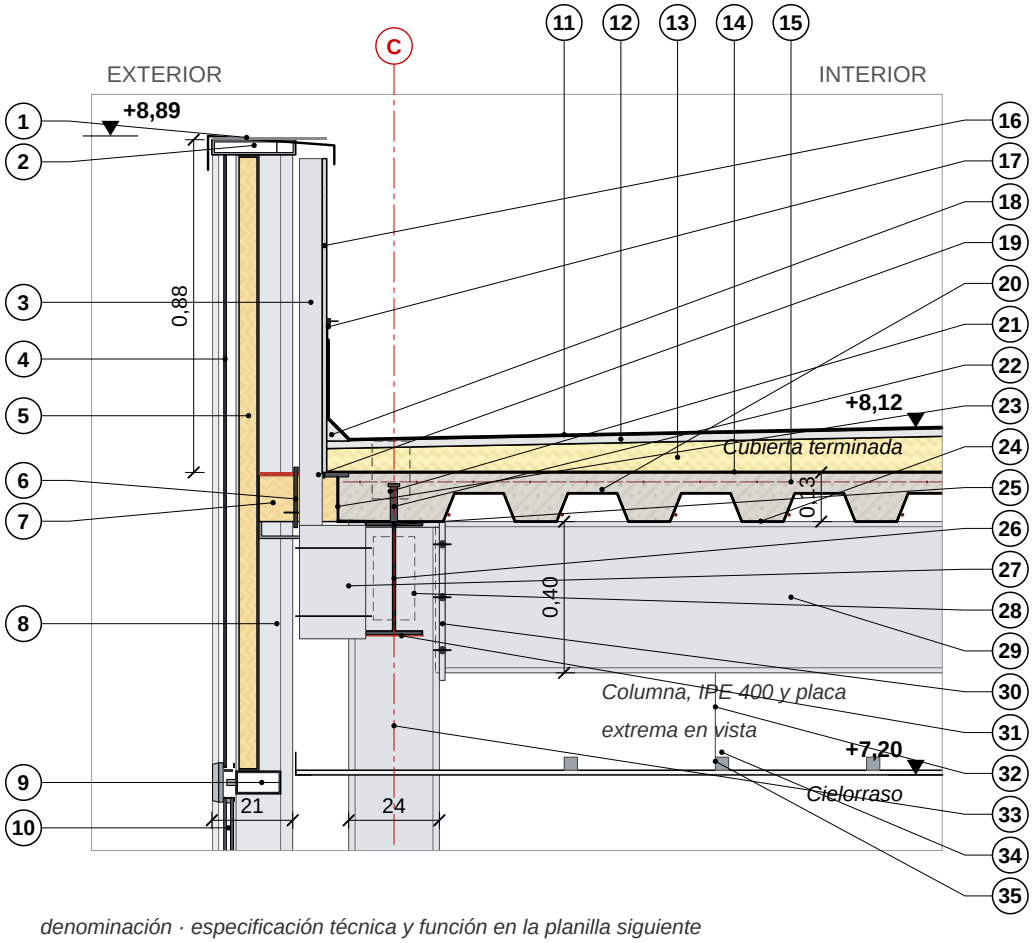

REFERENCIAS *denominación · especificación técnica y función en la planilla siguiente*

1 Cupertina
2 Perfil de cierre superior
3 Montante de parapeto (en vista)
4 Spandrel
5 Bandeja aislante
6 Grapa de anclaje (en vista)
7 Barrera cortafuego de borde de losa
8 Montante (mullion)
9 Travesaño + presor + tapa
10 Doble vidriado hermético (DVH)
11 Membrana hidrófuga
12 Carpeta de asiento
13 Contrapiso de pendiente (aislante)
14 Barrera de vapor
15 Malla de repartición
16 Revestimiento interior del parapeto
17 Babeta
18 Media caña
19 Placa de anclaje embebida
20 Losa de hormigón
21 Embudo de desagüe (oculto)
22 Conector de corte
23 Frentín de borde (pour stop)
24 Chapa colaborante (steel deck)
25 Placa de cierre de columna
26 Viga de borde IPE 300
27 Ménsula de parapeto
28 Unión viga de borde / columna (oculta)
29 Viga principal IPE 400 (en vista)
30 Unión viga principal / columna
31 Protección contra fuego y corrosión
32 Velas de cuelgue
33 Columna HEB 240 (en vista)
34 Estructura del cielorraso
35 Cielorraso suspendido

ESCALA GRÁFICA 1:20

0 0,50 1,00 m

Cotas en m (secciones en cm) · niveles en m s/ N.P.T. P. Baja ±0,00

Estructura de acero (perfiles laminados) + losa colaborante · corte integral láms. 02–03

PRÁCTICA EN CLASE · NUDOS Nudo 2: Cubierta con cerramiento exterior vidriado - corte 1:20	DOCENTE: Arq. Tucci y Arq. Cardozo ALUMNA: Candelaria Vitale GRUPO: 13	**CONSTRUCCIONES II · UNM** CÁTEDRA: ARQ. TUCCI FECHA: 22/10/2026	LÁMINA **07/19** **ESC. 1:20**