
NUDO 3 — ENTREPISO CON CERRAMIENTO EXTERIOR OPACO

Corte vertical entre columnas (columna y viga IPE 400 en vista) · ESCALA 1:20

Correas C 160 fijadas a las columnas c/ clips · barrera cortafuego en el borde de losa · losa colaborante + IPE 300 / IPE 400

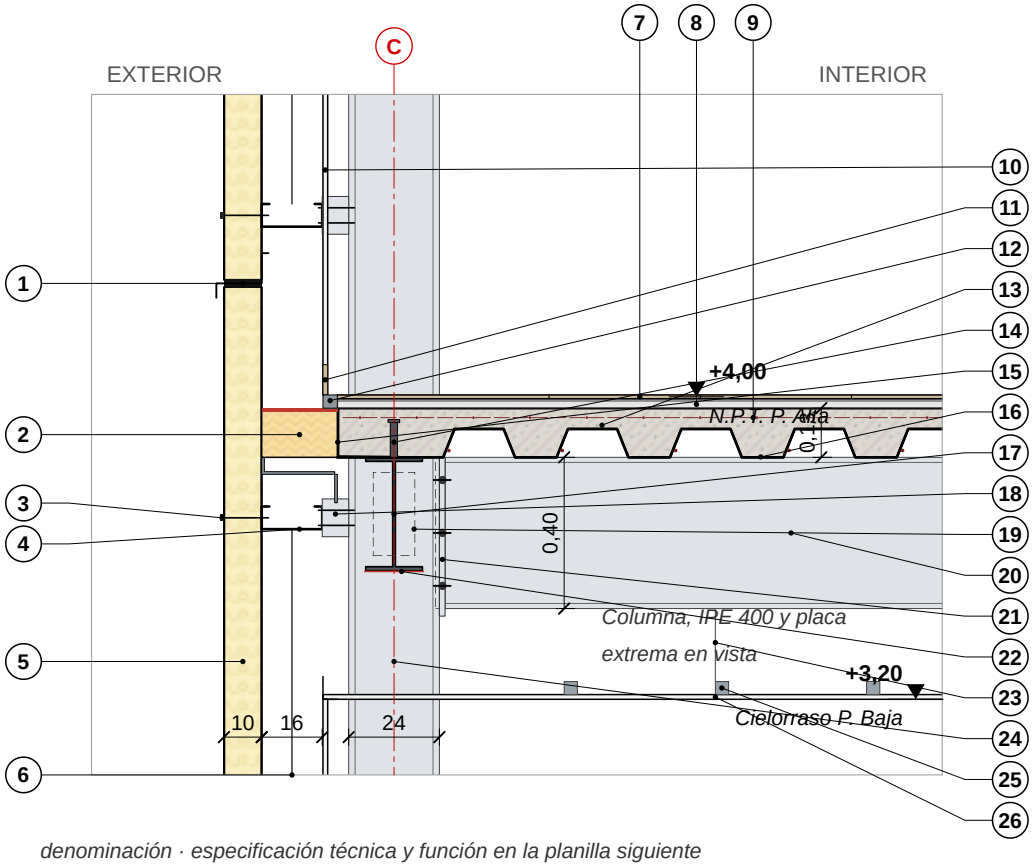

REFERENCIAS *denominación · especificación técnica y función en la planilla siguiente*

1 Junta horizontal del panel
2 Barrera cortafuego de borde de losa
3 Fijación del panel
4 Correa de fachada
5 Panel sándwich metálico
6 Tensor de correas
7 Solado
8 Carpeta niveladora
9 Malla de repartición
10 Revestimiento interior
11 Zócalo
12 Solera / cubrejunta de borde
13 Losa de hormigón
14 Conector de corte
15 Frentín de borde (pour stop)
16 Chapa colaborante (steel deck)
17 Viga de borde IPE 300
18 Ángulo de clip
19 Unión viga de borde / columna (oculta)
20 Viga principal IPE 400 (en vista)
21 Unión viga principal / columna
22 Protección contra fuego y corrosión
23 Velas de cuelgue
24 Columna HEB 240 (en vista)
25 Estructura del cielorraso
26 Cielorraso suspendido

ESCALA GRÁFICA 1:20

0 — 0,50 — 1,00 m

Cotas en m (secciones en cm) · niveles en m s/ N.P.T. P. Baja ±0,00

Estructura de acero (perfiles laminados) + losa colaborante · corte integral láms. 02–03

PRÁCTICA EN CLASE · NUDOS Nudo 3: Entrepiso con cerramiento exterior opaco - corte 1:20	DOCENTE: Arq. Tucci y Arq. Cardozo ALUMNA: Candelaria Vitale GRUPO: 13	**CONSTRUCCIONES II · UNM** CÁTEDRA: ARQ. TUCCI FECHA: 22/10/2026	LÁMINA **10/19** **ESC. 1:20**