
NUDO 4 ENTREPISO CON CERRAMIENTO EXTERIOR VIDRIADO

Corte vertical entre columnas (columna y viga IPE 400 en vista) · ESCALA 1:20

Muro cortina: grapa s/ placa embebida en la losa, junta de dilatación del montante y barrera cortafuego en el borde de losa

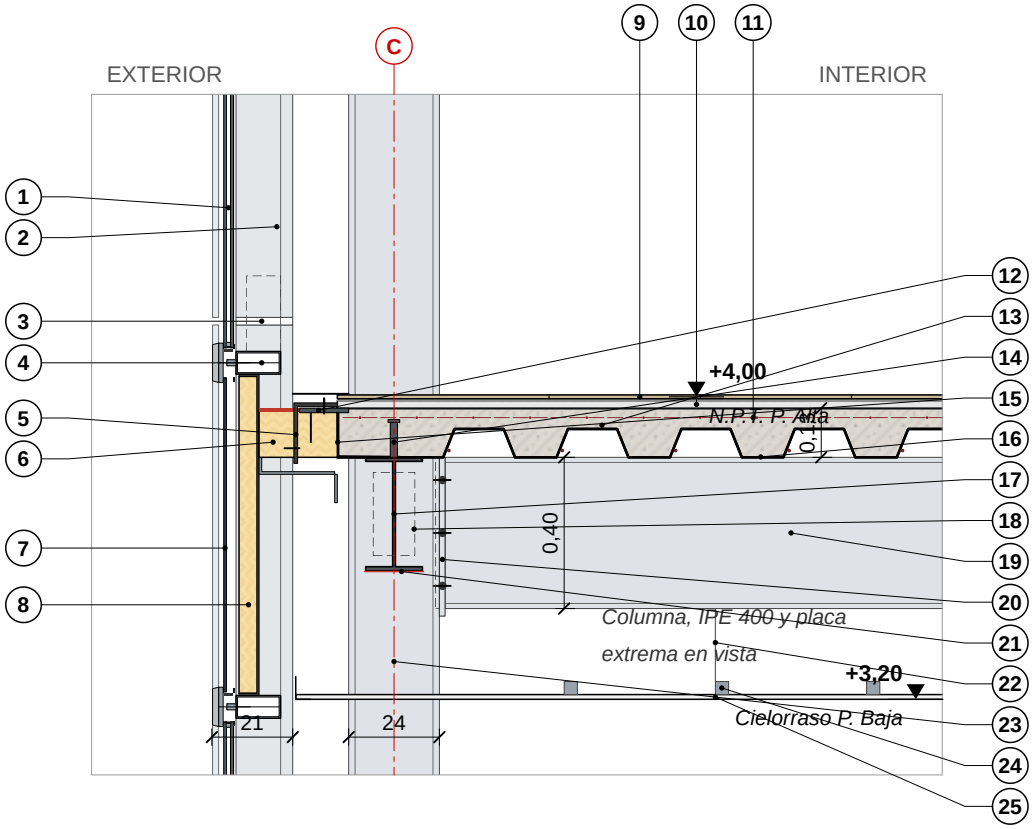

REFERENCIAS *denominación · especificación técnica y función en la planilla siguiente*

1 Doble vidriado hermético (DVH)
2 Montante (mullion)
3 Junta de dilatación del montante
4 Travesaño + presor + tapa
5 Grapa de anclaje (en vista)
6 Barrera cortafuego de borde de losa
7 Spandrel
8 Bandeja aislante
9 Solado
10 Carpeta niveladora
11 Malla de repartición
12 Placa de anclaje embebida
13 Losa de hormigón
14 Conector de corte
15 Frentín de borde (pour stop)
16 Chapa colaborante (steel deck)
17 Viga de borde IPE 300
18 Unión viga de borde / columna (oculta)
19 Viga principal IPE 400 (en vista)
20 Unión viga principal / columna
21 Protección contra fuego y corrosión
22 Velas de cuelgue
23 Columna HEB 240 (en vista)
24 Estructura del cielorraso
25 Cielorraso suspendido

ESCALA GRÁFICA 1:20

0 0,50 1,00 m

Cotas en m (secciones en cm) · niveles en m s/ N.P.T. P. Baja ±0,00

Estructura de acero (perfiles laminados) + losa colaborante · corte integral láms. 02–03

PRÁCTICA EN CLASE · NUDOS Nudo 4: Entrepiso con cerramiento exterior vidriado - corte 1:20	DOCENTE: Arq. Tucci y Arq. Cardozo ALUMNA: Candelaria Vitale GRUPO: 13	**CONSTRUCCIONES II · UNM** CÁTEDRA: ARQ. TUCCI FECHA: 22/10/2026	LÁMINA **12/19** **ESC. 1:20**