
NUDO 5

PISO SOBRE TERRENO NATURAL CON CERRAMIENTO EXTERIOR OPACO Y FUNDACIÓN

Corte vertical entre columnas (columna y viga IPE 400 en vista) · ESCALA 1:20

Panel s/ perfil de arranque en viga de fundación · placa base c/ pernos de anclaje y grout s/ cuello y zapata de H°A

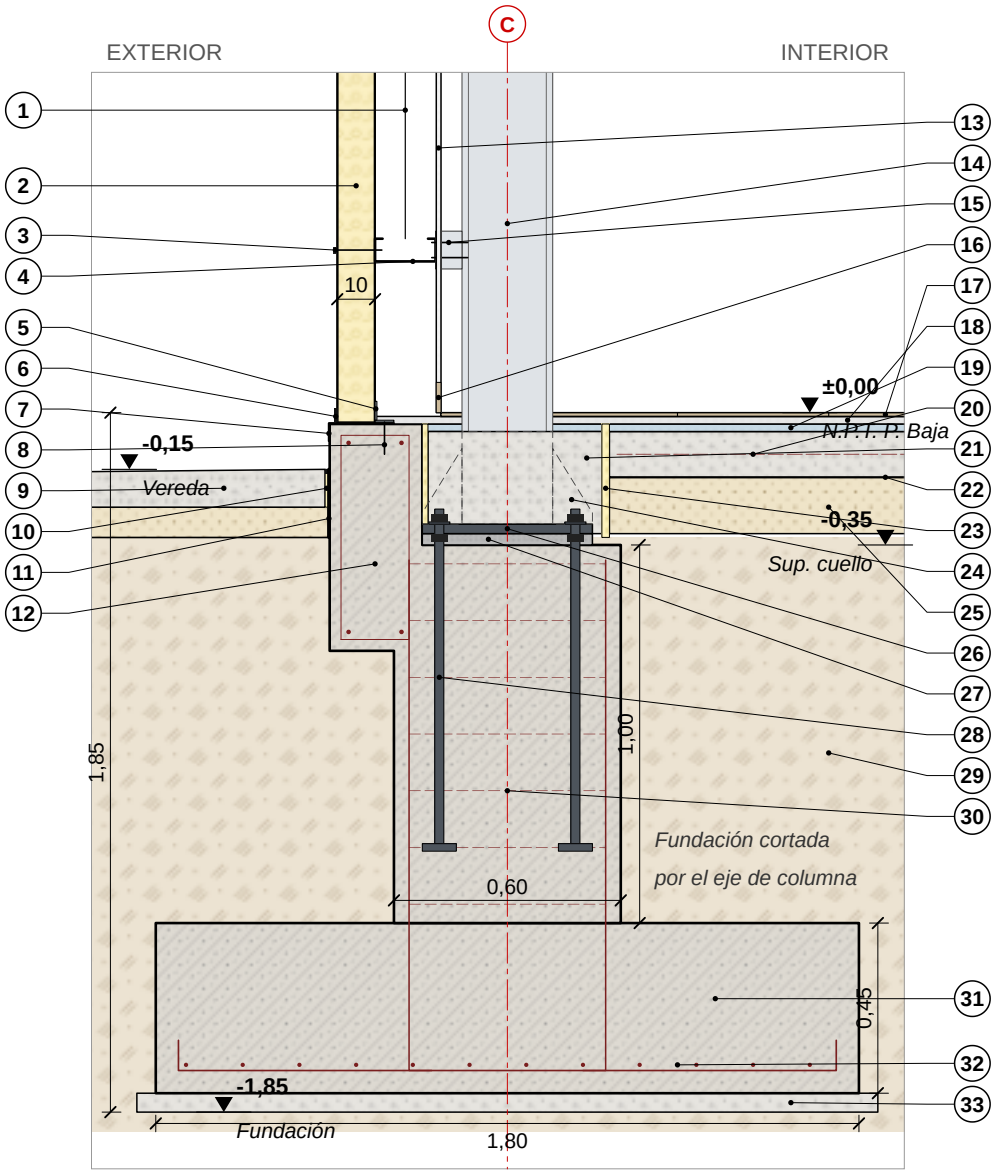

REFERENCIAS *denominación · especificación técnica y función en la planilla siguiente*

1 Tensor de correas
2 Panel sándwich metálico
3 Fijación del panel
4 Correa de fachada
5 Perfil de arranque
6 Sellado del arranque
7 Babeta-goterón de arranque
8 Broca de fijación
9 Vereda perimetral
10 Junta vereda / viga
11 Protección de caras enterradas
12 Viga de fundación (encadenado)
13 Revestimiento interior
14 Columna HEB 240 (en vista)
15 Ángulo de clip
16 Zócalo
17 Solado
18 Carpeta niveladora
19 Carpeta hidrófuga
20 Contrapiso armado
21 Dado de protección
22 Film de polietileno
23 Junta de dilatación
24 Cartelas (ocultas en el dado)
25 Relleno compactado
26 Placa base
27 Mortero de nivelación (grout)
28 Pernos de anclaje
29 Terreno natural
30 Cuello (pedestal) de la base
31 Zapata aislada
32 Armadura de la zapata
33 Hormigón de limpieza

ESCALA GRÁFICA 1:20

0 — 0,50 — 1,00 m

Cotas en m (secciones en cm) · niveles en m s/ N.P.T. P. Baja ±0,00

Estructura de acero (perfiles laminados) + losa colaborante · corte integral láms. 02–03

PRÁCTICA EN CLASE · NUDOS Nudo 5: Piso sobre terreno natural con cerramiento exterior opaco y fundación - corte 1:20	DOCENTE: Arq. Tucci y Arq. Cardozo ALUMNA: Candelaria Vitale GRUPO: 13	**CONSTRUCCIONES II · UNM** CÁTEDRA: ARQ. TUCCI FECHA: 22/10/2026	LÁMINA **14/19** **ESC. 1:20**