
NUDO 6

PISO SOBRE TERRENO NATURAL CON CERRAMIENTO EXTERIOR VIDRIADO Y FUNDACIÓN

Corte vertical entre columnas (columna y viga IPE 400 en vista) · ESCALA 1:20

Muro cortina colgado del entrepiso c/ perfil guía deslizante · placa base c/ pernos de anclaje s/ cuello y zapata de H°A

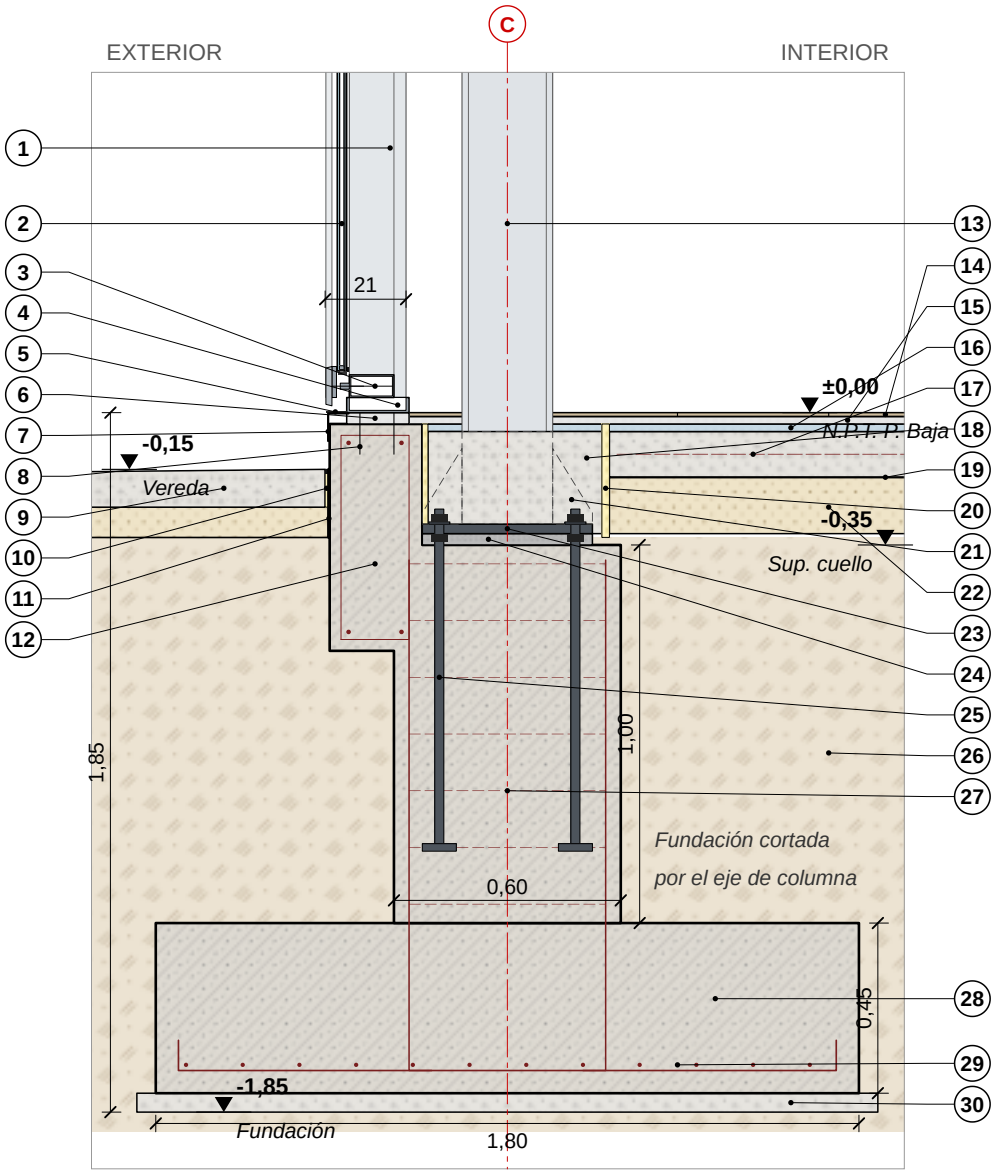

REFERENCIAS *denominación · especificación técnica y función en la planilla siguiente*

1 Montante de planta baja
2 Doble vidriado hermético (DVH)
3 Travesaño + presor + tapa
4 Perfil guía de arranque
5 Sellado perimetral
6 Suplemento de nivelación
7 Babeta-goterón de arranque
8 Broca de fijación
9 Vereda perimetral
10 Junta vereda / viga
11 Protección de caras enterradas
12 Viga de fundación (encadenado)
13 Columna HEB 240 (en vista)
14 Solado
15 Carpeta niveladora
16 Carpeta hidrófuga
17 Contrapiso armado
18 Dado de protección
19 Film de polietileno
20 Junta de dilatación
21 Cartelas (ocultas en el dado)
22 Relleno compactado
23 Placa base
24 Mortero de nivelación (grout)
25 Pernos de anclaje
26 Terreno natural
27 Cuello (pedestal) de la base
28 Zapata aislada
29 Armadura de la zapata
30 Hormigón de limpieza

ESCALA GRÁFICA 1:20

0 — 0,50 — 1,00 m

Cotas en m (secciones en cm) · niveles en m s/ N.P.T. P. Baja ±0,00

Estructura de acero (perfiles laminados) + losa colaborante · corte integral láms. 02–03

PRÁCTICA EN CLASE · NUDOS Nudo 6: Piso sobre terreno natural con cerramiento exterior vidriado y fundación - corte 1:20	DOCENTE: Arq. Tucci y Arq. Cardozo ALUMNA: Candelaria Vitale GRUPO: 13	**CONSTRUCCIONES II · UNM** CÁTEDRA: ARQ. TUCCI FECHA: 22/10/2026	LÁMINA **17/19** **ESC. 1:20**