
1° ELEMENTOS CONSTRUCTIVOS DEL SISTEMA

Axonometría estructural del edificio adoptado con la referencia de cada elemento

1 AXONOMETRÍA ESTRUCTURAL (ISOMÉTRICA)

ESC. 1:190

Ejes en rojo. Globos negros: N° de elemento (ver listado).

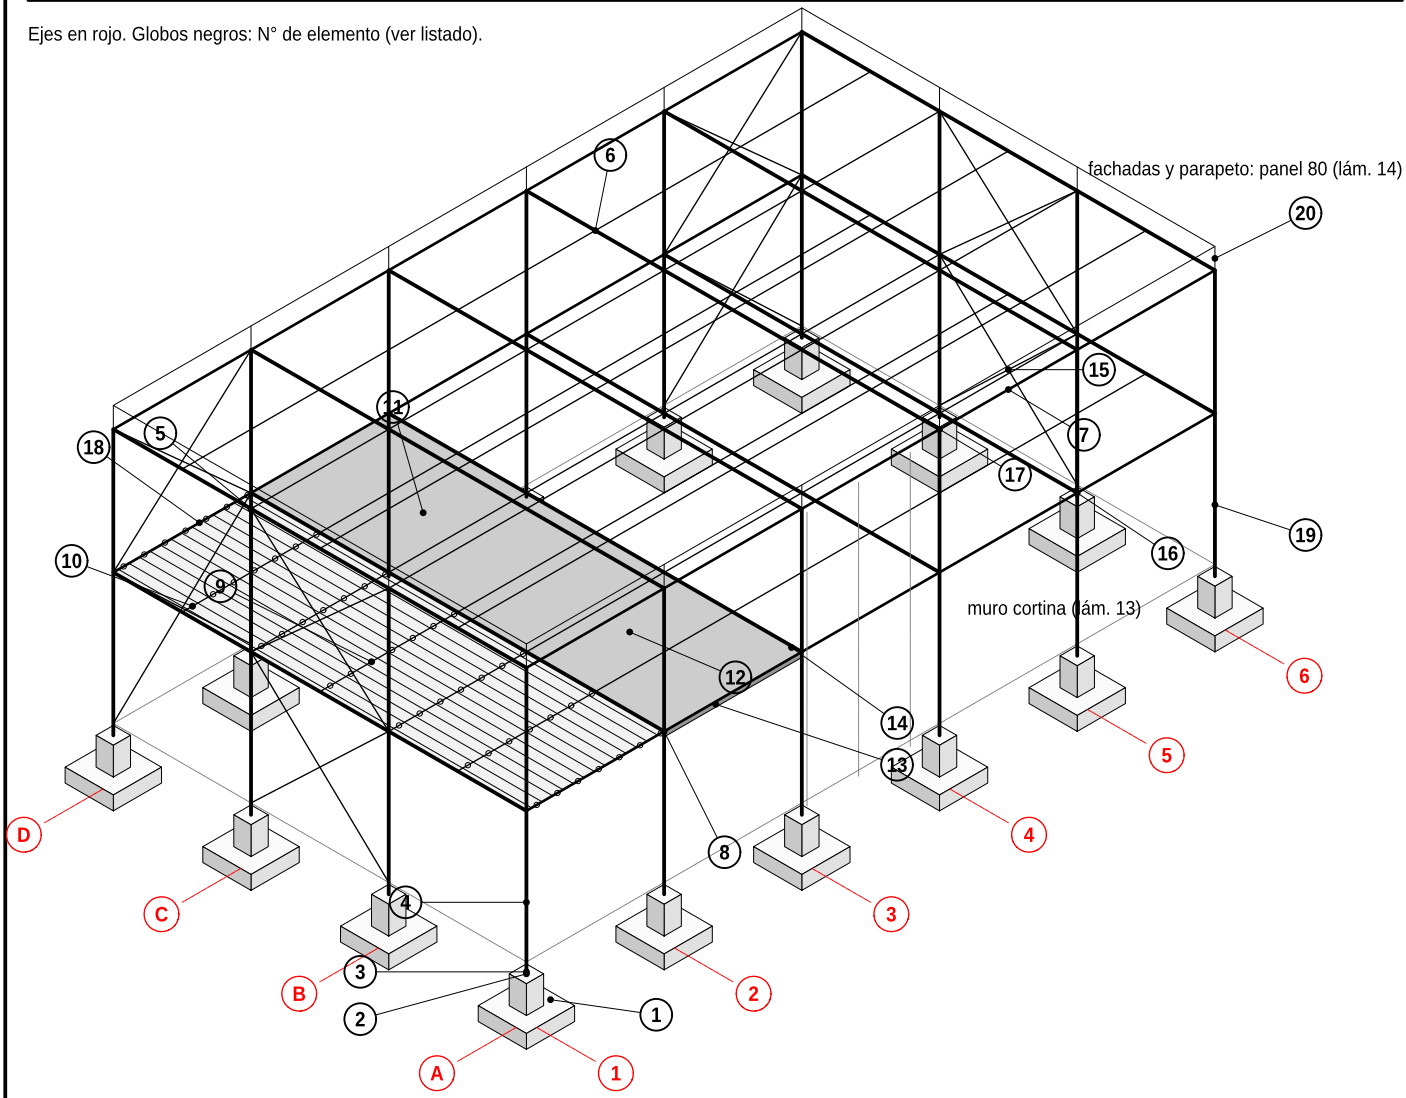

2 LISTADO DE ELEMENTOS DEL SISTEMA

N°	Elemento	Función	Lám.
1	Base aislada de H°A° con pedestal	Transmitir las cargas de la columna al suelo	03
2	Pernos de anclaje M20 (4 por columna)	Fijar la placa base a la fundación	03
3	Placa base 450x250x22 + mortero de nivelación	Repartir la carga y nivelar la columna	03
4	Columna IPN 300	Bajar cargas verticales; parte del pórtico	03
5	Viga principal IPN 500 (luz 12,00 m)	Salvar la gran luz; recibe las secundarias	04
6	Viga secundaria IPN 200 c/ 2,00 m	Apoyo de la chapa colaborante (luz 4,00 m)	04
7	Viga de borde IPN 200	Borde de losa; anclaje de los cerramientos	04
8	Placas de corte y angulares de unión	Vincular vigas entre sí y con columnas	04
9	Chapa colaborante h = 76 mm, e = 0,9 mm	Encofrado perdido y armadura inferior	05
10	Conectores de corte (stud Ø19 x 125)	Hacer trabajar juntos losa y viga	05

N°	Elemento	Función	Lám.
11	Malla Q188 + armadura de negativos	Retracción, temperatura y continuidad	05
12	Hormigón H-25 (losa e = 140 mm)	Losa de compresión; diafragma rígido	05
13	Cenefa de borde (chapa galv. e = 1,6)	Encofrado del borde de la losa	05
14	Tapas de cierre de nervios	Evitar fugas de hormigón en extremos	05
15	Arriostramiento: barra Ø20 + tensor	Estabilidad lateral (viento / sismo)	06
16	Bulones ISO 8.8 (ASTM A325) M16 / M20	Uniones abulonadas de obra	06
17	Soldadura (electrodo E7018)	Uniones de taller y studs	06
18	Fijaciones: clavos de pólvora / autoperforantes	Fijar y coser la chapa colaborante	06
19	Protección: antióxido + esmalte / intumescente	Corrosión y resistencia al fuego	06
20	Subestructura de fachada (montantes, portapanel)	Soporte de cerramientos	13/14

ESPECIFICACIONES GENERALES

Perfiles laminados IPN de acero F-24 (ASTM A36, fy = 240 MPa); chapas y placas F-24; bulones ISO 8.8; barras de anclaje F-24 roscadas; chapa colaborante de acero galvanizado Z275 (fy = 280 MPa); hormigón H-25; malla ADN 420. Todas las piezas se fabrican, perforan y pintan en taller y se montan en obra con uniones abulonadas (montaje en seco); en obra solo se suelda el conector de corte y se hormigona la losa.

ALUMNA: Vitale Candelaria
GRUPO: 13 (TP6 ACERO)
DOCENTES: Arq. Tucci y Arq. Cardozo

ESCALAS:
Axonometría isométrica 1:190
FECHA: 22/10/26
HOJA A4 - IMPRIMIR AL 100 %