
DETALLE 1 · UNIÓN COLUMNA – VIGA (ENTREPISO)

CORTE · ESC. 1:5

Corte integral, zona de entrepiso: viga "L" cortada; columna y ménsula en vista con rotura parcial en el bulón

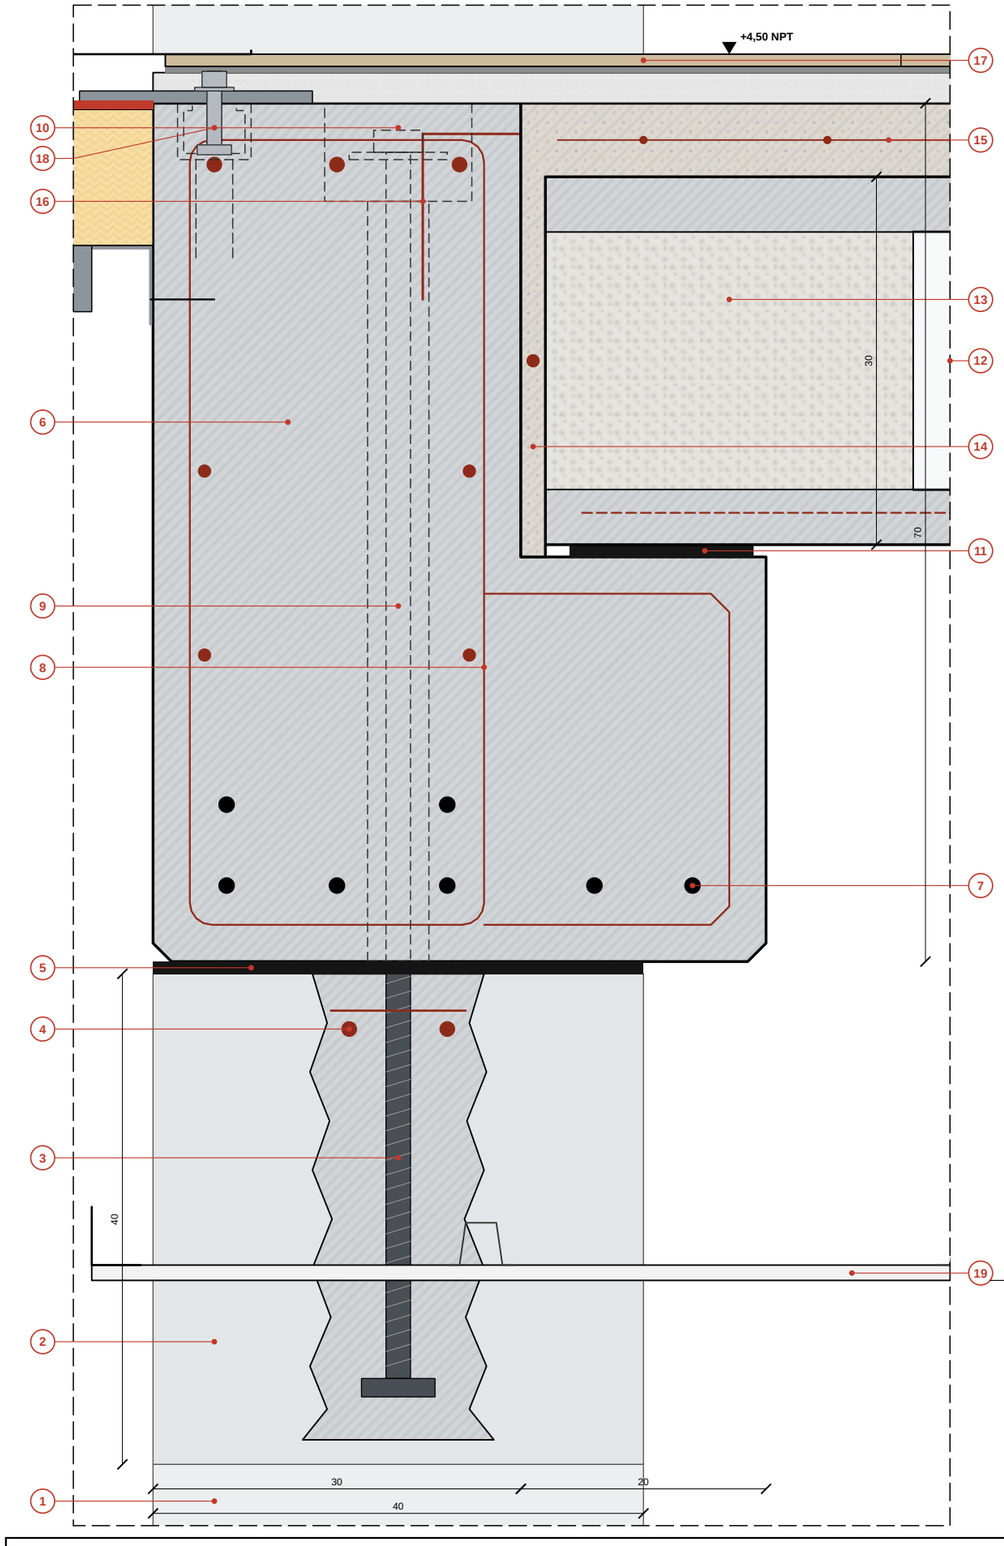


1 Columna premoldeada H°A° 40x40 H-30 (en vista).
2 Ménsula corta (en vista) c/ rotura parcial.
3 Bulón Ø20 anclado en la ménsula c/ placa de anclaje.
4 Armadura de la ménsula (Ø12 + estribos).
5 Apoyo de neopreno 10 mm ménsula / viga.
6 Viga "L" pretensada 30/70 c/ talón 20x33 (corte).
7 Cordones de pretensado Ø12,7.
8 Estribos Ø8 c/15 y barras Ø12 / Ø10 de piel.
9 Vaina corrugada Ø50 + bulón (oculto) llenado c/ grout.
10 Cajeado sup.: arandela + tuerca, llenado c/ grout.
11 Neopreno continuo losa / talón 10 mm.
12 Losa alveolar pretensada e = 30 cm (corte por alvéolo).
13 Tapón de H° en alvéolos (30 cm).
14 Junta viga–losa c/ H° in situ + barra Ø10.
15 Capa de compresión H°A° 6 cm c/ malla Q188.
16 Estribos salientes de la viga (vinculación).
17 Carpeta 2,5 cm + adhesivo + porcelanato.
18 Riel de anclaje tipo Halfen embutido (en vista).
19 Cielorraso placa de roca de yeso 12,5 s/ omegas.

DETALLE 3 · UNIÓN VIDRIO – VIGA DE ENTREPISO

CORTE · ESC. 1:5

Corte integral, borde de losa: grapa del montante, spandrel, barrera cortafuego

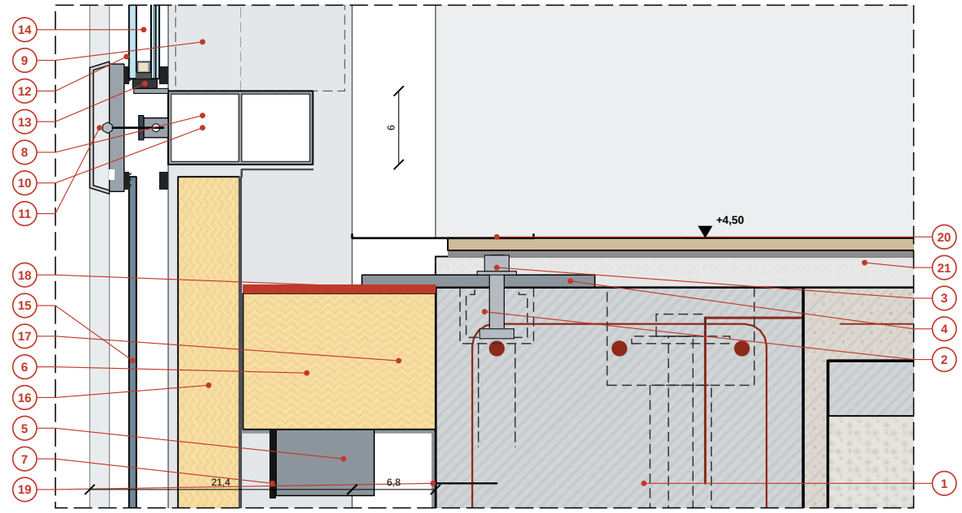


1 Viga "L" pretensada (borde de losa).
2 Riel Halfen embutido + pernos de anclaje (vista).
3 Bulón cabeza martillo M12 + arandela + tuerca.
4 Grapa acero galv. regulable 3D (ala horizontal).
5 Ala vertical frente al montante c/ coliso.
6 Bulón M12 inox pasante por el montante.
7 Separador aislante de neopreno (par galvánico).
8 Montante 50x150 (en vista).
9 Manguito interior de empalme (junta de dilatación 20 mm sobre +4,70).
10 Travesaño 50x120: cámaras, nariz y poliamida.
11 Presor + tornillo inox + tapa clipada.
12 Burletes EPDM exterior / interior.
13 Calzo EPDM s/ apoyo de vidrio.
14 DVH 6 + 12 + 3+3 laminado PVB.
15 Spandrel: vidrio templado 6 mm esmaltado.
16 Lana mineral 50 + bandeja chapa galv.
17 Barrera cortafuego: lana mineral 100 kg/m³.
18 Sellador intumescente.
19 Ángulo soporte chapa galv. atornillado a viga.
20 Cubrejunta aluminio.
21 Capa de compresión + carpeta + porcelanato.

DETALLE 2 · UNIÓN VIDRIO – MURO (PANEL)

CORTE · ESC. 1:5

Corte integral, remate superior: muro cortina contra panel premoldeado

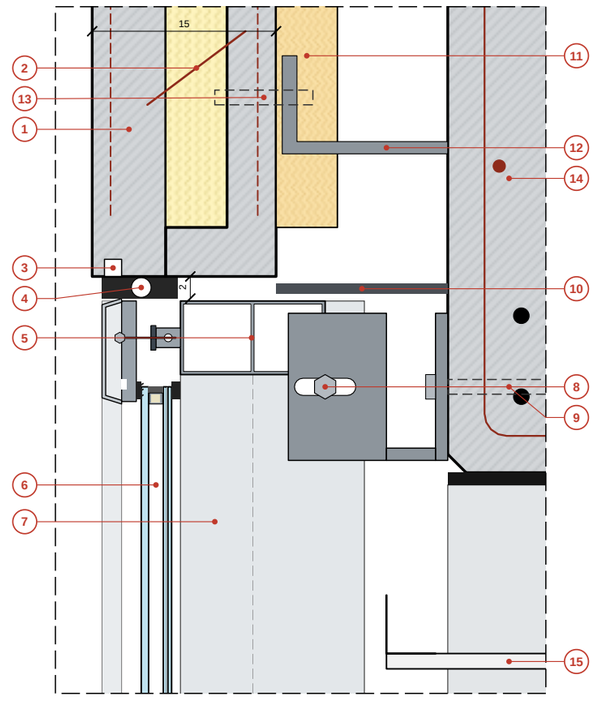

1 Panel sándwich premoldeado: H°A° 6 + EPS 5 + H°A° 4.
2 Conectores inox entre capas.
3 Goterón (buña 14x14).
4 Sellador silicona neutra + fondo de junta.
5 Travesaño superior + presor + tapa.
6 DVH 6 + 12 + 3+3 laminado.
7 Montante 50x150 (en vista).
8 Grapa superior c/ coliso + bulón M12.
9 Anclaje químico M12 a la viga.
10 Chapa galv. de cierre de cámara.
11 Lana mineral 50 mm en cámara.
12 Perfil L de restricción del panel.
13 Inserto roscado embutido en el panel.
14 Viga "L" de cubierta (corte).
15 Cielorraso placa de roca de yeso.

LÁMINA 3 · DETALLES DE UNIONES EN CORTE (del corte integral)

Sistema de hormigón premoldeado de grandes luces · Cerramiento vidriado – muro cortina (sistema stick, módulo 1,25 m)

Ventanas ampliadas del mismo corte integral de la Lámina 1 (mismo plano y cotas), a escala 1:5. Cotas en cm salvo indicación.

MATERIA	CÁTEDRA	ALUMNO/A	GRUPO	HOJA
Construcciones II	Arq. _____	_____	____	3 de 4 · A3 · 2026