CONSTRUCCIONES II · UNM

NUDOS

PRÁCTICA EN CLASE · HORMIGÓN PREMOLDEADO DE GRANDES LUCES

Nudos pertenecientes al proyecto del trabajo práctico, dibujados en forma proporcionada a escala 1:20, con referencias que incluyen función, denominación y especificación técnica de los materiales.

ÍNDICE DE LÁMINAS (A4)

01	Carátula, consigna e índice; ubicación de los nudos en los cortes integrales	1:100
02	Nudo 1: Cubierta con cerramiento exterior opaco	1:20
03	Nudo 1: planilla de referencias	—
04	Nudo 2: Cubierta con cerramiento exterior vidriado	1:20
05	Nudo 2: planilla de referencias	—
06	Nudo 3: Entrepiso con cerramiento exterior opaco	1:20
07	Nudo 3: planilla de referencias	—
08	Nudo 4: Entrepiso con cerramiento exterior vidriado	1:20
09	Nudo 4: planilla de referencias	—
10	Nudo 5: Piso sobre terreno natural con cerramiento exterior opaco y fundación	1:20
11	Nudo 5: planilla de referencias	—
12	Nudo 6: Piso sobre terreno natural con cerramiento exterior vidriado y fundación	1:20
13	Nudo 6: planilla de referencias	—

SISTEMA CONSTRUCTIVO

Estructura de hormigón premoldeado de grandes luces (sistema Pi): columnas 40x40 c/ ménsulas, vigas VL doble T pretensadas en fachada, vigas VP T invertida interiores y losas TT h 0,65 con capa de compresión in situ. Bases aisladas de H°A in situ con cuello (anclaje mecánico húmedo).

CERRAMIENTOS


Opaco: panel sándwich premoldeado de H°A (6 + EPS 6 + 8 cm) fijado a la VL con bulón pasante y apoyado en viga portapanel.
Vidriado: muro cortina stick de aluminio con DVH y spandrel, colgado de la estructura c/ grapas.

CONVENCIONES

- H° premoldeado (cortado)
- H°A in situ
- H° pobre / contrapiso
- EPS / H° liviano c/ EPS
- Lana mineral
- Terreno natural
- Vidrio
- Aluminio

CORTE INTEGRAL
CERRAMIENTO OPACO

CORTE INTEGRAL
CERRAMIENTO VIDRIADO

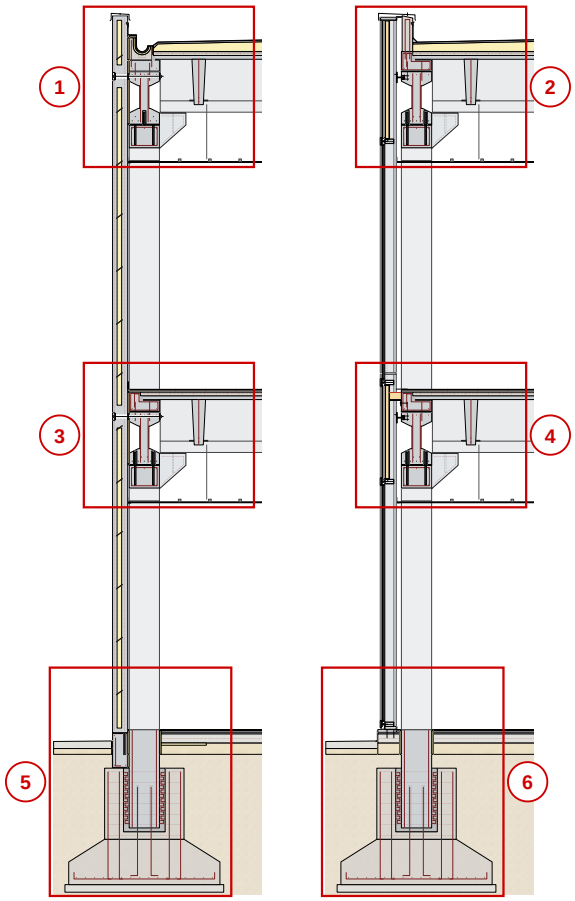

Cortes integrales esquemáticos esc. 1:100 · en rojo, el encuadre de cada nudo

PRÁCTICA EN CLASE · NUDOS Carátula, consigna e índice; ubicación de los nudos en los cortes integrales	DOCENTE: Arq. Tucci y Arq. Cardozo ALUMNA: Candelaria Vitale GRUPO: 13	**CONSTRUCCIONES II · UNM** CÁTEDRA: ARQ. TUCCI FECHA: 22/10/2026	LÁMINA **01/13** **ESC. 1:100**