
NUDO 1 — CUBIERTA CON CERRAMIENTO EXTERIOR OPACO

Corte vertical por la zona de apoyo de la viga VL · ESCALA 1:20

Panel sándwich premoldeado H°A como parapeto · canaleta H°A in situ · VL + viga de borde + losa TT

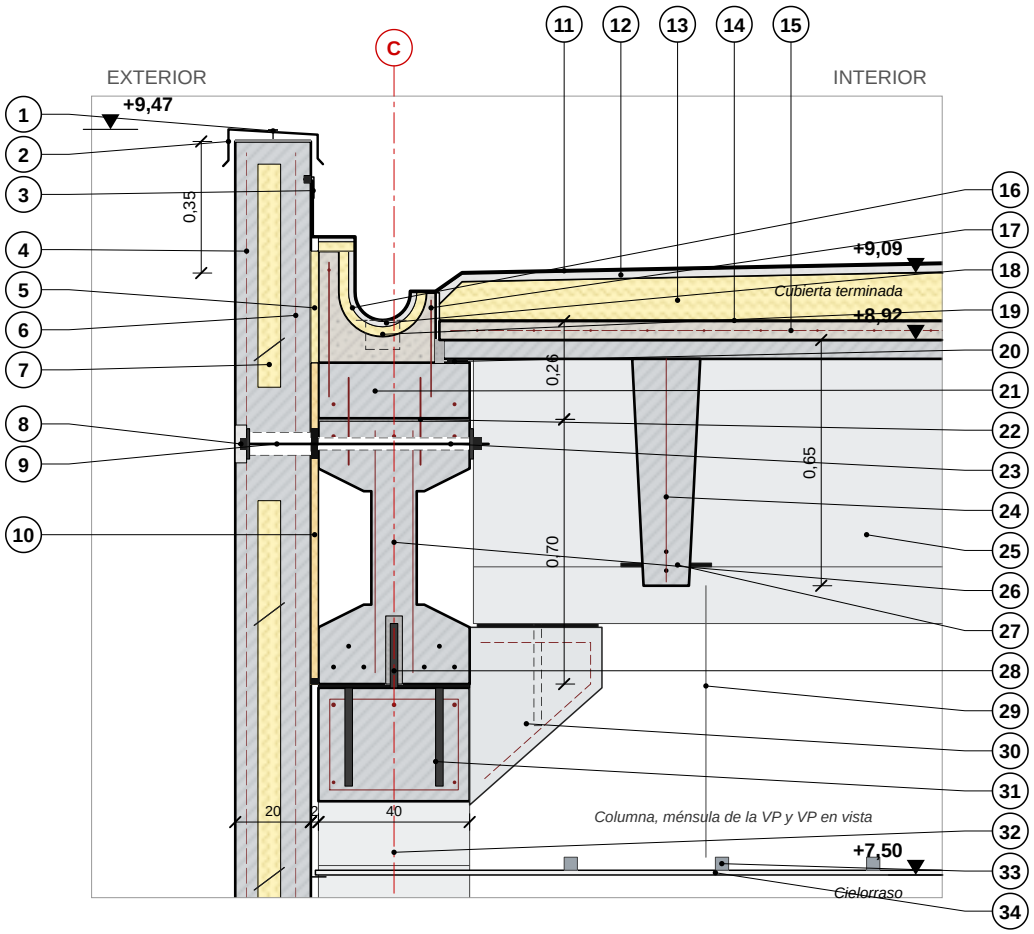

REFERENCIAS

denominación (especificación técnica y función: ver planilla de la lámina siguiente)

1 Fijación de la cupertina
2 Cupertina
3 Babeta
4 Panel sándwich premoldeado
5 Junta panel / canaleta
6 Hojas de hormigón del panel
7 Núcleo aislante del panel
8 Rehundido del anclaje
9 Agujero ovalado + vaina
10 Junta panel / estructura
11 Membrana hidrófuga
12 Carpeta de asiento
13 Contrapiso de pendiente (aislante)
14 Barrera de vapor
15 Capa de compresión
16 Aislación de la canaleta
17 Estribos salientes
18 Canaleta de desagüe
19 Embudo de desagüe (oculto)
20 Apoyo del ala del TT
21 Viga de borde
22 Junta VL / viga de borde
23 Bulón pasante (fija panel)
24 Losa premoldeada TT
25 Viga VP principal (en vista)
26 Viga VL perimetral
27 Apoyo nervio TT / VP
28 Neopreno + perno VL / ménsula
29 Velas de cuelgue
30 Apoyo de la VP (en vista)
31 Ménsula corta de columna
32 Columna premoldeada (en vista)
33 Estructura del cielorraso
34 Cielorraso suspendido

ESCALA GRÁFICA 1:20

0 — 0,50 — 1,00 m

Cotas en m (secciones en cm) · niveles en m respecto del N.P.T. P. Baja ±0,00

Hormigón premoldeado de grandes luces (sistema Pi) · mismo edificio del corte integral del TP

PRÁCTICA EN CLASE · NUDOS Nudo 1: Cubierta con cerramiento exterior opaco - corte 1:20	DOCENTE: Arq. Tucci y Arq. Cardozo ALUMNA: Candelaria Vitale GRUPO: 13	**CONSTRUCCIONES II · UNM** CÁTEDRA: ARQ. TUCCI FECHA: 22/10/2026	LÁMINA **02/13** **ESC. 1:20**