
# NUDO 2 — CUBIERTA CON CERRAMIENTO EXTERIOR VIDRIADO

Corte vertical por la zona de apoyo de la viga VL · ESCALA 1:20

*Muro cortina stick (aluminio + DVH) colgado de la estructura · zócalo H°A in situ · VL + viga L + losa TT*

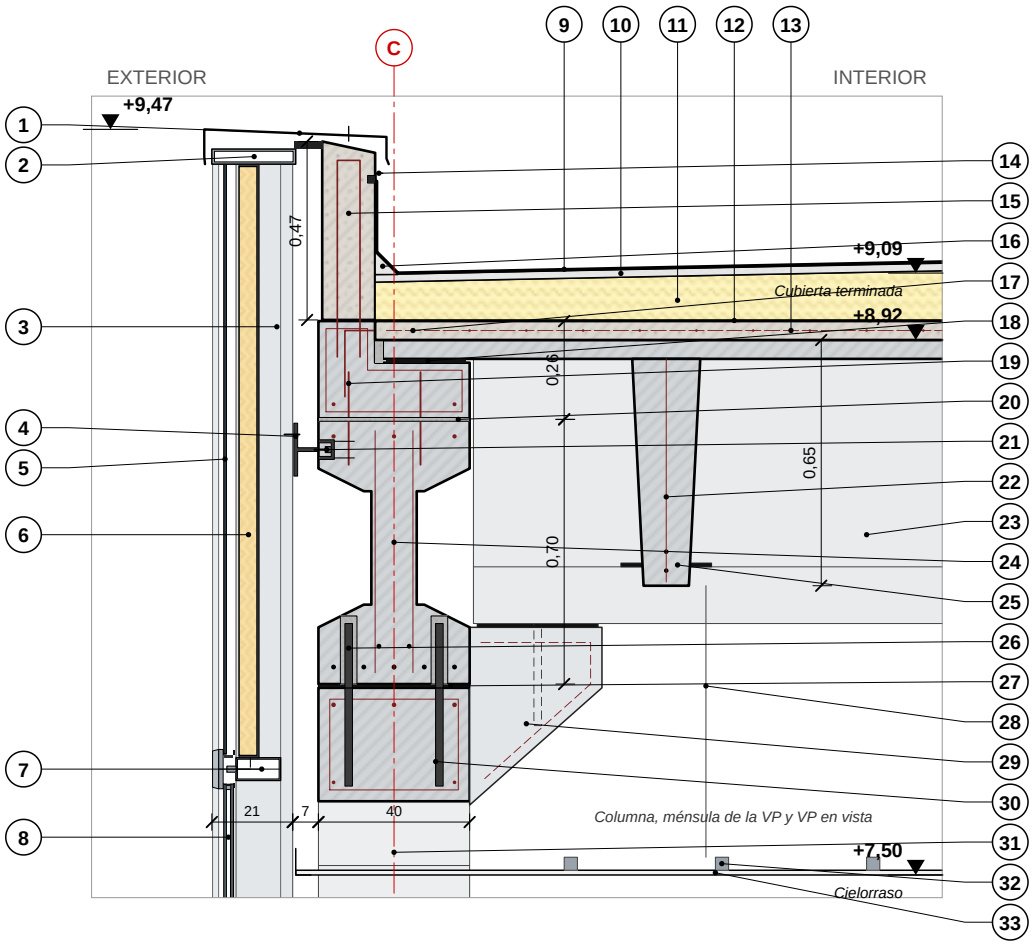


## REFERENCIAS

*denominación (especificación técnica y función: ver planilla de la lámina siguiente)*

**1** Cupertina
**2** Perfil de cierre superior del muro cortina
**3** Montante (mullion)
**4** Grapa de anclaje
**5** Spandrel
**6** Bandeja aislante
**7** Travesaño + presor + tapa
**8** Doble vidriado hermético (DVH)
**9** Membrana hidrófuga
**10** Carpeta de asiento
**11** Contrapiso de pendiente (aislante)
**12** Barrera de vapor
**13** Capa de compresión
**14** Babeta
**15** Zócalo / parapeto superior
**16** Media caña
**17** Estribos salientes
**18** Apoyo del ala del TT
**19** Viga L de borde
**20** Junta VL / viga de borde
**21** Riel de anclaje embutido
**22** Losa premoldeada TT
**23** Viga VP principal (en vista)
**24** Viga VL perimetral
**25** Apoyo nervio TT / VP
**26** Pernos de vinculación VL
**27** Apoyo elastomérico de la VL
**28** Velas de cuelgue
**29** Apoyo de la VP (en vista)
**30** Ménsula corta de columna
**31** Columna premoldeada (en vista)
**32** Estructura del cielorraso
**33** Cielorraso suspendido

**ESCALA GRÁFICA 1:20**

0 — 0,50 — 1,00 m

*Cotas en m (secciones en cm) · niveles en m respecto del N.P.T. P. Baja ±0,00*

*Hormigón premoldeado de grandes luces (sistema Pi) · mismo edificio del corte integral del TP*

| | | | |
|---|---|---|---|
| **PRÁCTICA EN CLASE · NUDOS**<br>Nudo 2: Cubierta con cerramiento exterior vidriado - corte 1:20 | DOCENTE: Arq. Tucci y Arq. Cardozo<br>ALUMNA: Candelaria Vitale<br>GRUPO: 13 | **CONSTRUCCIONES II · UNM**<br>CÁTEDRA: ARQ. TUCCI<br>FECHA: 22/10/2026 | LÁMINA **04/13**<br>**ESC. 1:20** |