
NUDO 3 ENTREPISO CON CERRAMIENTO EXTERIOR OPACO

Corte vertical por la zona de apoyo de la viga VL · ESCALA 1:20

Panel sándwich fijado a la VL con bulón pasante · viga L de borde + losa TT + capa de compresión

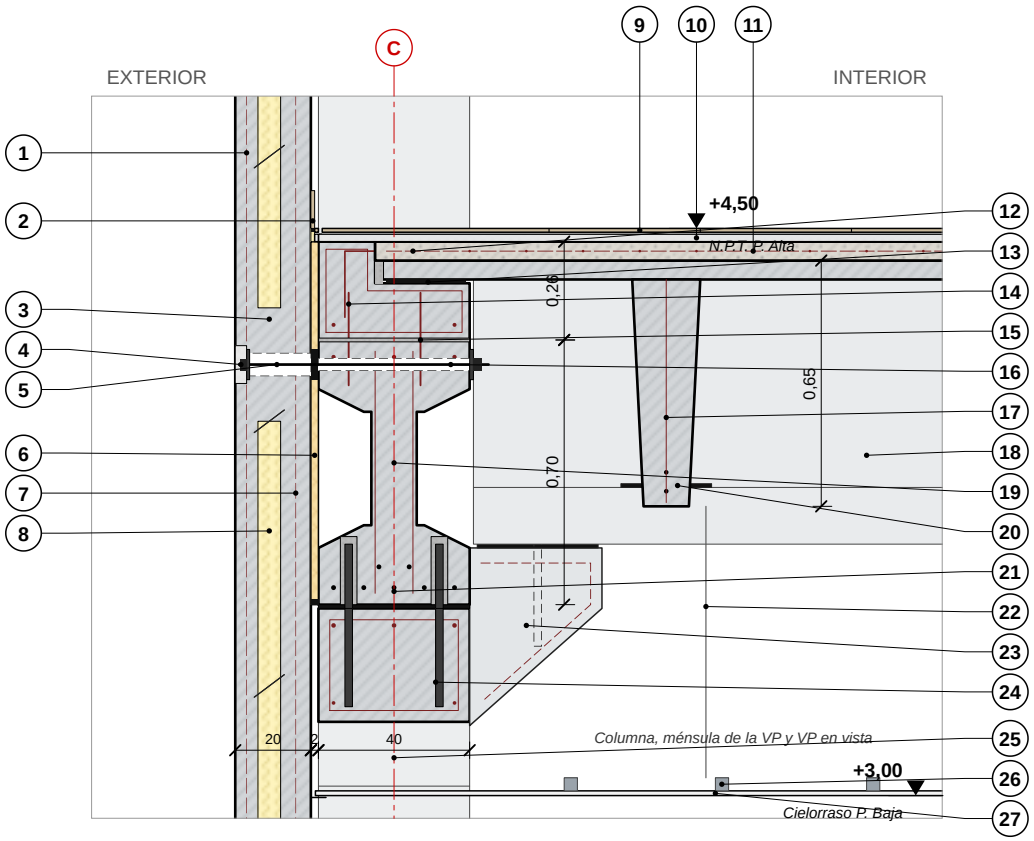

REFERENCIAS

denominación (especificación técnica y función: ver planilla de la lámina siguiente)

1 Panel sándwich premoldeado
2 Junta perimetral del piso
3 Zona maciza de anclaje
4 Rehundido del anclaje
5 Agujero ovalado + vaina
6 Junta panel / estructura
7 Hojas de hormigón del panel
8 Núcleo aislante del panel
9 Solado
10 Carpeta niveladora
11 Capa de compresión
12 Estribos salientes
13 Apoyo del ala del TT
14 Viga L de borde
15 Junta VL / viga de borde
16 Bulón pasante (fija panel)
17 Losa premoldeada TT
18 Viga VP principal (en vista)
19 Viga VL perimetral
20 Apoyo nervio TT / VP
21 Neopreno + perno VL / ménsula
22 Velas de cuelgue
23 Apoyo de la VP (en vista)
24 Ménsula corta de columna
25 Columna premoldeada (en vista)
26 Estructura del cielorraso
27 Cielorraso suspendido

ESCALA GRÁFICA 1:20

0 0,50 1,00 m

Cotas en m (secciones en cm) · niveles en m respecto del N.P.T. P. Baja ±0,00

Hormigón premoldeado de grandes luces (sistema Pi) · mismo edificio del corte integral del TP

PRÁCTICA EN CLASE · NUDOS Nudo 3: Entrepiso con cerramiento exterior opaco - corte 1:20	DOCENTE: Arq. Tucci y Arq. Cardozo ALUMNA: Candelaria Vitale GRUPO: 13	**CONSTRUCCIONES II · UNM** CÁTEDRA: ARQ. TUCCI FECHA: 22/10/2026	LÁMINA **06/13** **ESC. 1:20**