CORTE INTEGRAL CERRAMIENTO OPACO

ESCALA 1:20


Hormigón premoldeado de grandes luces
Panel sándwich de H°A · Sistema Pi (Astori)
Cerramiento integral: apoyado en la base,
vinculado a la estructura en cada nivel

REFERENCIAS

1 Cupertina chapa galv. N°22, pend. al interior, c/ goterones
2 Tornillo autoperforante c/ arandela de neopreno + sellador
3 Babeta chapa galv. en buña del panel + sellador PU
4 Membrana asfáltica 4 mm c/ aluminio, continua en canaleta
5 Carpeta de nivelación MCI 1:3, e = 2 cm
6 Contrapiso liviano H° c/ EPS, e mín. 6 cm, pend. 2 %
7 Aislación térmica: plancha EPS 25 kg/m³, e = 5 cm
8 Barrera de vapor: imprimación asfáltica + film 200 µ
9 Panel Pi pretensado h 0,50 (Astori): losa cortada, nervio en vista
10 Canaleta H°A in situ s/ VP, pend. 1 % a desagüe lateral
11 Media caña de mortero
12 Estribos salientes de la VP (Ø10) anclados al H° in situ
13 Neopreno 10 mm + pasador Ø16 en vaina c/ grout
14 Junta EPS 20 mm panel / H° in situ
15 Viga VP-70 pretensada doble T 0,40 x 0,70 (Astori)
16 Columna premoldeada H°A 0,40 x 0,40 (en vista)
17 Ménsula lateral: apoyo de la VP (en vista)
18 Ménsula interior: apoyo del recorte de losa (en vista)
19 Losa alveolar pretensada h 0,30 (ALV-30 Astori)
20 Capa de compresión H°A e = 5 cm + malla Ø6 c/15
21 Banda de neopreno continua 10 mm s/ VP
22 Panel sándwich premoldeado e = 0,20 (apoyado en la base)
23 Alma de EPS 6 cm + conectores de fibra de vidrio
24 Hoja interior portante H°A 8 cm / hoja ext. 6 cm
25 Riel de anclaje embutido (tipo Halfen) + bulón T M16
26 Fija panel: 2 ángulos L 100x100x10 galv. c/ ovalados
27 Bulón M16 pasante en vaina del alma + arandela y tuerca
28 Junta 20 mm: lana mineral cortafuego + sellador
29 Junta perimetral EPS 10 mm + sellador
30 Solado cerámico s/ adhesivo cementicio + zócalo
31 Carpeta niveladora MCI 1:3, e = 2 cm
32 Contrapiso liviano H° c/ EPS, e = 6 cm (acústico)
33 Cielorraso placa de yeso 12,5 mm s/ perfiles galv. 35 mm
34 Vela de cuelgue regulable fijada a la losa
35 Perfil perimetral (buña) de cielorraso
36 Solado cerámico s/ adhesivo cementicio
37 Carpeta hidrófuga MCI 1:3 + 10 % hidrófugo, e = 2 cm
38 Contrapiso H° armado e = 12 cm c/ malla Ø4,2 c/15
39 Film de polietileno 200 µ
40 Tosca compactada en capas de 15 cm
41 Junta de dilatación EPS 20 mm + sellador
42 Mortero de asiento + calces de neopreno
43 Pasador Ø16 panel / viga en vaina c/ grout
44 Viga portapanel premoldeada 0,25 x 0,60 (solo bajo paneles)
45 Neopreno de apoyo s/ pared del cáliz
46 Sellador PU s/ fondo de junta (junta horizontal ext.)
47 Pintura asfáltica en caras enterradas
48 Vereda H° peinado e = 8 cm, pend. 2 % hacia afuera
49 Contrapiso de tosca bajo vereda
50 Junta vereda / viga EPS 10 mm + sellador
51 Columna empotrada en el cáliz 0,70 (≥ 1,5 lado)
52 Cáliz H°A in situ c/ paredes dentadas (llaves de corte)
53 Relleno grout sin contracción (H-30)
54 Base aislada H°A in situ (dimensiones s/ cálculo)
55 Armadura de base Ø12 c/15 (s/ cálculo)
56 Hormigón de limpieza e = 5 cm
57 Terreno natural compactado
58 Mortero de nivelación bajo columna
59 Junta vertical entre paneles: fondo de junta + sellador PU
60 Junta EPS 20 mm viga portapanel / columna


NUDO 1 · CUBIERTA

Axonometría esc. 1:15 · corte entre columnas

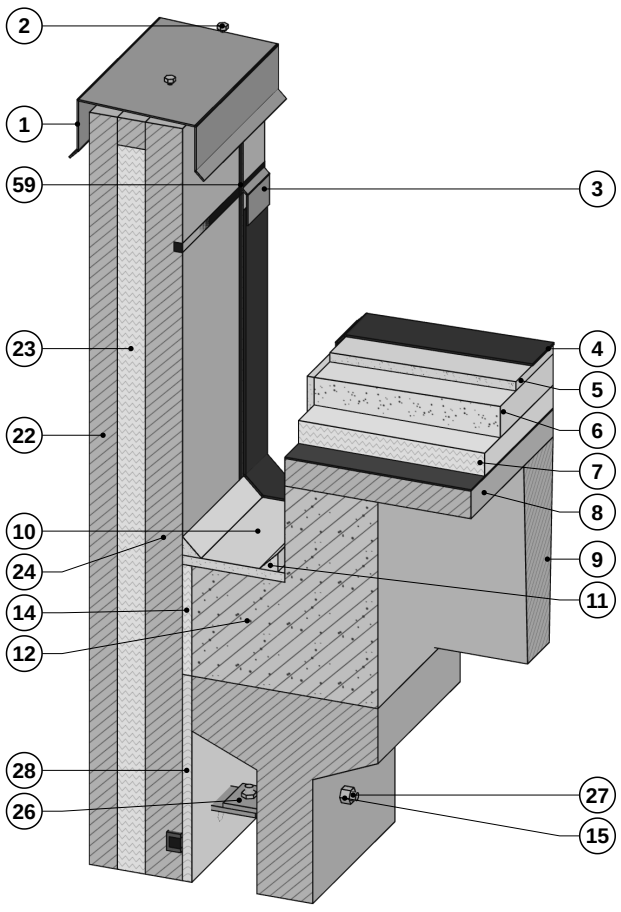


NUDO 2 · ENTREPISO

Axonometría esc. 1:15 · corte por eje de columna

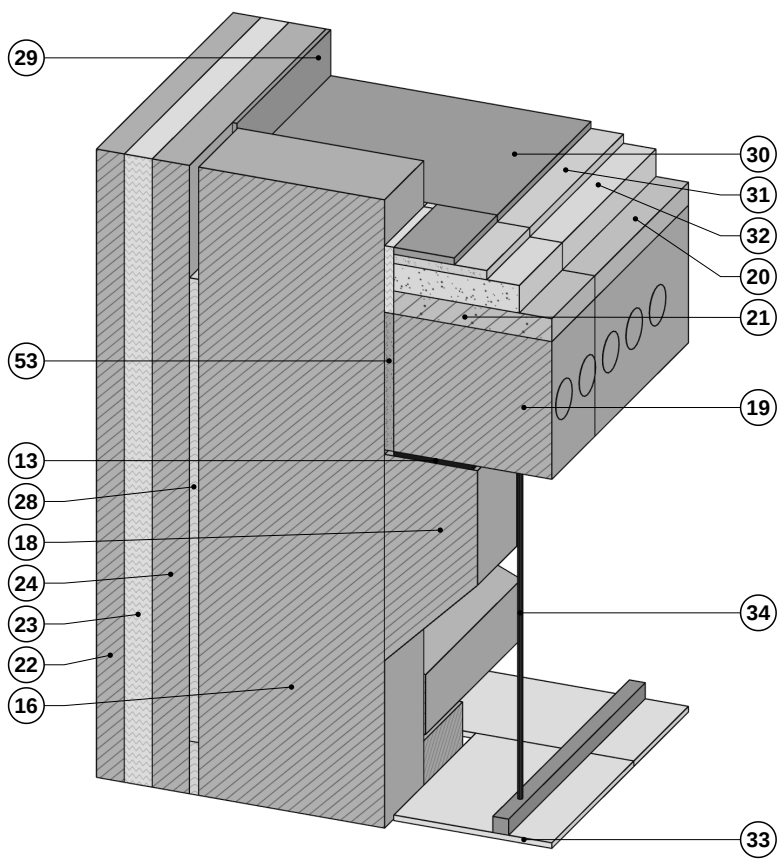


NUDO 3 · PISO S/ TERRENO

Axonometría esc. 1:15 · corte por eje de columna

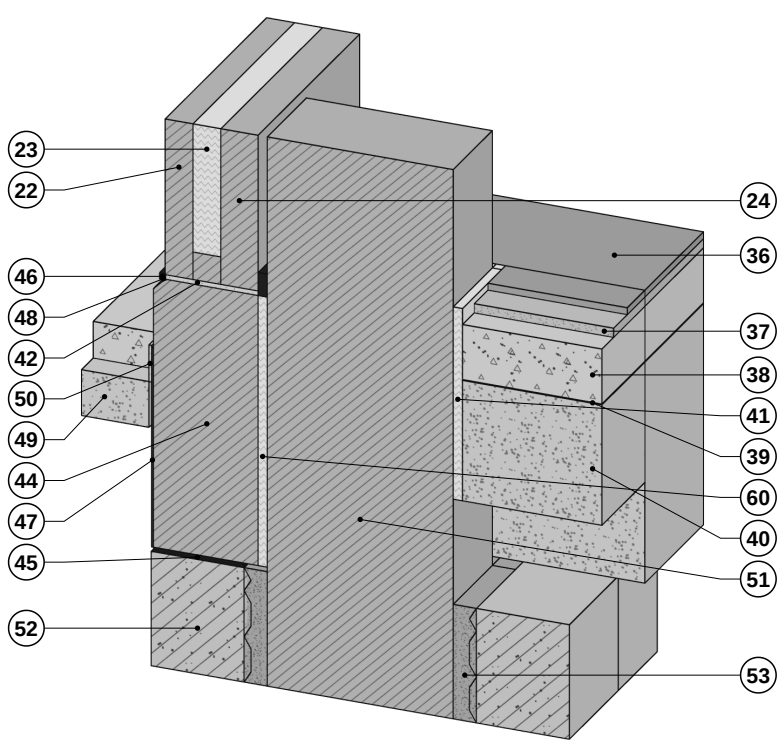

CONVENCIONES

- H°A premoldeado
- H°A in situ
- H° simple / contrapiso
- H° liviano c/ EPS
- Carpeta / mortero
- Carpeta hidrófuga
- Grout sin contracción
- EPS (aislación térmica)
- Lana mineral
- Tosca compactada
- Terreno natural
- Neopreno / sellador
- Acero galvanizado
- Elemento en vista

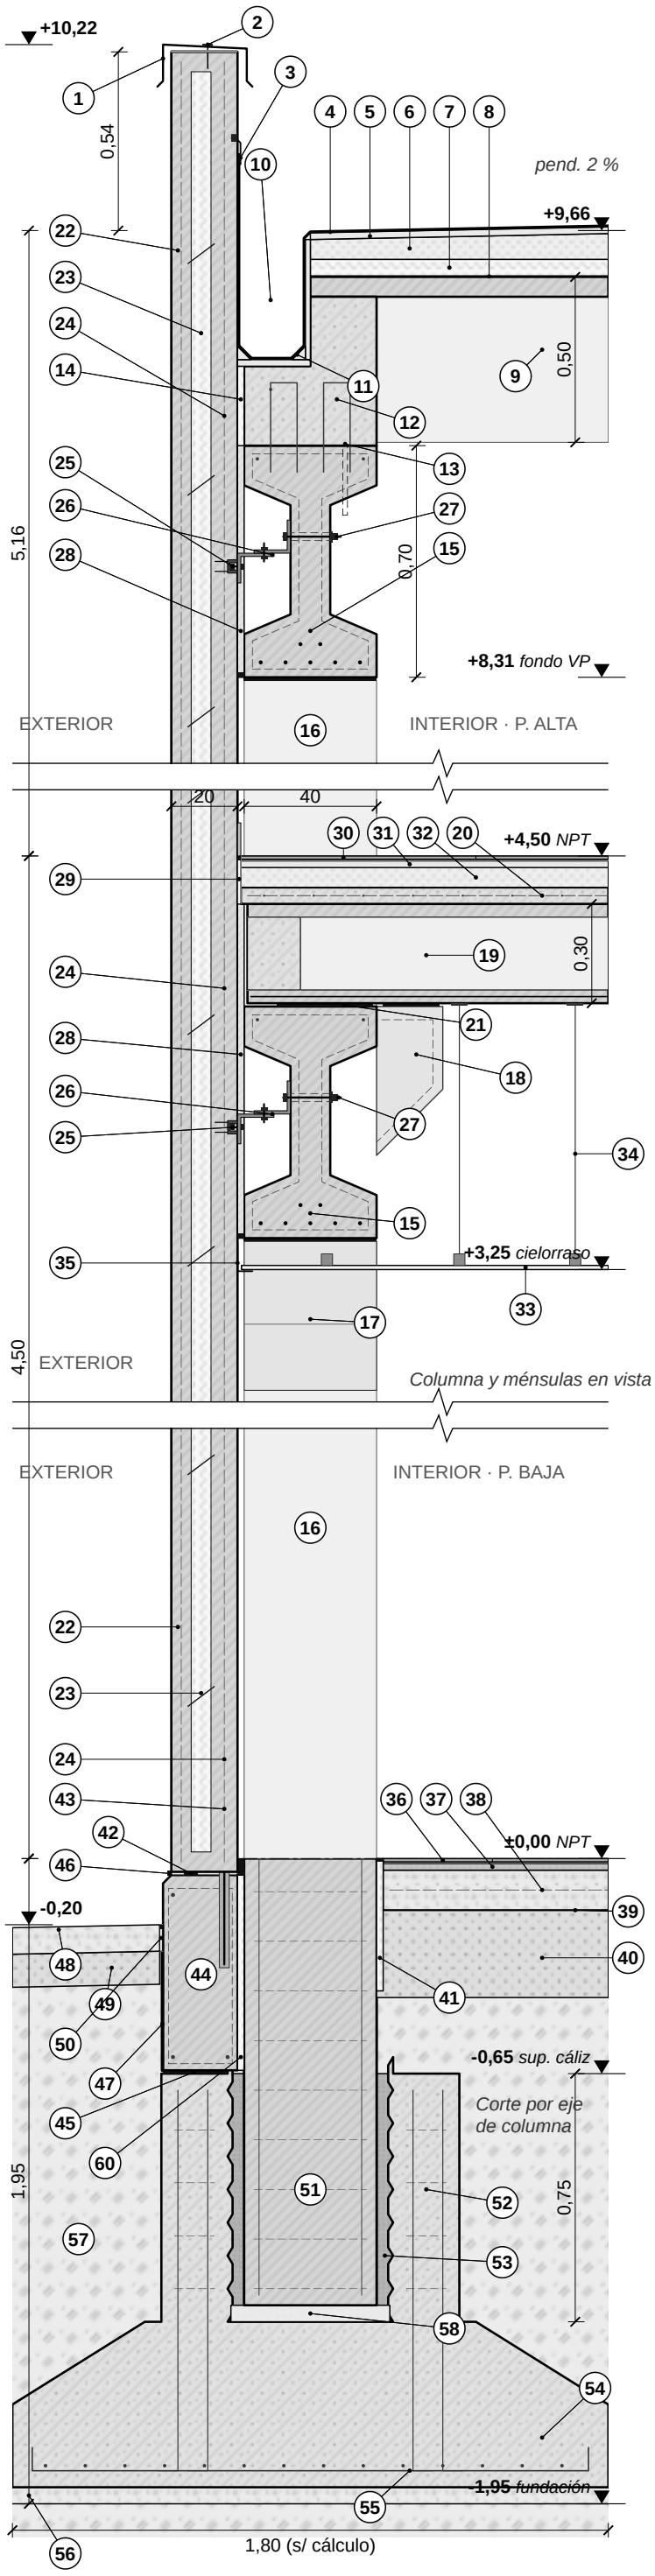

TP FINAL FECHA: 19/10/2026	DOCENTE: Arq. Tucci y Arq. Cardozo ALUMNA: Candelaria Vitale GRUPO: 13	NIVEL: OBS:	CONSTRUCCIONES II CATEDRA: ARQ. TUCCI