CERRAMIENTO VIDRIADO
DETALLE INTEGRAL 1:20

NUDO: CUBIERTA PLANA Y CERRAMIENTO PANEL SANDWICH


63. Soporte de Malla
62. Moldura tapa ALCOR
61. Cupertina de chapa galvanizada
60. Aislacion termica EPS para cierre superior
59. Tornillo autoperforante para fijaciones cupertina
58. Malla de reparticion
57. Losa de H°A° sobre encofrado perdido h: 0.11mts
56. Membrana asfaltica de aluminio
55. Carpeta niveladora
54. Mortero impermeable MCI e: 0.05mts
53. Contrapiso liviano EPS con pendiente e: 0.04mts
52. Barrera de vapor: pintura asfaltica


NUDO: ENTREPISO STEEL DECK Y CERRAMIENTO SISTEMA PANEL SANDWICH


51. Cerramiento integral en muro panel sandwich
50. Encuentro entre paneles con fijacion oculta y encastre
49. Tornillo autoperforante de union oculta entre Paneles y PGU
48. Lamina exterior de acero galvanizado
47. Aislacion termica: panel poliuretano(PUR) e: 80mm
46. Lamina interior de acero galvanizado
45. Tornillo de union perfil PGU—Columna metalica
44. Perfil PGU 100
43. Cuelgue de esctructura de cielorraso tecnico
42. Placa soldada a viga para fijacion de cielorraso tecnico
41. Perfil travesaño
40. Perfil larguero
39. Placa roca yeso para cielorraso tecnico e: 0.02m
38. Angulo "L" perimetral para cierre de cielorraso tecnico
37. Viga entrepiso secundaria HEB300(30x30cm) Luz: 6.00m
36. Placa colaborante Steel Deck ALCOR h: 0.11m
35. Capa de compresion H°A° e: 0.03m
34. Malla electrosoldada c/0.15m s/calculo
33. Contrapiso liviano EPS e: 0.04m
32. Carpeta MHR 1:1/4:3 e: 0.02m
31. Solado de terminacion: porcelanato 60x60cm e: 0.01m
30. Moldura frontera ALCOR de borde "L" galvanizada + sujetador de borde
29. Tuerca abulonada para vinculacion viga—columna
28. Perno conector de corte Steel Deck(placa colaborante)h: 0.13mts
27. Cartela angular vinculacion viga—columna
26. Viga metalica HEB400 (40X30cm) Luz: 6.00mts


NUDO: FUNDACION ZAPATA AISLADA DE H°A° Y CERRAMIENTO VERTICAL OPACO

25. Remate inferior de panel en fachada (Acero prelacado) e: 0.06cm
24. Contrapiso HRP 1:1/4:3:6 e: 0.08m
23. Carpeta niveladora MHR
22. Solado de terminacion: porcelanato 60x60cm e: 0.01m
21. Mortero de jjunta e: 0.01m
20. Adhesivo cementicio para porcelanato e: 0.01m
19. Carpeta niveladora e: 0.02m
18. Carpeta hidrofuga MCI e: 0.02m
17. Contrapiso de H° pobre de cascote e: 0.08m
16. Film de polietileno 200u.
15. Columna metalica HEB 400 s/corte.
14. Cartelas metalicas soldadas.
13. Doble tuerca roscada y contra tuerca con arandela
12. Placa de anclaje de base columna metalica e: 0.012m
11. Perno roscado de anclaje
10. Mortero fluido para anclajes tipo "Grout" e: 0.03m
09. Cabezal H°A° h: 0.80m
08. Perchas ø10 s/calculo
07. Estribos ø10 s/calculo
06. Armadura principal de cabezal.
05. Tronco de base H°A° IN SITU
04. As de tronco de base
03. H° de limpieza e: 0.05m
02. As inferior de la base
01. Suelo tosca compactada

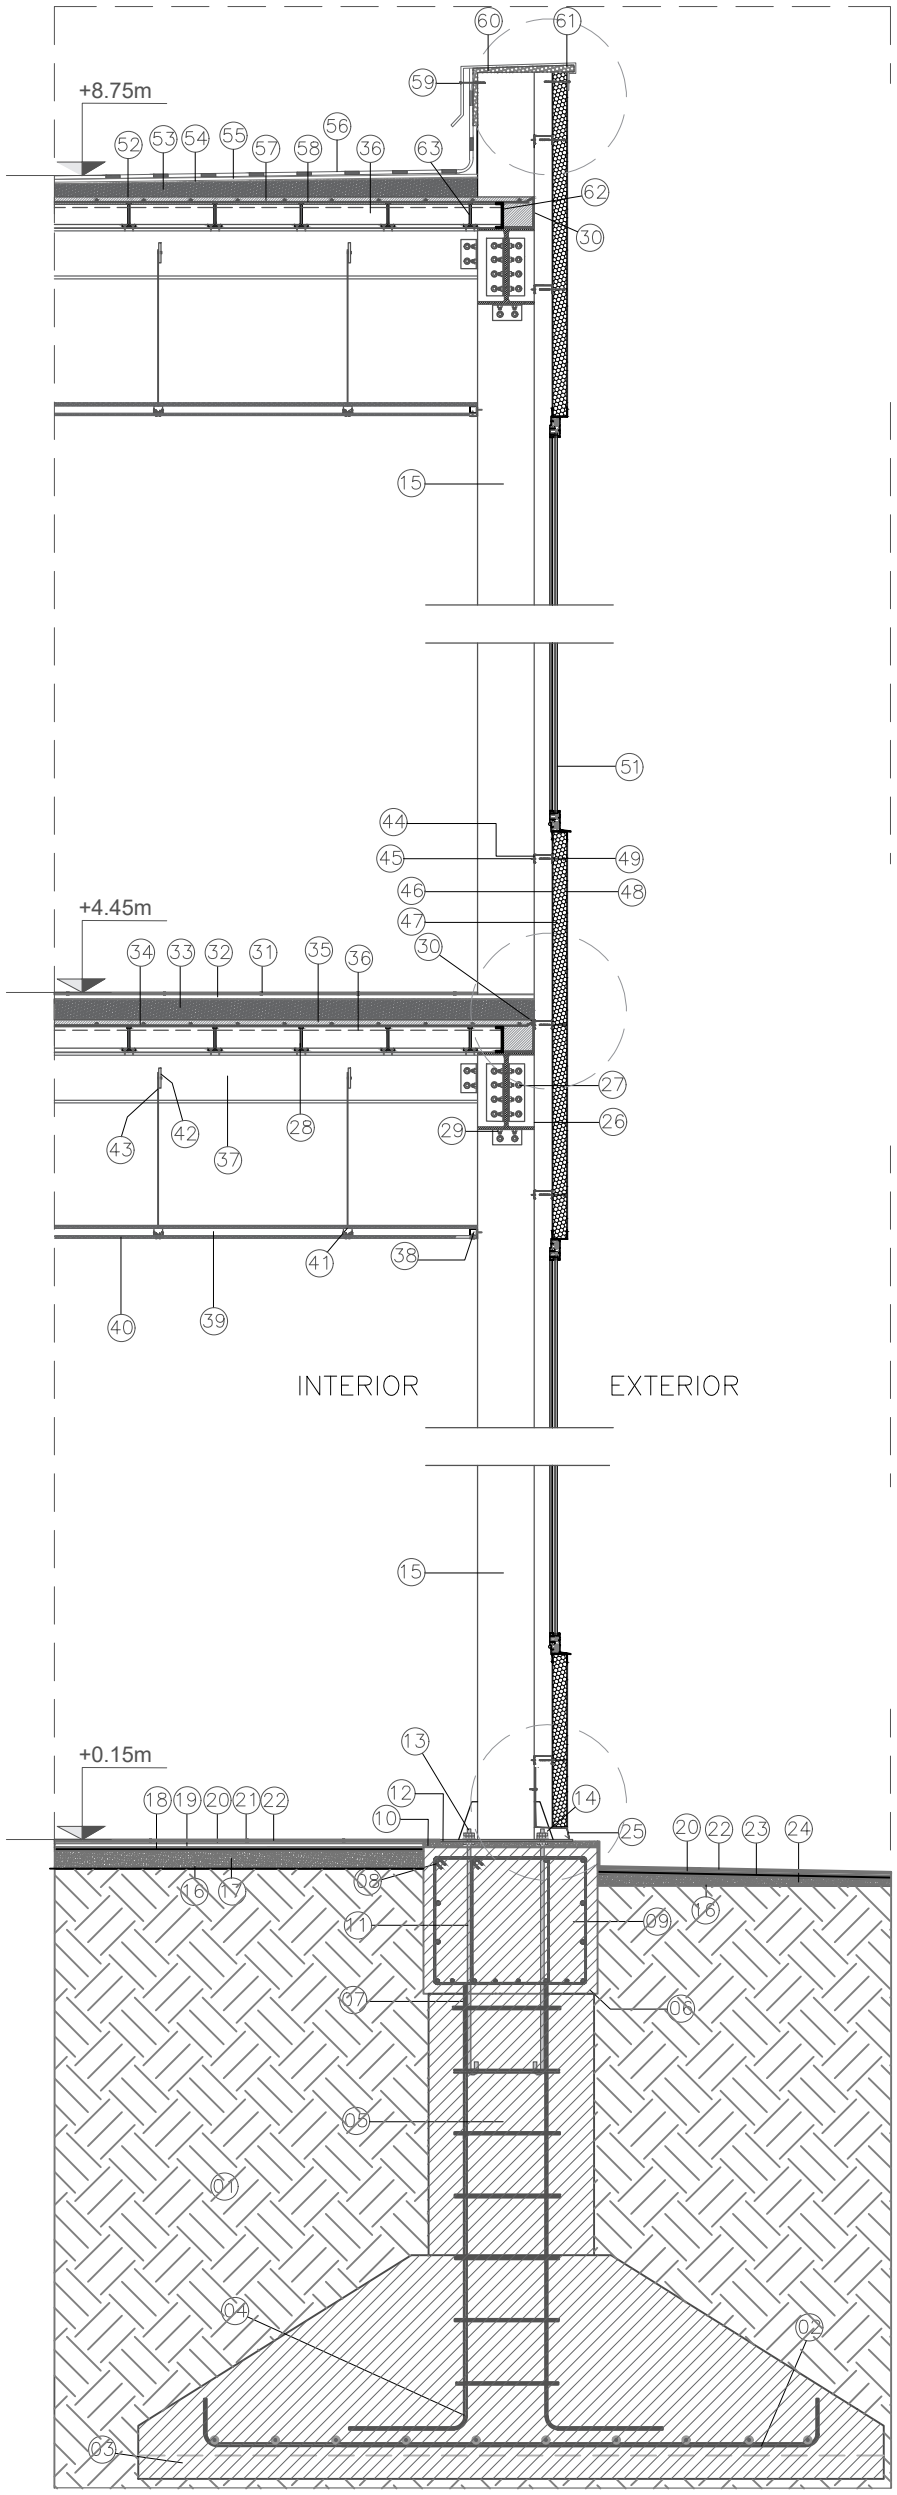

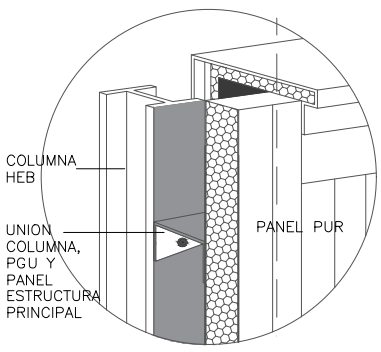

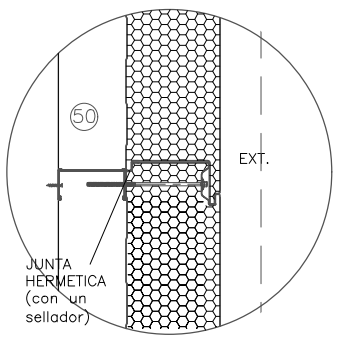

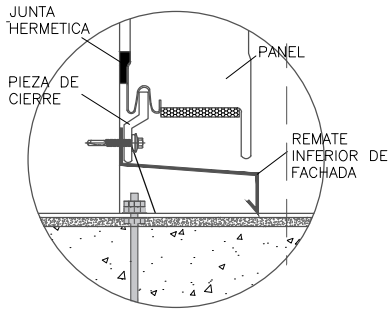

TP N°6 FECHA:19/10/26	DOCENTE: Arq. Tucci y Arq. Cardozo ALUMNOS: Gómez Karen GRUPO: 13	NIVEL: OBS:	CONSTRUCCIONES II CATEDRA: ARQ. TUCCI