
CORTE INTEGRAL — FACHADA VIDRIADA · HORMIGÓN PREMOLDEADO

ESC. 1:20

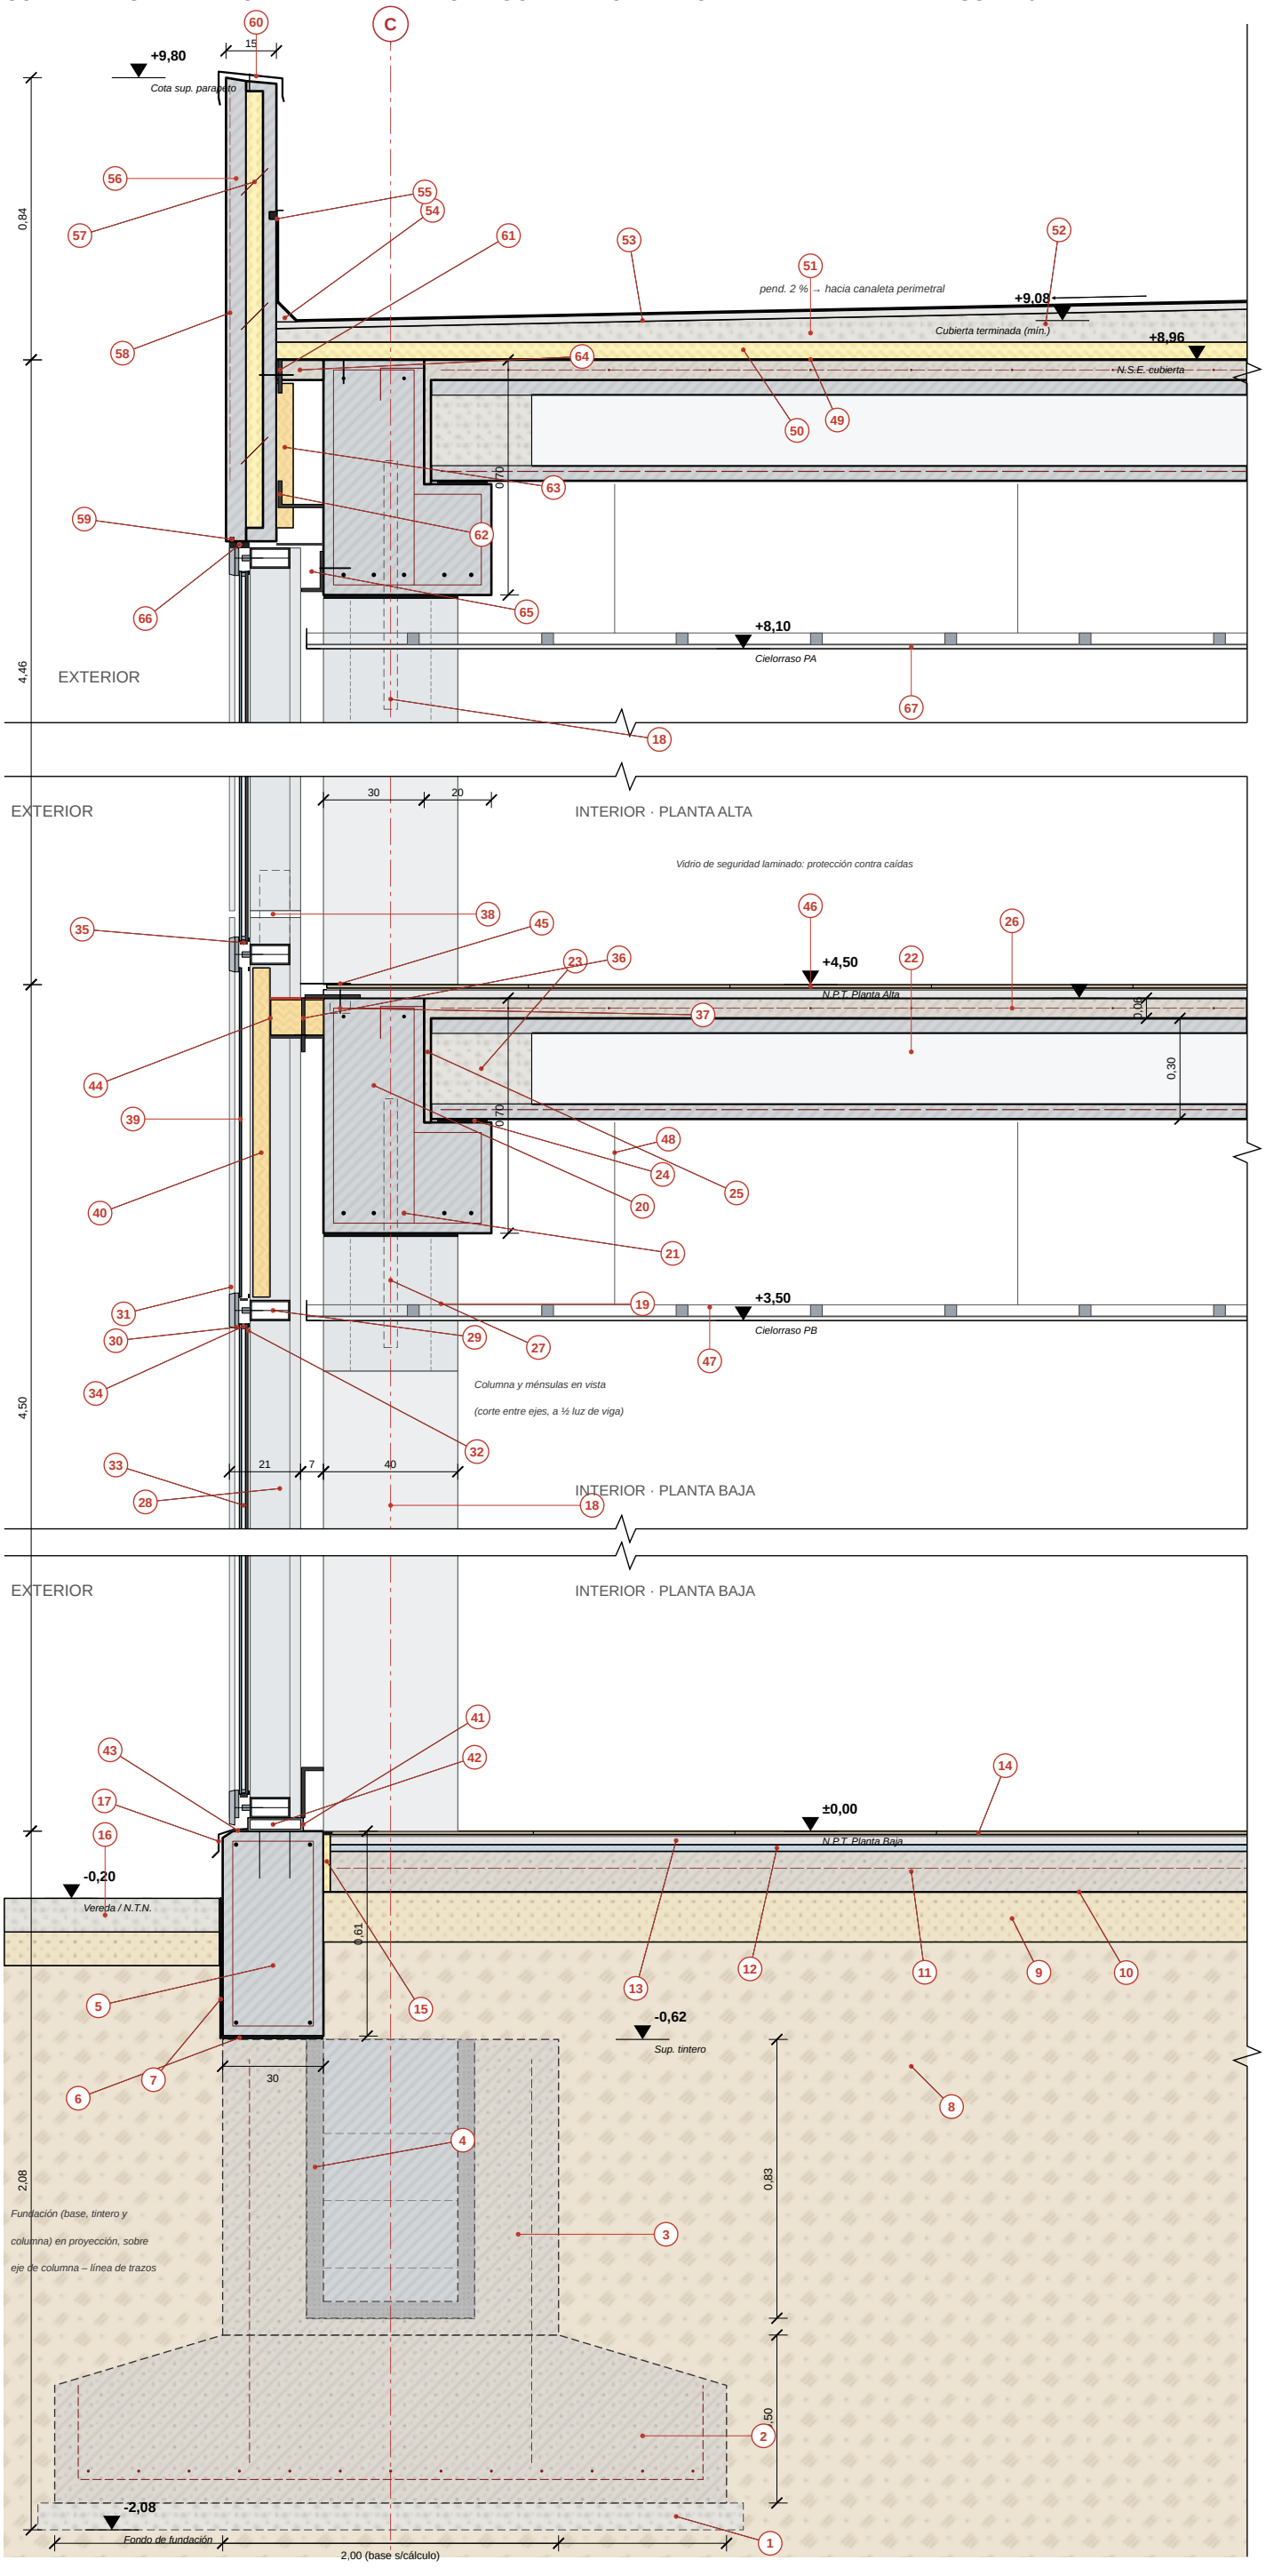

0 10 20 30 40 50 cm

ESC. 1:20

REFERENCIAS

FUNDACIÓN Y PISO SOBRE TERRENO

1 Hormigón de limpieza H-8, e = 8 cm.
2 Base aislada H°A° in situ H-25 (dim. y armadura s/ cálculo y estudio de suelos).
3 Tintero / cáliz H°A° in situ, empotramiento de columna ≥ 1,5 b (83 cm).
4 Columna empotrada c/ llaves de corte + grout cementicio sin retracción (5 cm).
5 Viga de fundación premoldeada H°A° 30x61 (VF) apoyada en tinteros.
6 Apoyo de neopreno e = 10 mm, VF / tintero.
7 Aislación hidrófuga vertical: pintura asfáltica 2 manos + film 200 µ.
8 Suelo natural compactado.
9 Tosca compactada e = 15 cm (95 % Proctor).
10 Film de polietileno 200 µ, solapes 20 cm (barrera de humedad).
11 Contrapiso H°A° e = 12 cm c/ malla Q188.
12 Carpeta hidrófuga 1:3 + 10 % hidrófugo, e = 2 cm.
13 Carpeta de nivelación 1:3, e = 2,5 cm.
14 Porcelanato 60x60 s/ adhesivo cementicio impermeable.
15 Junta perimetral EPS 20 mm + sellador poliuretánico.
16 Vereda H° peinado e = 10 cm s/ tosca + junta c/ sellador.
17 Babeta chapa galv. N°24 plegada c/ goterón.

ESTRUCTURA PREMOLDEADA (GRANDES LUCES)

18 Columna premoldeada H°A° 40x40 H-30 c/ ménsulas (en vista).
19 Ménsula corta de columna 40x40 (en vista).
20 Viga portante premoldeada pretensada tipo “L” 30/70 c/ talón 20x33, H-40.
21 Cordones de pretensado Ø 12,7 mm + estribos / armadura pasiva.
22 Losa alveolar pretensada e = 30 cm (luces hasta 14 m), corte por alvéolo.
23 Tapón de H° en alvéolos de apoyo (30 cm).
24 Apoyo de neopreno continuo 10 mm, losa / talón de viga.
25 Junta viga–losa llenada c/ H° in situ (llave de corte).
26 Capa de compresión H°A° in situ H-25 e = 6 cm c/ malla Q188 (diafragma).
27 Bulón Ø 20 ménsula–viga en vaina grouteada + neopreno (en vista).

MURO CORTINA – SISTEMA STICK, MÓDULO 1,25 m

28 Montante aluminio 50x150 anodizado (en vista).
29 Travesaño aluminio 50x120 (corte).
30 Presor de aluminio + tornillo inox c/ 25 cm.
31 Tapa exterior clipada (cubre-presor).
32 Burletes EPDM interior y exterior.
33 DVH: 6 templado + 12 cámara + 3+3 laminado PVB.
34 Separador alum. c/ desecante + butilo + silicona estructural.
35 Calzos de apoyo de EPDM (2 por paño).
36 Grapa de anclaje acero galv. regulable 3D, agujeros colisos + bulón M12 inox.
37 Riel de anclaje (tipo Halfen) embutido en viga + bulón T.
38 Junta de dilatación de montante 20 mm c/ manguito interior.
39 Spandrel: vidrio templado 6 mm esmaltado + cámara ventilada.
40 Lana mineral 50 mm + bandeja de chapa galv. (back-pan).
41 Grapa inferior a VF (anclaje mecánico).
42 Perfil de arranque alum. c/ drenaje + tarugos a VF.
43 Sellador de silicona neutra s/ fondo de junta.
44 Barrera cortafuego: lana mineral 100 kg/m³ comprimida s/ chapa galv.
45 Cubrejunta perfil aluminio + sellador intumescente.
46 Carpeta 2,5 cm + adhesivo + porcelanato (piso PA).
47 Cielorraso suspendido placa de roca de yeso 12,5 mm junta tomada s/ perfilería galv.
48 Vela rígida a losa (perfil galv.).

CUBIERTA Y PARAPETO

49 Barrera de vapor: imprimación asfáltica + film 200 µ.
50 Aislación térmica EPS 30 kg/m³ e = 5 cm.
51 H° de pendiente alivianado, mín. 4 cm, pend. 2 %.
52 Carpeta cementicia 1:3 e = 2 cm.
53 Membrana asfáltica 4 mm c/ geotextil + pintura reflectiva.
54 Media caña de mortero (encuentro con parapeto).
55 Babeta: membrana en buña + perfil chapa + sellador.
56 Panel sándwich premoldeado (cenefa/parapeto): H°A° 6 + EPS 5 + H°A° 4 cm.
57 Conectores de acero inox entre capas del panel.
58 Malla electrosoldada del panel.
59 Goterón (buña 12x12).
60 Cupertina chapa galv. N°22 c/ goterones, tornillo + sellador.
61 Unión mecánica panel–viga: perfil L 100x10 galv. + inserto roscado + anclaje químico M16.
62 Perfil L de restricción inferior del panel.
63 Lana mineral 50 mm en cámara panel–viga.
64 H° de relleno in situ s/ chapa galv. (cierre de cámara).
65 Grapa superior de montante a viga (anclaje químico).
66 Sellador + fondo de junta: travesaño sup. / panel.
67 Cielorraso suspendido PA (ídem 47) – plenos de instalaciones.

CONVENCIONES

- H°A° premoldeado
- H°A° in situ
- H° simple / pendiente
- Mortero / carpeta
- Grout s/ retracción
- Suelo natural
- Tosca compactada
- EPS
- Lana mineral
- Vidrio
- Aluminio
- Acero galv. / neopreno
- Proyección / oculto
- Eje de columna

NOTAS DEL SISTEMA

Sistema: columnas premoldeadas empotradas en tinteros + vigas “L” pretensadas s/ ménsulas + losas alveolares pretensadas (luces 10–14 m). Uniones mecánicas (bulones, perfiles, insertos) y húmedas (grout / H° in situ: capa de compresión). Corte entre ejes de columnas (a ½ luz de viga); columna y ménsulas en vista. Muro cortina stick: montantes colgados de cada entrepiso (grapa superior fija, inferior deslizante) c/ junta de dilatación 20 mm para absorber deformaciones. Tolerancias de montaje premoldeado ±10 mm, absorbidas por grapas regulables 3D. Juntas de fachada c/ fondo de junta + sellador; drenaje y ventilación de travesaños. Barrera cortafuego continua en cada borde de losa (sectorización por piso). Cotas en m (niveles) y cm (detalles). Verificar todo s/ cálculo estructural.

LÁMINA 2 · CORTE INTEGRAL

Sistema de hormigón premoldeado de grandes luces
Cerramiento vidriado – muro cortina (sistema stick)

MATERIA	Construcciones II
CÁTEDRA	Arq. _____
ALUMNO/A	_____
GRUPO	_____
ESCALA	1:20 (impresión al 100 % en A3)
HOJA	1 de 4 · A3 · 2026