
CORTE INTEGRAL
CERRAMIENTO OPACO

ESCALA 1:20


REFERENCIAS

1 Cupertina chapa galv. N°22 c/ goterones
2 Tornillo c/ arandela de neopreno + sellador
3 Membrana asfáltica 4 mm c/ aluminio
4 Carpeta 1:3 c/ 10 % hidrófugo, e = 2 cm
5 Contrapiso liviano H° c/ EPS (aislante), pend. 2 %
6 Babeta chapa galv. + sellador en buña del panel
7 Barrera de vapor: imprimación + film 200 µ
8 Junta EPS 2 cm panel / canaleta + sellador
9 Canaleta H°A in situ c/ hueco semicircular, pend. 1 %
10 Capa de compresión 5 cm c/ malla Ø6 c/15
11 Estribos salientes Ø10 (anclan canaleta y capa)
12 Panel TT h 0,65: ala y nervios cortados
13 Viga de borde premold. s/ VL (L en entrepiso)
14 Viga VL doble T 40x70 pretensada
15 Columna pretensada 40x40 (en vista)
16 Ménsula de columna c/ diagonal (en vista)
17 Neopreno + perno Ø20 (VL / ménsula)
18 Barras de vinculación VL / L en mortero
19 Ala del TT s/ viga de borde + neopreno
20 Solado cerámico s/ adhesivo cementicio
21 Carpeta niveladora MHR 1:1/4:3, e = 2 cm
22 Cielorraso placa de roca de yeso 12,5 mm
23 Montantes y soleras chapa galv. 35 mm
24 Gancho / vela a los nervios del panel TT
25 Panel sándwich premoldeado H°A, e = 20 cm
26 Hoja ext. H°A 6 cm / hoja int. portante 8 cm
27 Alma EPS 6 cm + conectores de fibra de vidrio
28 Rehundido Ø100 prof. 3 cm tapado c/ mortero
29 Bulón pasante M20: atraviesa panel y ala de VL
30 Agujero ovalado 40x60 + vaina, tuerca y arandela
31 Junta 2 cm: lana mineral cortafuego + sellador
32 Junta perimetral EPS 1 cm + zócalo
33 Junta vertical panel / panel: fondo + sellador PU
34 Sellador PU s/ fondo de junta (junta horizontal)
35 Solado cerámico s/ adhesivo cementicio
36 Carpeta niveladora MHR 1:1/4:3
37 Carpeta hidrófuga MCI 1:3
38 Contrapiso de H° pobre, e = 12 cm
39 Film de polietileno 200 µ
40 Tosca compactada, e = 15 cm
41 Junta de dilatación EPS 2 cm + sellador
42 Viga portapanel premoldeada 22x45 (s/ cuellos)
43 Mortero de asiento + pasador Ø16 en vaina c/ grout
44 Pintura asfáltica en caras enterradas
45 Vereda de H° peinado s/ tosca
46 Tronco de columna dentro del cuello
47 Anclaje mecánico húmedo (horquillas)
48 Relleno de H° cementicio cuello/columna
49 Armadura de vinculación fundación–columna
50 Cuello de la base, H°A° in situ
51 Base de H°A° colada in situ (s/ cálculo)
52 Armadura de fundación s/ cálculo
53 H° de limpieza, e = 10 cm
54 Terreno natural
55 Neopreno de apoyo viga portapanel / cuello
56 Junta vereda / viga EPS 1 cm + sellador


NUDO 1 · CUBIERTA
Isométrica esc. 1:17,5

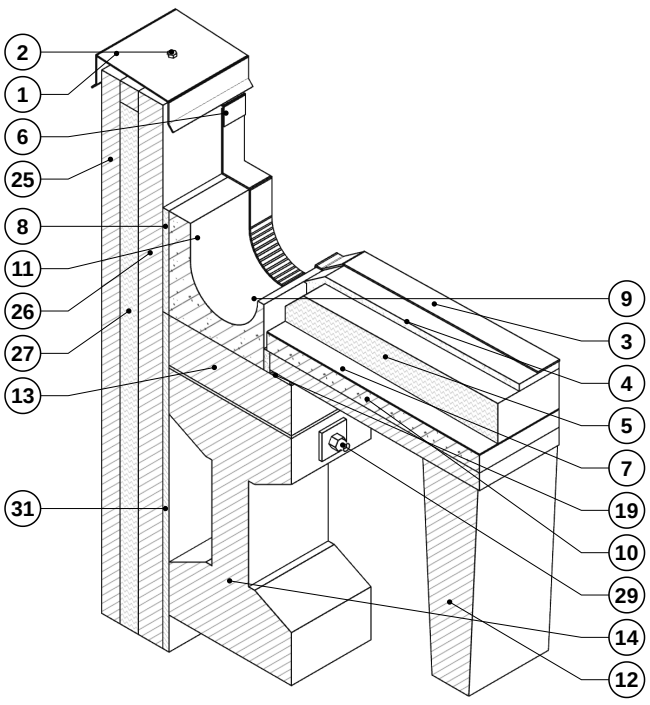


NUDO 2 · ENTREPISO
Isométrica esc. 1:20

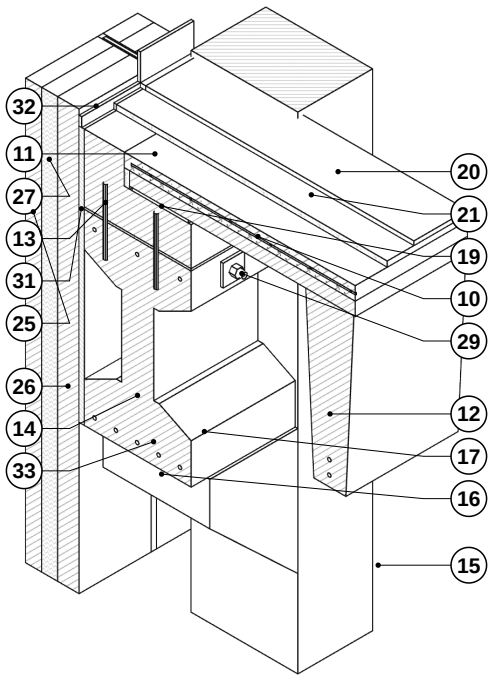

NUDO 3 · PISO
Isométrica esc. 1:15

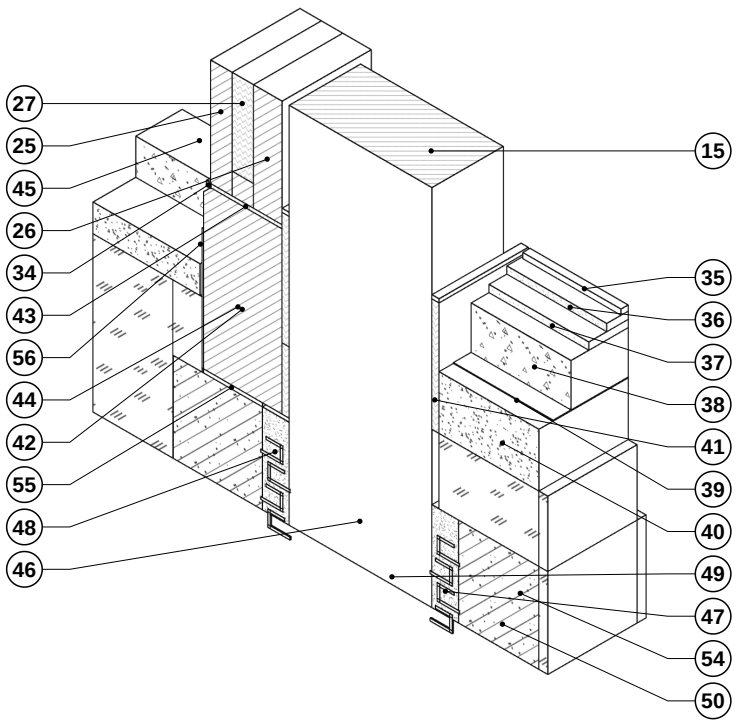

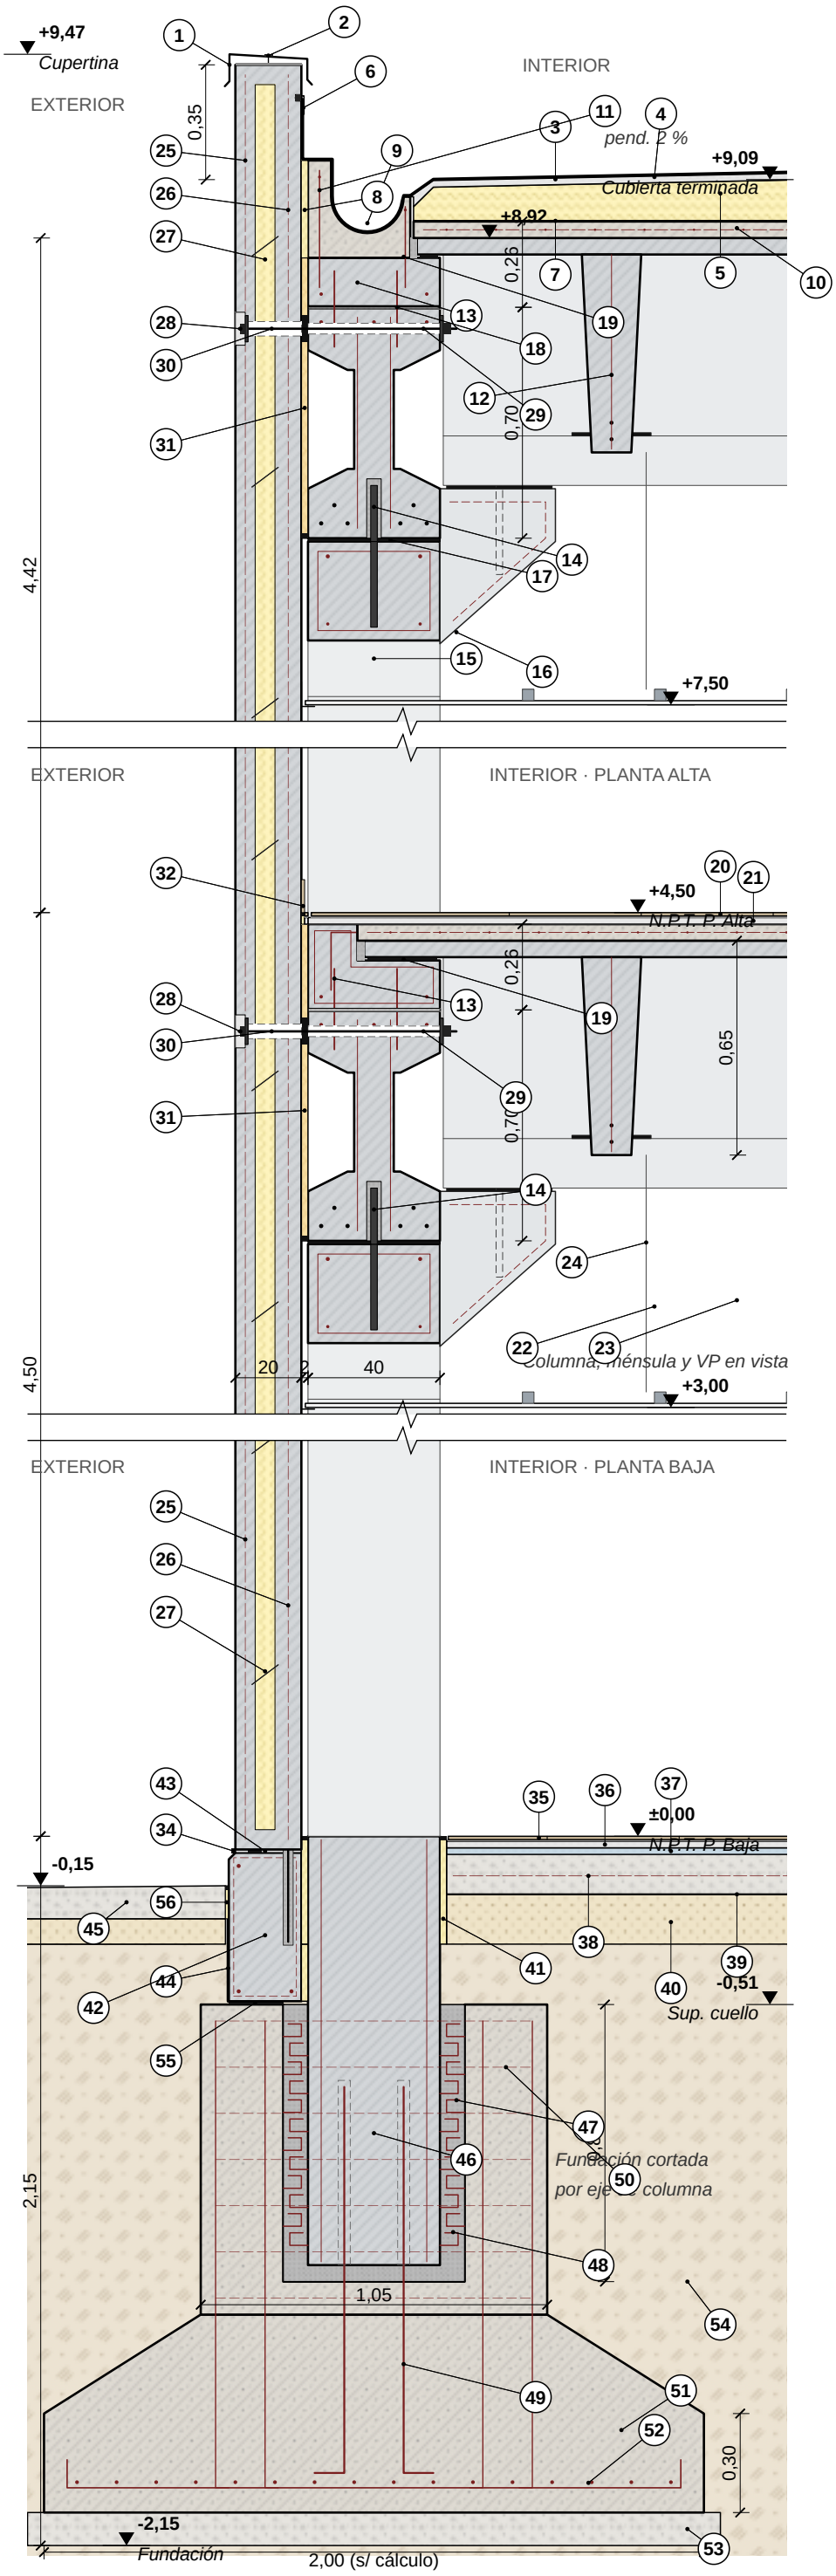

TP FINAL FECHA: 19/10/2026	DOCENTE: Arq. Tucci y Arq. Cardozo ALUMNA: Candelaria Vitale GRUPO: 13	NIVEL: OBS:	CONSTRUCCIONES II CATEDRA: ARQ. TUCCI