CORTE INTEGRAL ACERO
FRENTE INTEGRAL

Corte integral ESC. 1:20 · Detalles axonométricos ESC. 1:10

m · esc. 1:20 — 0 — 0,25 — 0,5 — 0,75 — 1


m · esc. 1:10 — 0 — 0,1 — 0,2 — 0,3 — 0,4 — 0,5

REFERENCIAS

1 Cupertina chapa galv. N°22 c/ goterones
2 Membrana asfáltica 4 mm c/ alum. + babeta
3 Carpeta de nivelación MHR 1:3, e = 2 cm
4 Contrapiso H° liviano, pend. 2 %
5 Barrera de vapor: film polietileno 200 µ
6 Capa de compresión H°A° s/ malla electrosold.
7 Separador de H° p/ malla electrosoldada
8 Conectores de corte (pernos) s/ viga IPN
9 Panel sándwich PUR 40 mm (termopanel)
10 Perfil L galv. borde de paquete de cubierta
11 Est. secundaria: omega + perfil Z inferior
12 Chapa plegada galv. C 75x80 e=2: anclaje panel
13 Montante parapeto tubo 100x100x3,2 soldado
14 Viga perimetral IPN 200, unión sold. + bulones
15 Viga IPN 180 (vista): chapa sold. + bulones
16 Columna HEB 200 (en vista)
17 Placa colaborante galv. (tipo Galvadeck)
18 Zinguería de borde fijada a la chapa
19 Platabanda 350x350x25 soldada + cartelas
20 Tuerca de nivelación / tuerca / contratuerca
21 Pernos de anclaje Ø20 en "J"
22 Grout de nivelación sin contracción, 25 mm
23 Dado estructural H°A° p/ columna y F. integral
24 Zapata de H°A°, armadura según cálculo
25 H° de limpieza, e = 5 cm
26 Travesaño: tapa int. MT-0817 / ext. MT-0819
27 Columna F.I.: MT-0817 / MT-0819 (en vista)
28 Doble vidrio hermético 6 + 12 + 6
29 Tubo 80x50x2 soldado a viga: anclaje F.I.
30 Grapa doble planchuela galv. + bulones M10
31 Sellador de junta + banda de neopreno
32 Zinguería a medida p/ cerramiento y buña
33 Zinguería a medida alféizar c/ pendiente
34 Aislación térmica: placa EPS 40 mm
35 Perfil U de arranque fijado al dado c/ brocas
36 Panel ciego PUR 40 mm en el frente integral
37 Baranda posapié acero inox. Ø42
38 Planchuela base + brocas Ø10 a losa
39 Solado s/ adhesivo cementicio
40 Carpeta hidrófuga MCI + 10 % hidrófugo
41 Contrapiso H° pobre e=12 cm (relleno)
42 Separador de suelo: film polietileno 200 µ
43 Suelo compactado
44 Cielorraso placa roca de yeso e = 9,5 mm
45 Vela rígida a losa: montante 35 + ángulo
46 Perfil Z buña en cielorraso independiente
47 Perfil C c/ banda neopreno colgado de viga
48 Vereda de H° peinado
49 Aislación hidrófuga vertical del dado


D1 · CUBIERTA / FRENTE INTEGRAL

Axonometría ESC. 1:10 · módulo entre columnas

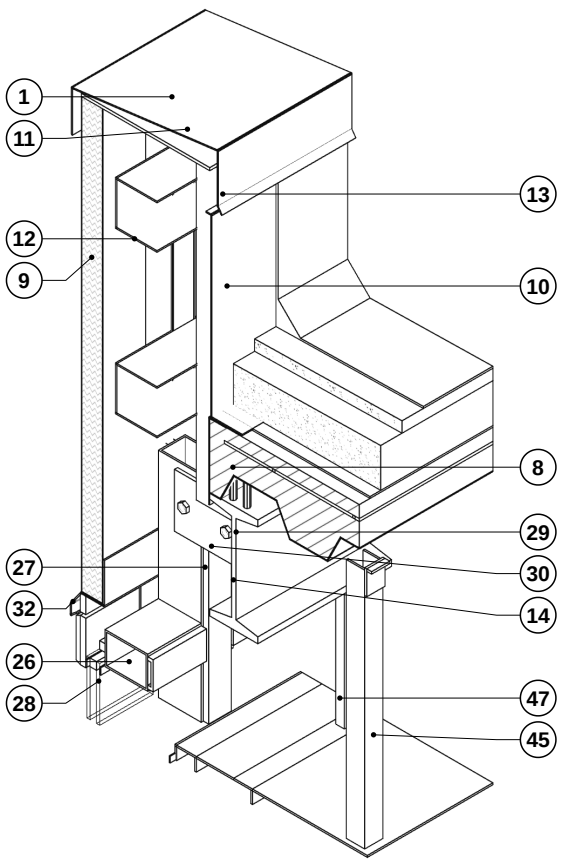


D2 · ENTREPISO / FRENTE INTEGRAL


Axonometría ESC. 1:10 · módulo entre columnas

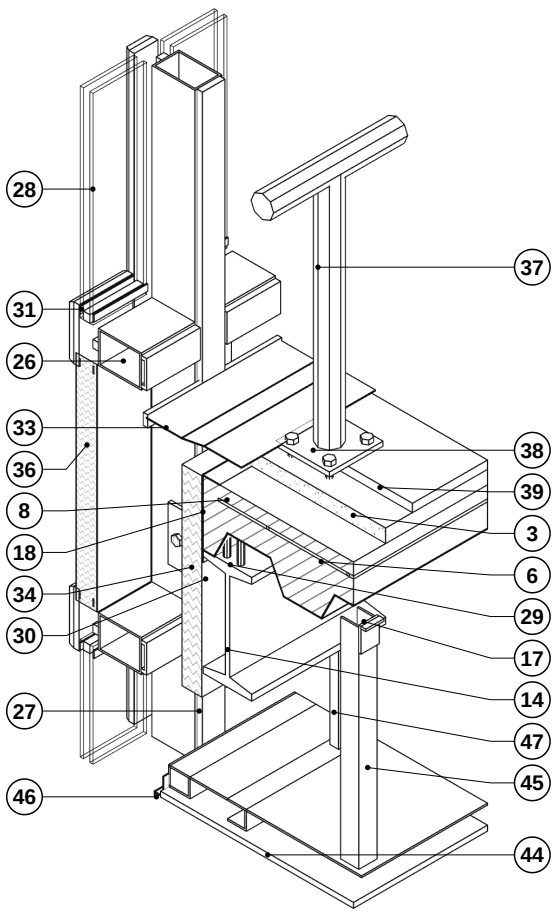


D3 · ARRANQUE / DADO ESTRUCTURAL

Axonometría ESC. 1:10 · eje de columna (corte por línea de pernos)

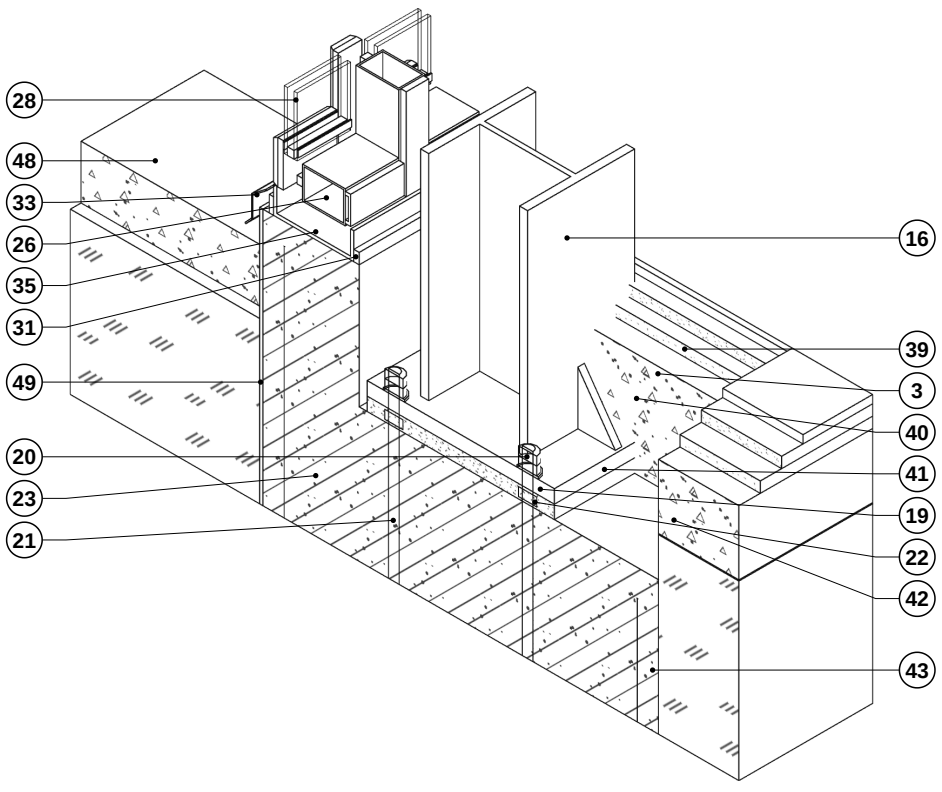

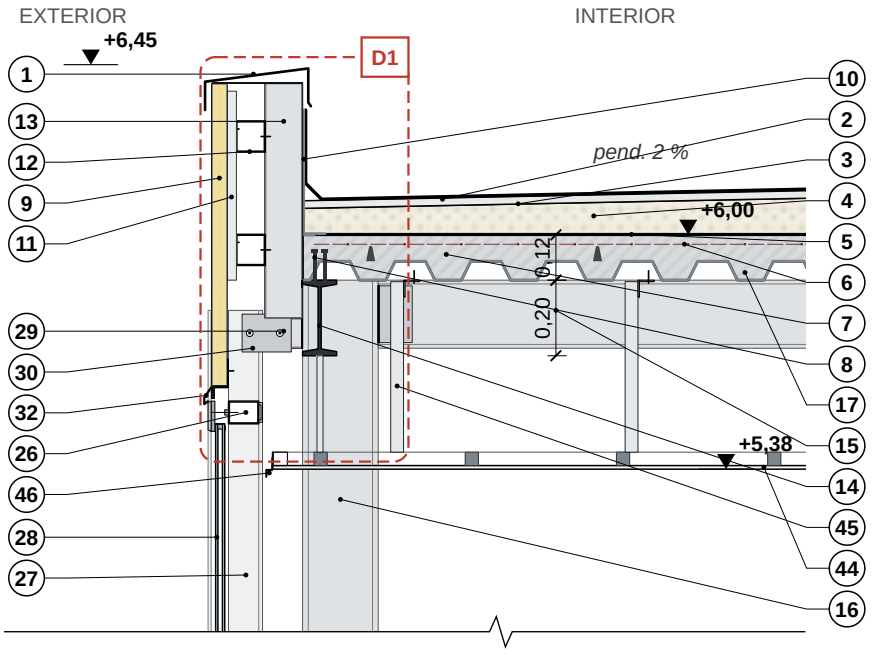

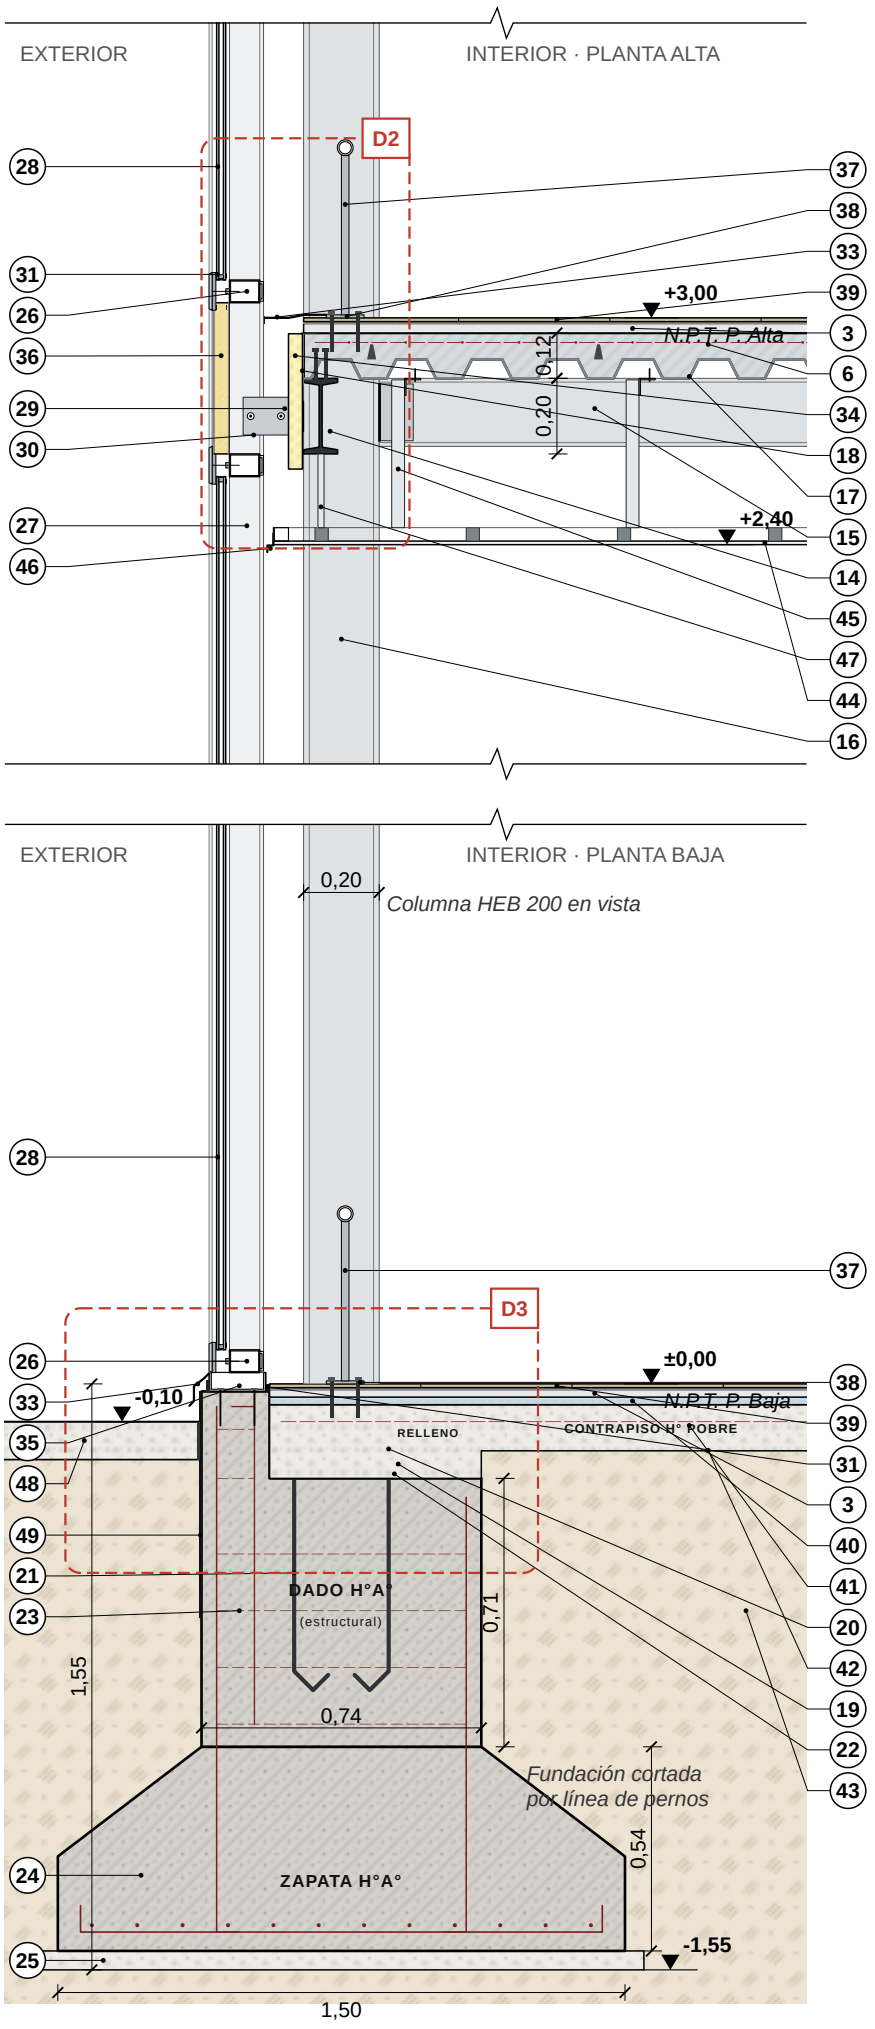

TP N°6 FECHA: 29/10/2026 LÁMINA: A3	DOCENTE: Arq. Tucci y Arq. Cardozo **ALUMNA: Candelaria Vitale** GRUPO: 13	NIVEL: OBS: corte integral esc. 1:20 / detalles esc. 1:10	CONSTRUCCIONES II CATEDRA: ARQ. TUCCI