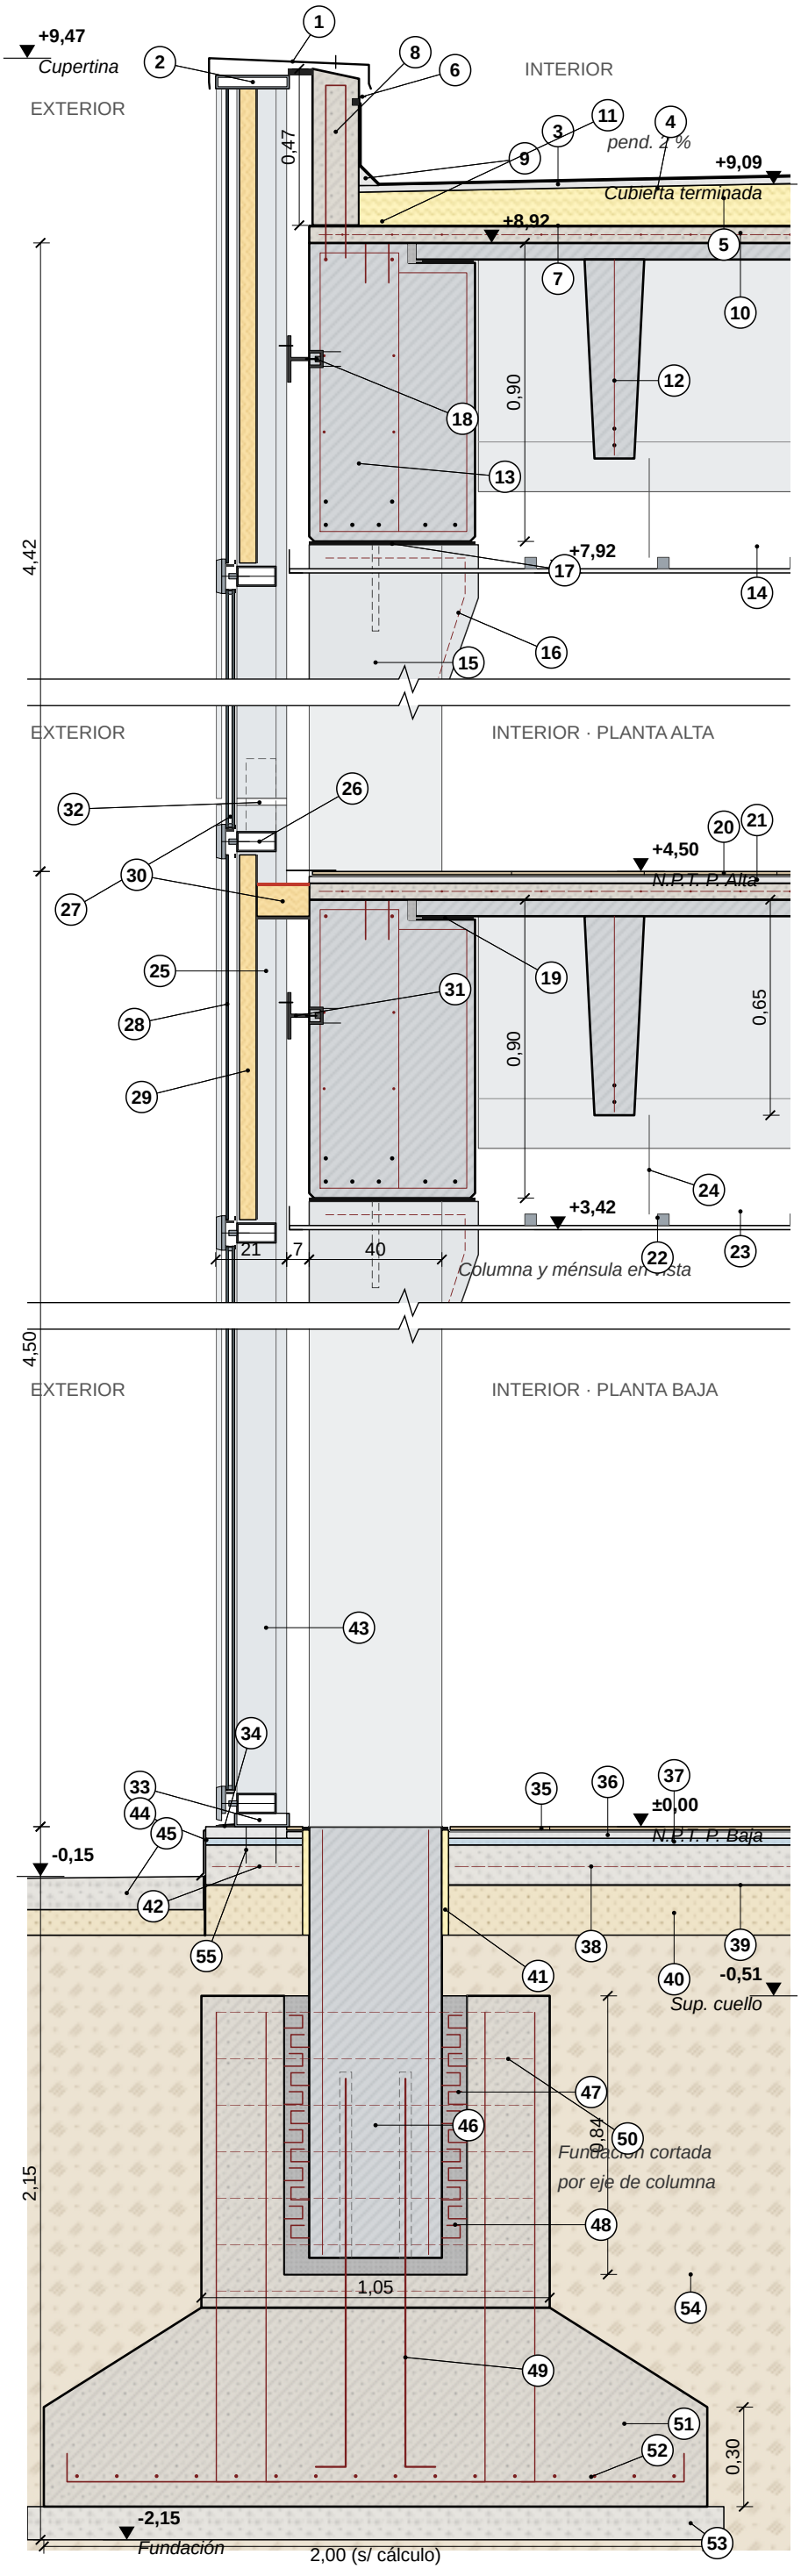


CORTE INTEGRAL — ESC. 1:20

0 50 cm

REFERENCIAS (corte integral y nudos)

CUBIERTA

1 Cupertina chapa galv. N°22 c/ goterones
2 Perfil de cierre sup. muro cortina + sellador
3 Membrana asfáltica 4 mm c/ aluminio + babeta
4 Carpeta 1:3 c/ 10 % hidrófugo, e = 2 cm
5 Contrapiso liviano H° c/ EPS (aislante), pend. 2 %
6 Babeta chapa galv. + sellador en buña
7 Barrera de vapor: imprimación + film 200 µ
8 Zócalo sup. H°A° in situ c/ barras a viga L
9 Media caña de mortero

ESTRUCTURA PREMOLDEADA (SISTEMA PI)

10 Capa de compresión 5 cm c/ malla Ø6 c/15
11 Estribos salientes de la viga L (2Ø10)
12 Panel TT h 0,65: ala y nervios cortados
13 Viga L de borde (recibe el panel TT)
14 Viga VP pretensada (en vista)
15 Columna pretensada 40x40 (en vista)
16 Ménsula de columna c/ diagonal (en vista)
17 Banda de neopreno + perno Ø20
18 Riel de anclaje embutido + bulón T
19 Ala del TT s/ ala viga L + neopreno

ENTREPISO Y CIELORRASOS

20 Solado cerámico s/ adhesivo cementicio
21 Carpeta niveladora MHR 1:1/4:3, e = 2 cm
22 Cielorraso placa de roca de yeso 12,5 mm
23 Montantes y soleras chapa galv. 35 mm
24 Gancho / vela a los nervios del panel TT


MURO CORTINA (STICK, MÓDULO 1,25 m)

25 Mullion: montante alum. 50x150
26 Travesaño + presor + tapa + burletes EPDM
27 DVH 6 templado + 12 + 3+3 laminado PVB
28 Spandrel: vidrio templado 6 mm esmaltado
29 Lana mineral 50 mm + bandeja chapa galv.
30 Barrera cortafuego lana mineral + intumescente
31 Grapa acero galv. regulable + bulón M12 inox
32 Junta de dilatación 20 mm + manguito
33 Perfil guía de arranque (deslizante)
34 Sellador silicona neutra s/ fondo de junta


PLANTA BAJA Y FUNDACIÓN

35 Solado cerámico s/ adhesivo cementicio
36 Carpeta niveladora MHR 1:1/4:3
37 Carpeta hidrófuga MCI 1:3
38 Contrapiso de H° pobre, e = 12 cm
39 Film de polietileno 200 µ
40 Tosca compactada, e = 15 cm
41 Junta de dilatación EPS 2 cm + sellador
42 Contrapiso armado hasta la fachada
43 Montante colgado del entrepiso
44 Babeta chapa galv. + aislación hidrófuga
45 Vereda de H° peinado s/ tosca
46 Tronco de columna dentro del cuello
47 Anclaje mecánico húmedo (horquillas)
48 Relleno de H° cementicio cuello/columna
49 Armadura de vinculación fundación–columna
50 Cuello de la base, H°A° in situ
51 Base de H°A° colada in situ (s/ cálculo)
52 Armadura de fundación s/ cálculo
53 H° de limpieza, e = 10 cm
54 Terreno natural
55 Broca c/ prisionero Ø9,5 x 80 + tuerca


NUDO 1 · CUBIERTA
Isométrica esc. 1:15

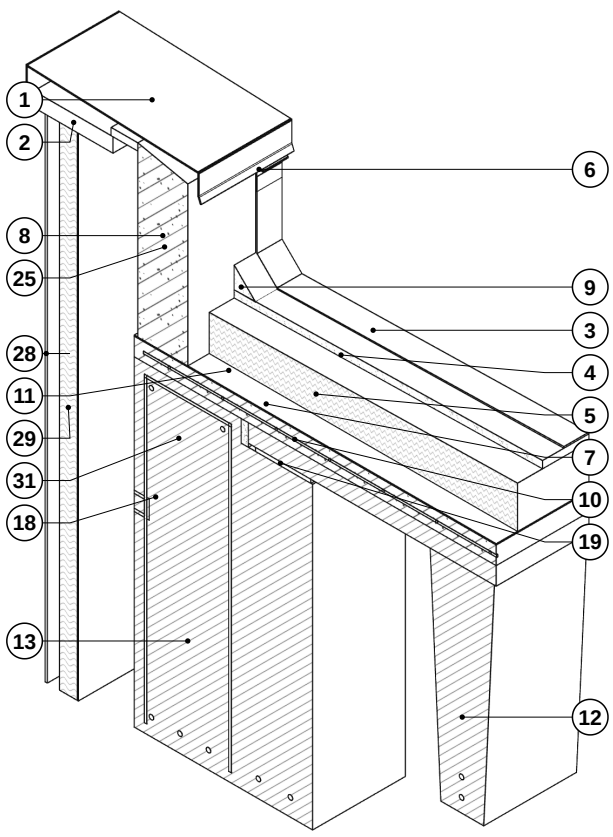

NUDO 2 · ENTREPISO
Isométrica esc. 1:15

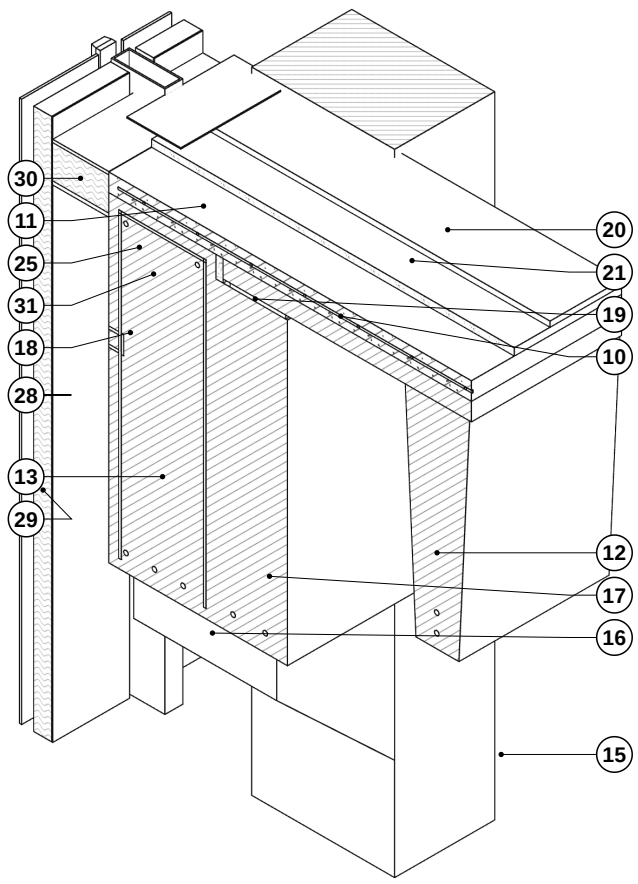

NUDO 3 · PISO S/ TERRENO
Isométrica esc. 1:15

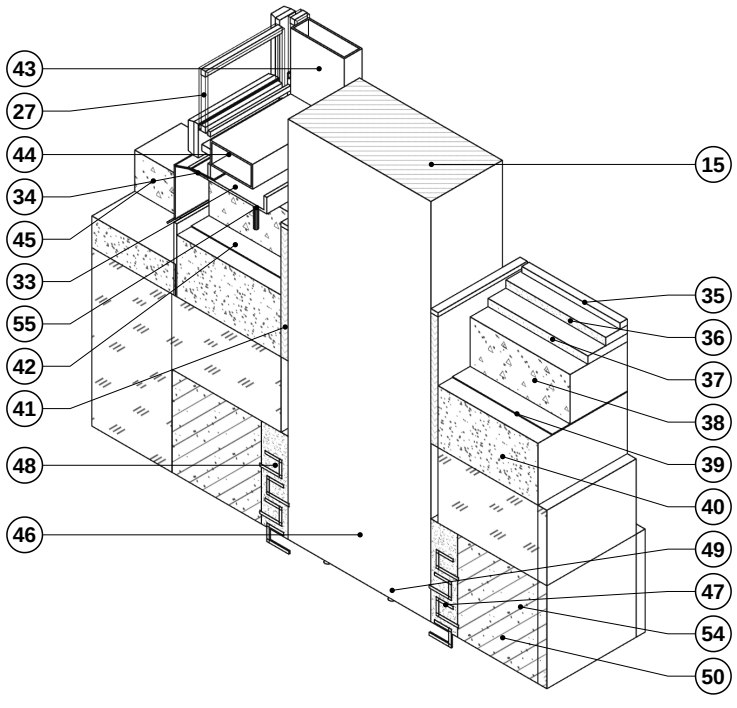

CORTE INTEGRAL 1:20 + NUDOS AXONOMÉTRICOS

H° premoldeado de grandes luces · cerramiento vidriado

MATERIA: Construcciones II
ALUMNO/A: _____
ESCALAS: Corte 1:20 · Nudos 1:15
CÁTEDRA: Arq. Tucci
GRUPO: ____
HOJA: A3 · 2026