CORTE INTEGRAL
CERRAMIENTO OPACO

ESCALA 1:20

REFERENCIAS

1 Cupertina chapa galv. N°22 c/ goterones
2 Tornillo c/ arandela de neopreno + sellador
3 Membrana asfáltica 4 mm c/ aluminio
4 Carpeta 1:3 c/ 10 % hidrófugo, e = 2 cm
5 Contrapiso liviano H° c/ EPS (aislante), pend. 2 %
6 Babeta chapa galv. + sellador en buña del panel
7 Barrera de vapor: imprimación + film 200 µ
8 Junta EPS 2 cm panel / canaleta + sellador
9 Canaleta H°A in situ (hueco semicirc.), pend. 1 %
10 Capa de compresión 5 cm c/ malla Ø6 c/15
11 Estribos salientes Ø10 (anclan canaleta y capa)
12 Panel TT h 0,65: ala y nervios cortados
13 Viga de borde premold. s/ VL (L en entrepiso)
14 Viga VL doble T 40x70 pretensada
15 Columna pretensada 40x40 (en vista)
16 Ménsula de columna c/ diagonal (en vista)
17 Neopreno + perno Ø20 (VL / ménsula)
18 Barras de vinculación VL / L en mortero
19 Ala del TT s/ viga de borde + neopreno
20 Solado cerámico s/ adhesivo cementicio
21 Carpeta niveladora MHR 1:1/4:3, e = 2 cm
22 Cielorraso placa de roca de yeso 12,5 mm
23 Montantes y soleras chapa galv. 35 mm
24 Gancho / vela a los nervios del panel TT
25 Panel sándwich premoldeado H°A, e = 20 cm
26 Hoja ext. H°A 6 cm / hoja int. portante 8 cm
27 Alma EPS 6 cm + conectores de fibra de vidrio
28 Rehundido Ø100 prof. 3 cm tapado c/ mortero
29 Bulón pasante M20: atraviesa panel y ala de VL
30 Agujero ovalado VERTICAL 40x60 (dilatación) + vaina
31 Junta 2 cm: lana mineral cortafuego + sellador
32 Junta perimetral EPS 1 cm + zócalo
33 Junta vertical panel / panel: fondo + sellador PU
34 Sellador PU s/ fondo de junta (junta horizontal)
35 Solado cerámico s/ adhesivo cementicio
36 Carpeta niveladora MHR 1:1/4:3
37 Carpeta hidrófuga MCI 1:3
38 Contrapiso de H° pobre, e = 12 cm
39 Film de polietileno 200 µ
40 Tosca compactada, e = 15 cm
41 Junta EPS 2 cm + faja perimetral EPS 3 cm x 0,60
42 Viga portapanel pretensada 20x85, diente 20x45
43 Mortero de asiento + pasador Ø16 en vaina c/ grout
44 Pintura asfáltica en caras enterradas
45 Vereda de H° peinado s/ tosca
46 Tronco de columna dentro del cuello
47 Anclaje mecánico húmedo (horquillas)
48 Relleno de H° cementicio cuello/columna
49 Armadura de vinculación fundación–columna
50 Cuello de la base, H°A° in situ
51 Base de H°A° colada in situ
52 Armadura de fundación (parrilla inferior)
53 H° de limpieza, e = 10 cm
54 Terreno natural
55 Neopreno de apoyo viga portapanel / cuello
56 Junta vereda / viga EPS 1 cm + sellador
57 Zona maciza local 30x30 en cada anclaje (sin EPS)
58 EPS 25 mm + carpeta armada bajo membrana (canaleta)
59 Embudo c/ rejilla en canaleta (c/ eje col.) a caño interior

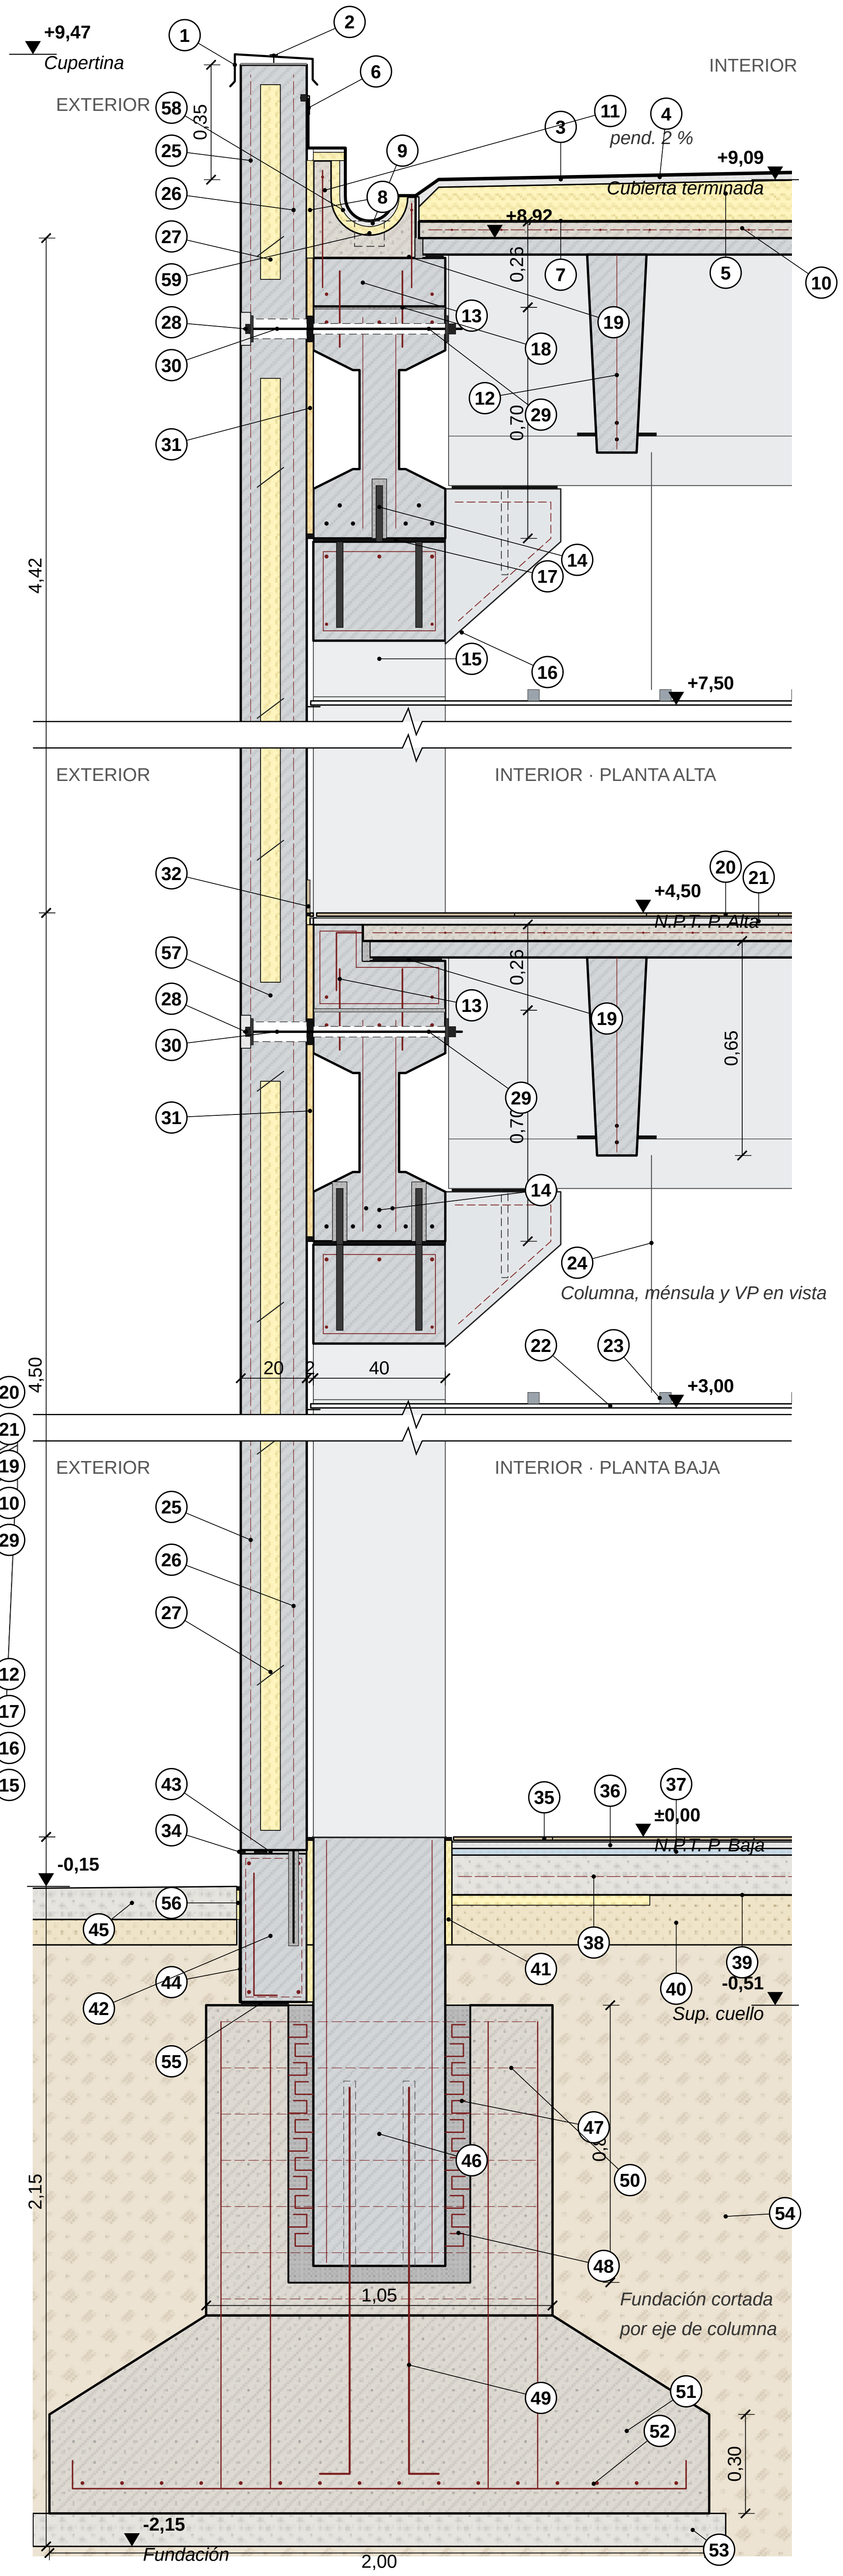

+9,47
Cupertina
1
2
6
EXTERIOR
INTERIOR
58
0,35
11
4
3
pend. 2 %
25
9
+9,09
26
8
Cubierta terminada
27
+8,92
59
0,25
7
5
10
19
13
28
18
30
12
29
31
0,70
4,42
17
14
15
16
+7,50
EXTERIOR
INTERIOR · PLANTA ALTA
20
21
32
+4,50
N.P.T. P. Alta
57
0,26
13
19
28
30
0,65
29
31
0,70
14
24
Columna, ménsula y VP en vista
22
23
20
2
40
4,50
+3,00
EXTERIOR
INTERIOR · PLANTA BAJA
25
26
27
43
35
36
37
±0,00
34
N.P.T. P. Baja
-0,15
56
45
38
41
39
44
40
-0,51
42
Sup. cuello
55
47
46
0,45
50
2,15
54
48
1,05
Fundación cortada
por eje de columna
49
51
52
0,30
-2,15
Fundación
2,00
53

NUDO 1 · CUBIERTA

Isométrica esc. 1:15

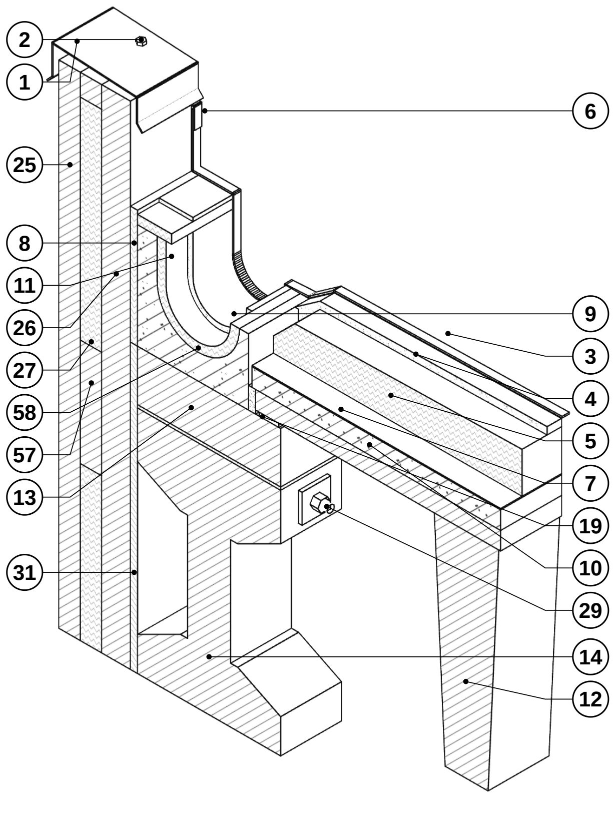

2
1
25
8
11
26
27
58
57
13
31
6
9
3
4
5
7
19
10
29
14
12

NUDO 2 · ENTREPISO

Isométrica esc. 1:15

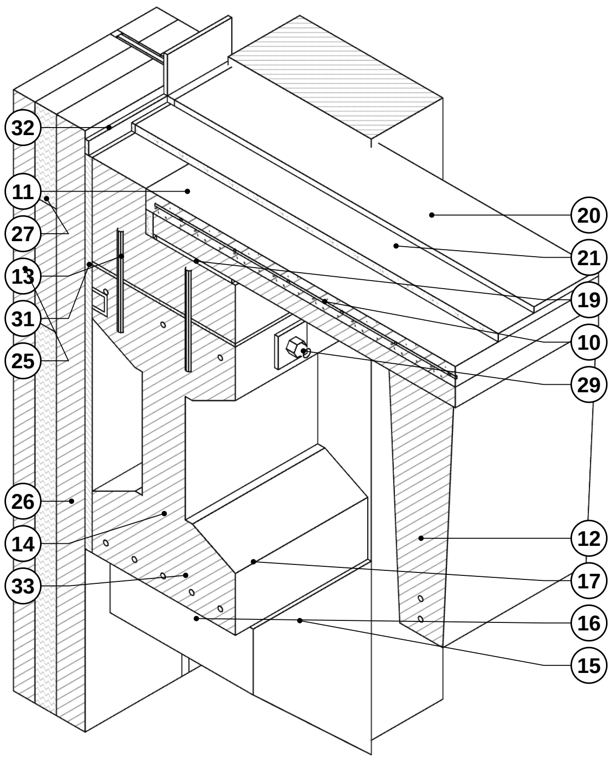

32
11
27
13
31
25
26
14
33
20
21
19
10
29
12
17
16
15

NUDO 3 · PISO

Isométrica esc. 1:15

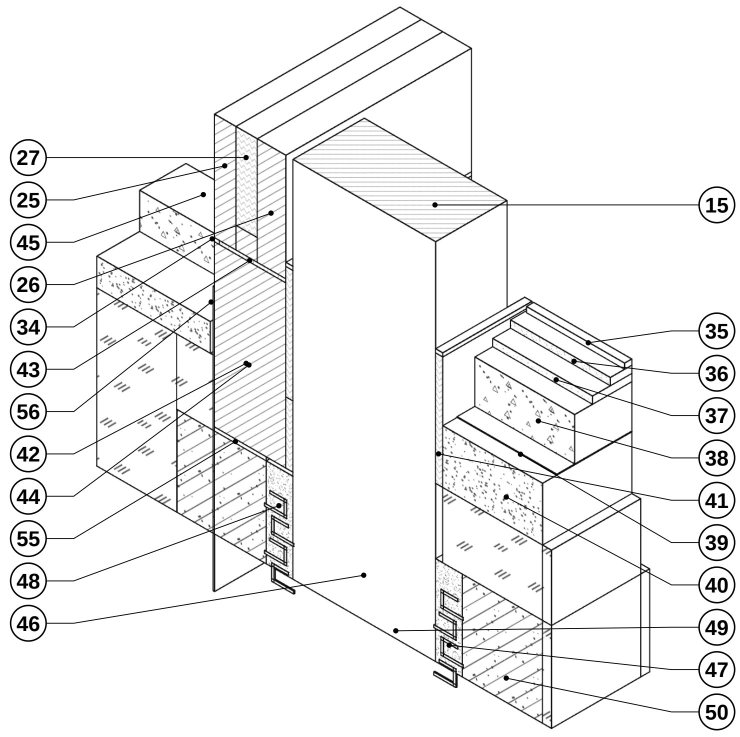

27
25
45
26
34
43
56
42
44
55
48
46
15
35
36
37
38
41
39
40
49
47
50

TP FINAL
FECHA: 19/10/2026

DOCENTE: Arq. Tucci y Arq. Cardozo
ALUMNA: Candelaria Vitale
GRUPO: 13

NIVEL:
OBS:

CONSTRUCCIONES II
CATEDRA: ARQ. TUCCI