
# CORTE INTEGRAL
# CERRAMIENTO OPACO

ESCALA 1:20


## REFERENCIAS

**1** Cupertina chapa galv. N°22 c/ goterones
**2** Tornillo c/ arandela de neopreno + sellador
**3** Membrana asfáltica 4 mm c/ aluminio
**4** Carpeta 1:3 c/ 10 % hidrófugo, e = 2 cm
**5** Contrapiso liviano H° c/ EPS (aislante), pend. 2 %
**6** Babeta chapa galv. + sellador en buña del panel
**7** Barrera de vapor: imprimación + film 200 µ
**8** Junta EPS 2 cm panel / canaleta + sellador
**9** Canaleta H°A in situ (hueco semicirc.), pend. 1 %
**10** Capa de compresión 5 cm c/ malla Ø6 c/15
**11** Estribos salientes Ø10 (anclan canaleta y capa)
**12** Panel TT h 0,65: ala y nervios cortados
**13** Viga de borde premold. s/ VL (L en entrepiso)
**14** Viga VL doble T 40x70 pretensada
**15** Columna pretensada 40x40 (en vista)
**16** Ménsula de columna c/ diagonal (en vista)
**17** Neopreno + perno Ø20 (VL / ménsula)
**18** Barras de vinculación VL / L en mortero
**19** Ala del TT s/ viga de borde + neopreno
**20** Solado cerámico s/ adhesivo cementicio
**21** Carpeta niveladora MHR 1:1/4:3, e = 2 cm
**22** Cielorraso placa de roca de yeso 12,5 mm
**23** Montantes y soleras chapa galv. 35 mm
**24** Gancho / vela a los nervios del panel TT
**25** Panel sándwich premoldeado H°A, e = 20 cm
**26** Hoja ext. H°A 6 cm / hoja int. portante 8 cm
**27** Alma EPS 6 cm + conectores de fibra de vidrio
**28** Rehundido Ø100 prof. 3 cm tapado c/ mortero
**29** Bulón pasante M20: atraviesa panel y ala de VL
**30** Agujero ovalado VERTICAL 40x60 (dilatación) + vaina
**31** Junta 2 cm: lana mineral cortafuego + sellador
**32** Junta perimetral EPS 1 cm + zócalo
**33** Junta vertical panel / panel: fondo + sellador PU
**34** Sellador PU s/ fondo de junta (junta horizontal)
**35** Solado cerámico s/ adhesivo cementicio
**36** Carpeta niveladora MHR 1:1/4:3
**37** Carpeta hidrófuga MCI 1:3
**38** Contrapiso de H° pobre, e = 12 cm
**39** Film de polietileno 200 µ
**40** Tosca compactada, e = 15 cm
**41** Junta EPS 2 cm + faja perimetral EPS 3 cm x 0,60
**42** Viga portapanel pretensada 20x85, diente 20x45
**43** Mortero de asiento + pasador Ø16 en vaina c/ grout
**44** Pintura asfáltica en caras enterradas
**45** Vereda de H° peinado s/ tosca
**46** Tronco de columna dentro del cuello
**47** Anclaje mecánico húmedo (horquillas)
**48** Relleno de H° cementicio cuello/columna
**49** Armadura de vinculación fundación–columna
**50** Cuello de la base, H°A° in situ
**51** Base de H°A° colada in situ
**52** Armadura de fundación (parrilla inferior)
**53** H° de limpieza, e = 10 cm
**54** Terreno natural
**55** Neopreno de apoyo viga portapanel / cuello
**56** Junta vereda / viga EPS 1 cm + sellador
**57** Zona maciza local 30x30 en cada anclaje (sin EPS)
**58** EPS 25 mm + carpeta armada bajo membrana (canaleta)
**59** Embudo c/ rejilla en canaleta (c/ eje col.) a caño interior


### NUDO 1 · CUBIERTA
Isométrica esc. 1:15

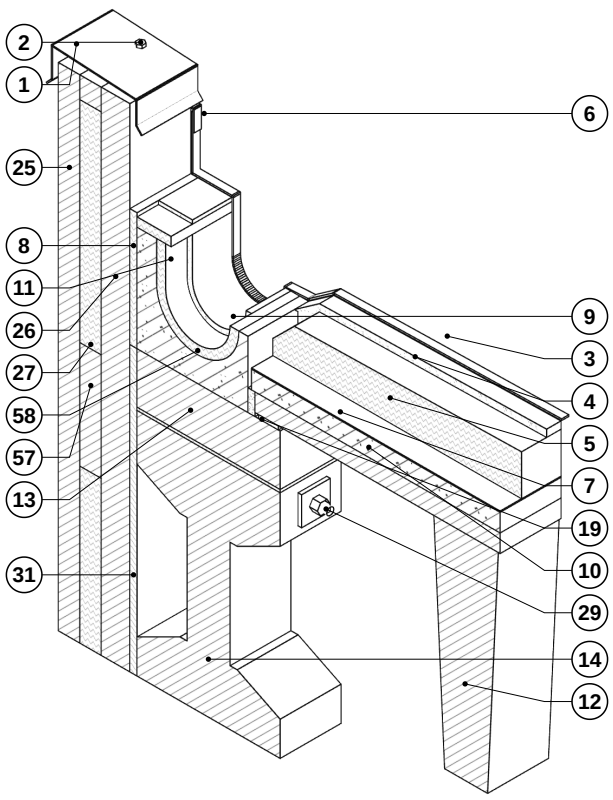



### NUDO 2 · ENTREPISO
Isométrica esc. 1:15

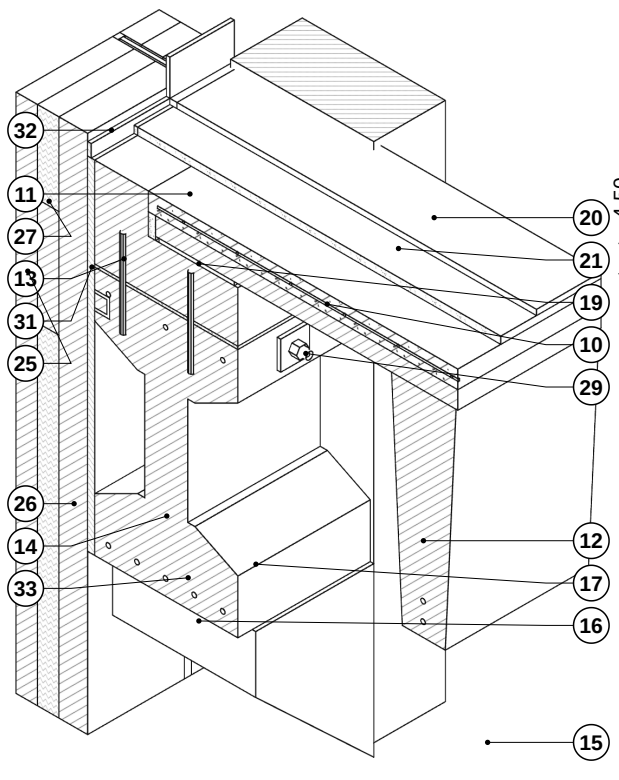


### NUDO 3 · PISO
Isométrica esc. 1:15

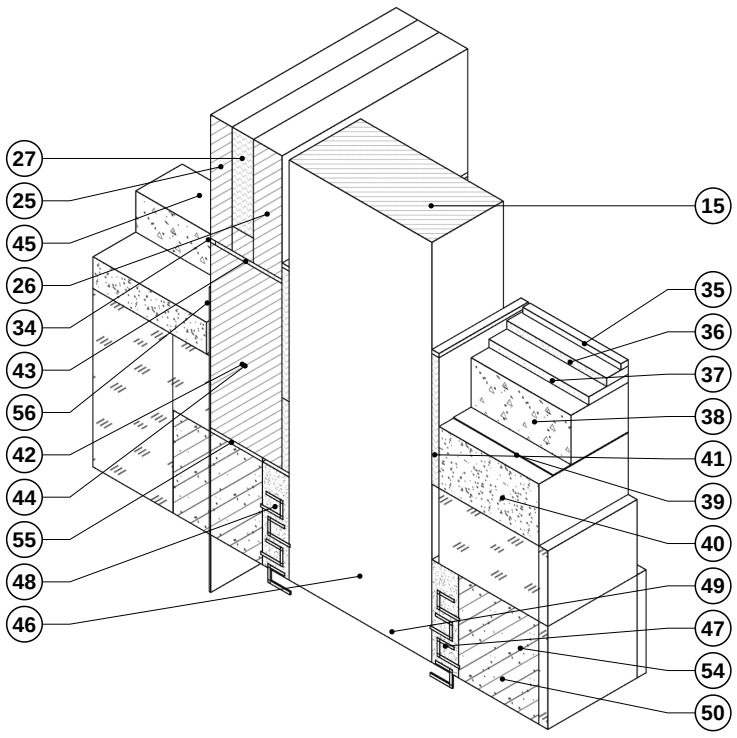

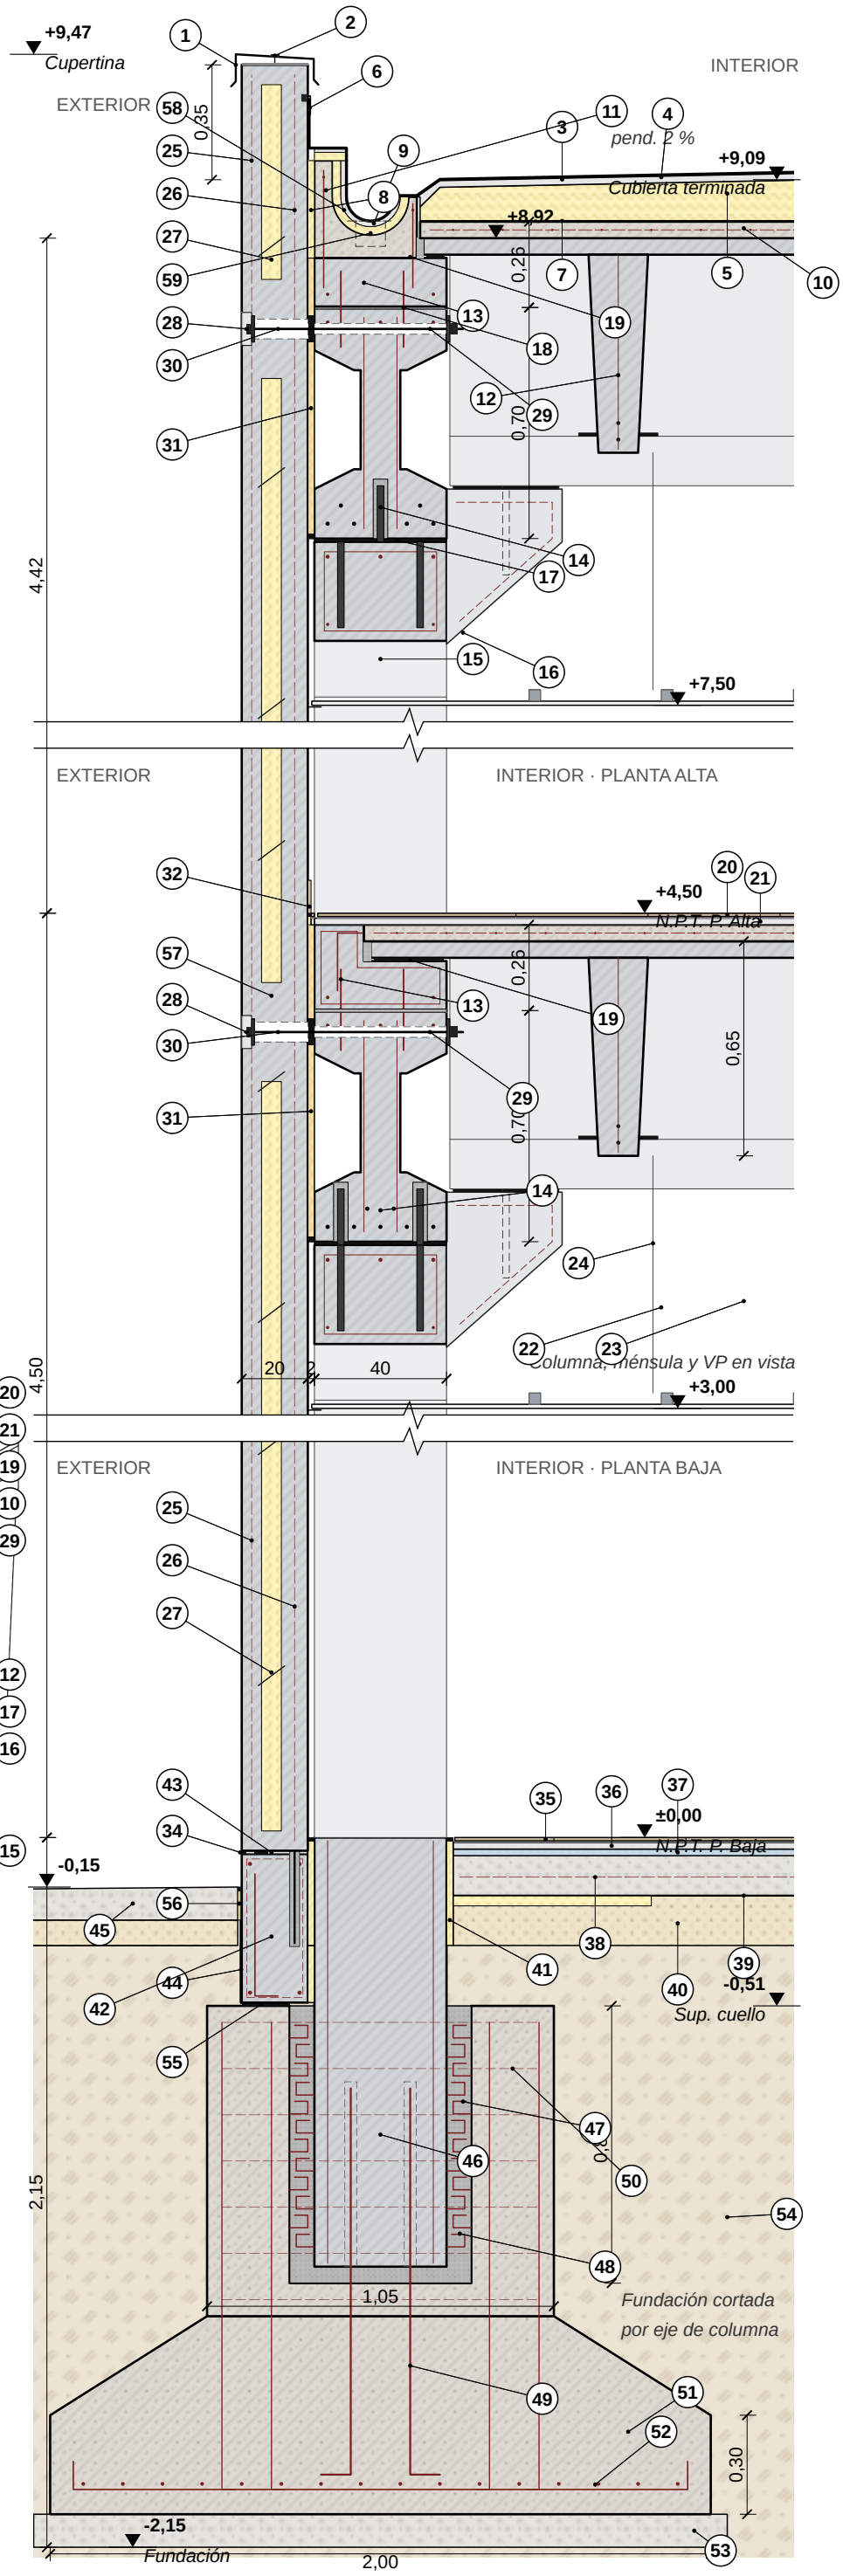
| | | | |
|---|---|---|---|
| **TP FINAL**<br>FECHA: 19/10/2026 | DOCENTE: Arq. Tucci y Arq. Cardozo<br>ALUMNA: Candelaria Vitale<br>GRUPO: 13 | NIVEL:<br>OBS: | CONSTRUCCIONES II<br>CATEDRA: ARQ. TUCCI |