
AXONOMETRÍA ISOMÉTRICA INFERIOR · CIELORRASO SUSPENDIDO

ESC. 1:15


Vista desde abajo con placas retiradas en parte: estructura de chapa galvanizada colgada de la losa

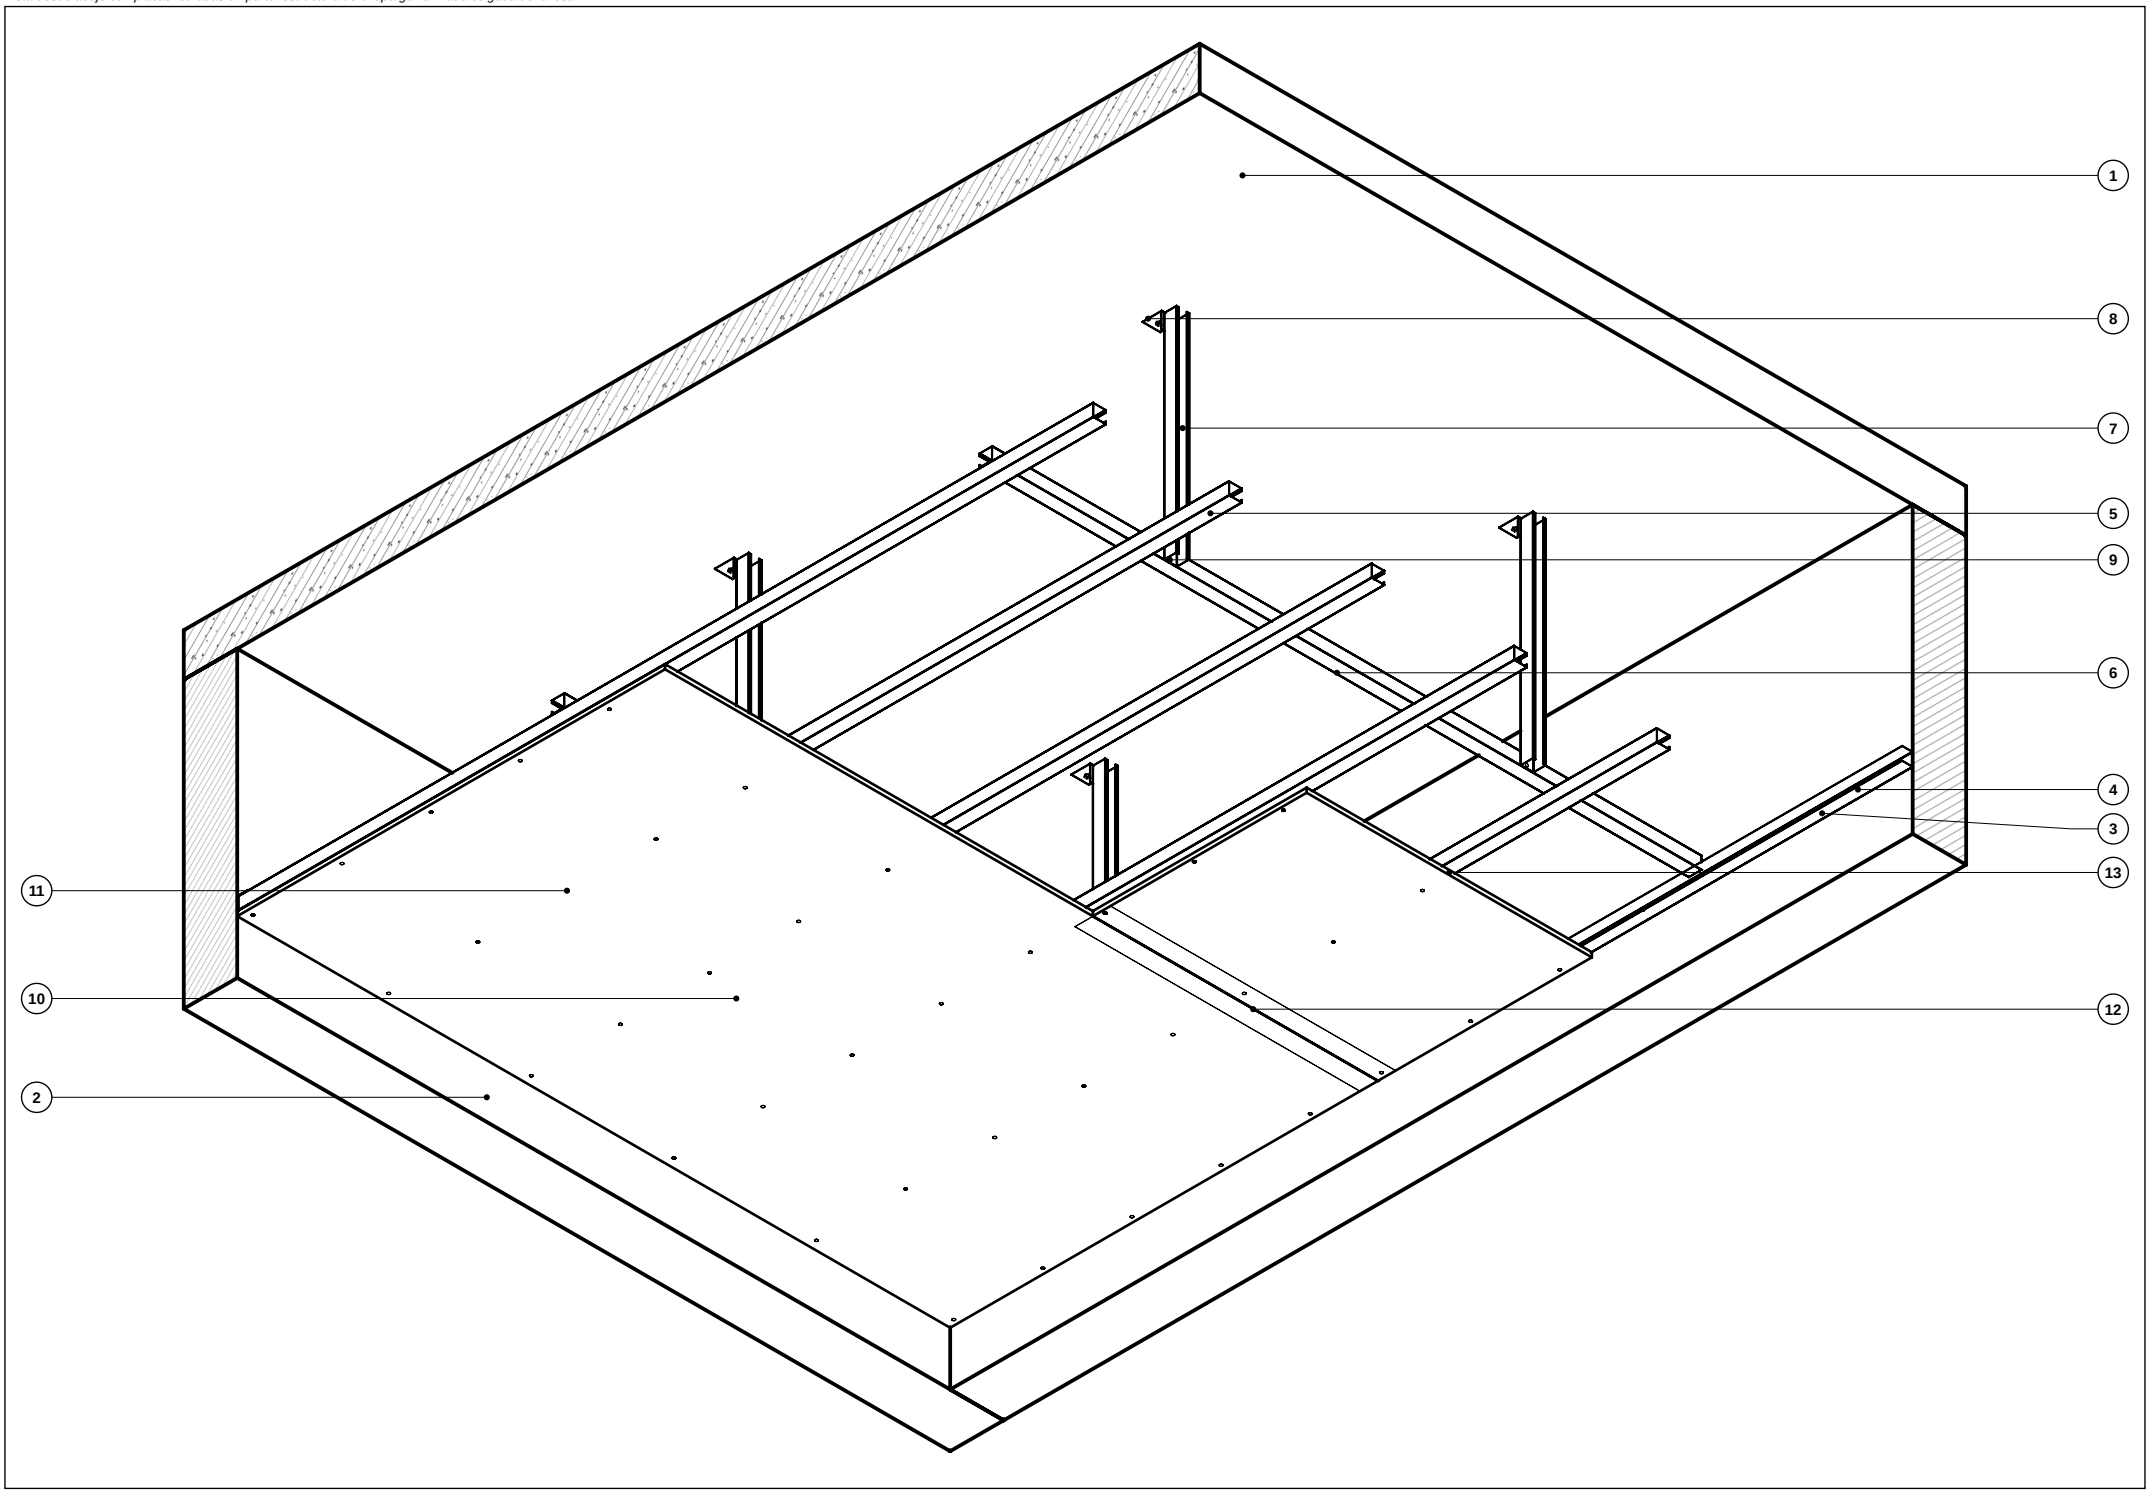

DETALLE A · ANCLAJE A LOSA

ESC. 1:5


Isometría inferior

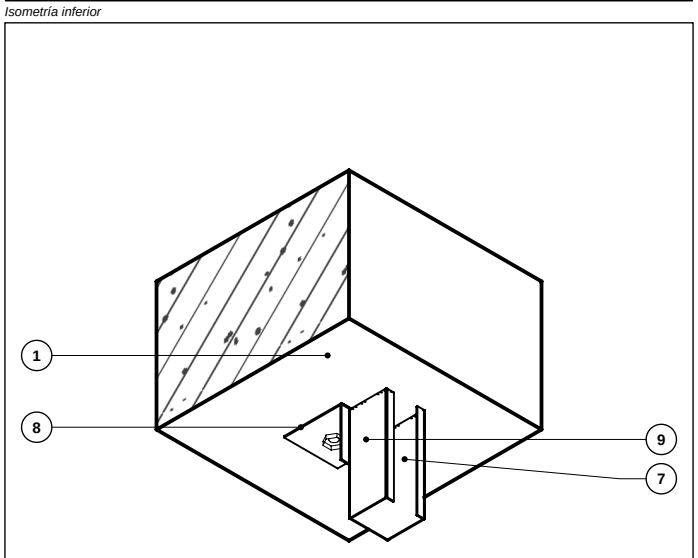

DETALLE B · MAESTRA – MONTANTE

ESC. 1:5


Isometría superior (desde el pleno)

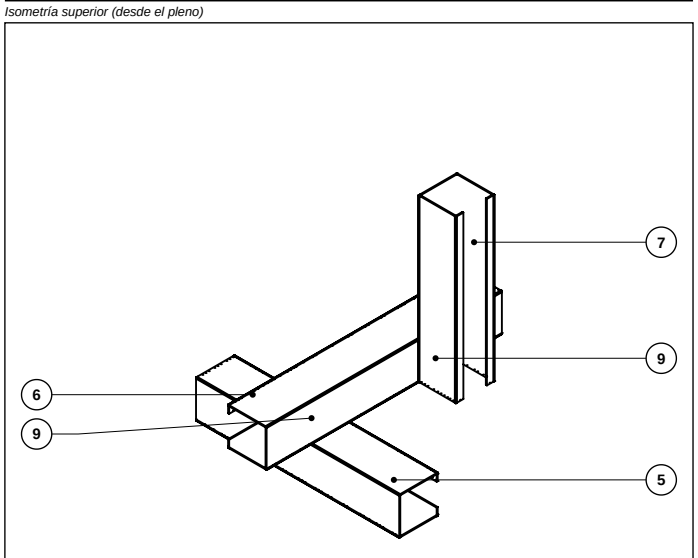

DETALLE C · ENCUENTRO CON MURO

ESC. 1:10

Isometría inferior

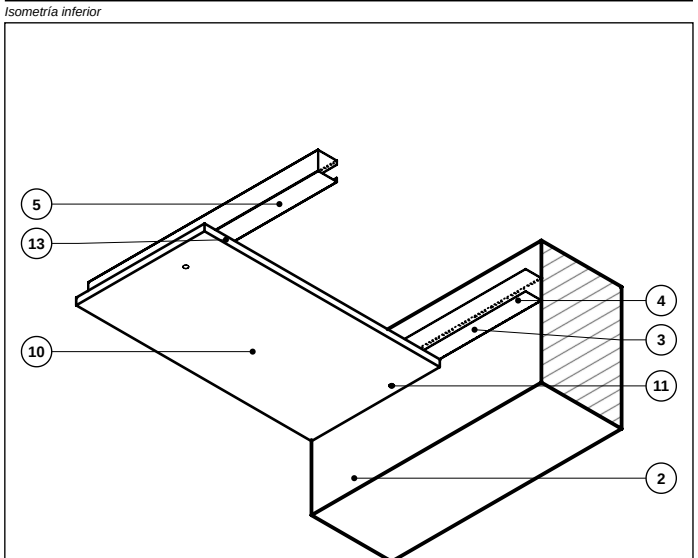

REFERENCIAS

1. Losa de H°A° (e = 12 cm) – cara inferior
2. Muro de mampostería revocada
3. Solera perimetral PGU 35 x 28 x 0,52 mm (chapa galv.)
4. Fijación de solera: tarugo nylon Ø 8 + tornillo c/ 60 cm
5. Montante secundario PGC 34 x 35 x 0,52 mm c/ 40 cm, encastrado en la solera
6. Viga maestra (montante 34) c/ 1,20 m, perpendicular a los secundarios
7. Vela rígida (montante 34) c/ 1,00 m sobre cada maestra
8. Ángulo de anclaje galv. + broca metálica Ø 8 a la losa
9. Tornillos T1 (punta aguja) en uniones perfil–perfil
10. Placa de roca de yeso estándar 12,5 mm (1,20 x 2,40 m), lado largo perpendicular a montantes
11. Tornillos T2 c/ 25 cm sobre montantes y soleras
12. Junta tomada: cinta de papel microperforada + masilla (3 manos)
13. Borde de placa (canto) – placa atornillada a la cara inferior de los montantes

NOTAS

Separaciones: montantes c/ 0,40 m · maestras c/ 1,20 m · velas c/ 1,00 m · tornillos T2 c/ 0,25 m (0,20 m en bordes). Pleno libre ≈ 0,60 m.
Placas trabadas, lado largo perpendicular a los montantes, juntas sobre perfil. Perfiles de chapa galvanizada Z275, e = 0,52 mm. Medidas en mm.

GROSORES DE LÍNEA: 0,5 mm · Cortes (losa, muro) — 0,35 mm · Placas — 0,25 mm · Perfiles — 0,13 mm · Fijaciones / referencias

CIELORRASO TÉCNICO SUSPENDIDO · AXONOMETRÍA

Sistema en seco (steel frame): placas de roca de yeso 12,5 mm sobre perfiles de chapa galvanizada colgados de la losa

MATERIA	CÁTEDRA	ALUMNO/A	GRUPO	FECHA	HOJA
Construcciones II	Arq. _____	_____	____	05/11/2026	A3 · 1/1