

CORTE INTEGRAL ACERO FRENTE INTEGRAL. ESC 1.10

REFERENCIAS

1. CUPERTINA ZINGUERÍA ESTANCA
2. AISLACIÓN HIDRÓFUGA MEMBRANA ASFÁLTICA
3. CARPETA DE NIVELACIÓN MHR
4. CONTRAPISO H°LIVIANO
5. BARRERA DE VAPOR FILM POLIETILENO 200µ
6. CAPA DE COMPRESIÓN SOBRE MALLA ELECTROSOLADA
7. SEPARADOR DE HORMIGÓN PARA MALLA ELECTROSOLDADA
8. CONECTORES DE CORTANTE SOBRE VIGA IPN
9. CERRAMIENTO EXTERIOR VERTICAL TERMOPANELES SANDWICH CON NÚCLEO DE POLIURETANO 40MM
10. PERFIL L PARA PAQUETE DE CONTRAPISO
11. ESTRUCTURA SECUNDARIA PARA PANELES VERTICALES: PERFIL OMEGA Y SUJECION INFERIOR PERFIL Z
12. ZINGUERIA DE BORDE CON SUJECIÓN A CHAPA GALVADECK
13. VIGA IPN 200 CON ANCLAJE A COLUMNA MEDIANTE UNIÓN SOLDADA Y MECÁNICA DE BULONES
14. PERFIL Z BUÑA EN CIELORRASO INDEPENDIENTE
15. CIELORRASO PLACA DURLOCK e= 9.5 mm
16. VIGA IPN 180 CON ANCLAJE A COLUMNA MEDIANTE UNIÓN SOLDADA Y MECÁNICA DE BULONES
17. PLACA COLABORANTE GALVADECK PARA LOSA
18. PERFIL C CON BANDA DE NEOPRENO FIJADO A VIGA PARA CIELORRASO INDEPENDIENTE
19. ZINGUERIA A MEDIDA PARA CERRAMIENTO Y BUÑA
20. FRENTE INTEGRAL: TRAVESAÑO CON MT-0817 TAPA INTERIOR Y MT-0819 TAPA EXTERIOR. ANCLAJE DE BULÓN A PERFIL IPN
21. FRENTE INTEGRAL: COLUMNA CON MT-0817 TAPA INTERIOR Y MT-0819 TAPA EXTERIOR. ANCLAJE DE BULÓN A PERFIL IPN
22. DOBLE VIDRIO HERMÉTICO
23. PERFIL HEB 200 COLUMNA
24. SELLADOR JUNTA + BANDA DE NEOPRENO
25. ZINGUERIA A MEDIDA ALFEIZAR CON PENDIENTE
26. BARANDA POSAPIE PARA PROTECCIÓN ACERO INOXIDABLE
27. SOLADO SOBRE ADHESIVO CEMENTICIO
28. AISLACIÓN TÉRMICA: PLACA DE EPS 40MM
29. PLATABANDA PARA ANCLAJE A FUNDACIÓN Y COLUMNA SOLDADA
30. TUERCA / CONTRATUERCA / TUERCA DE NIVELACIÓN
31. PERNOS DE ANCLAJE A FUNDACIÓN
32. SEPARADOR DE SUELO FILM POLIETILENO 200µ
33. CARPETA HIDRÓFUGA MCI + 10% ADITIVO HIDRÓFUGO
34. ZAPATA DE H° A° ARMADURA SEGÚN CÁLCULO
35. SUELO COMPACTO

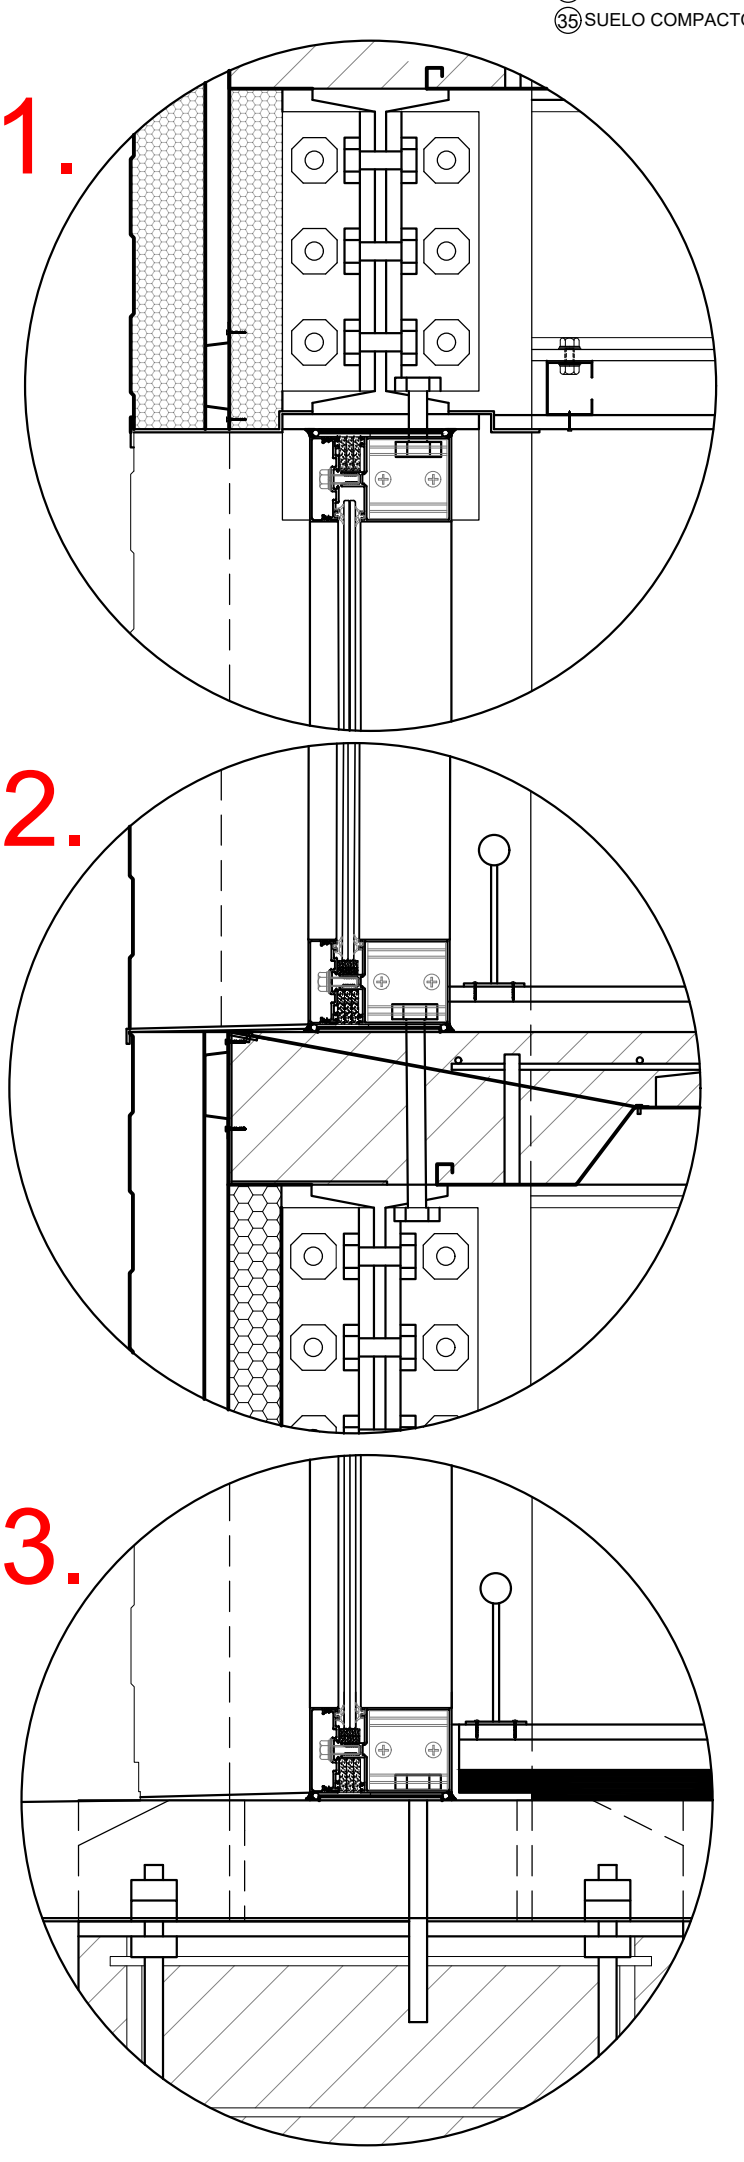

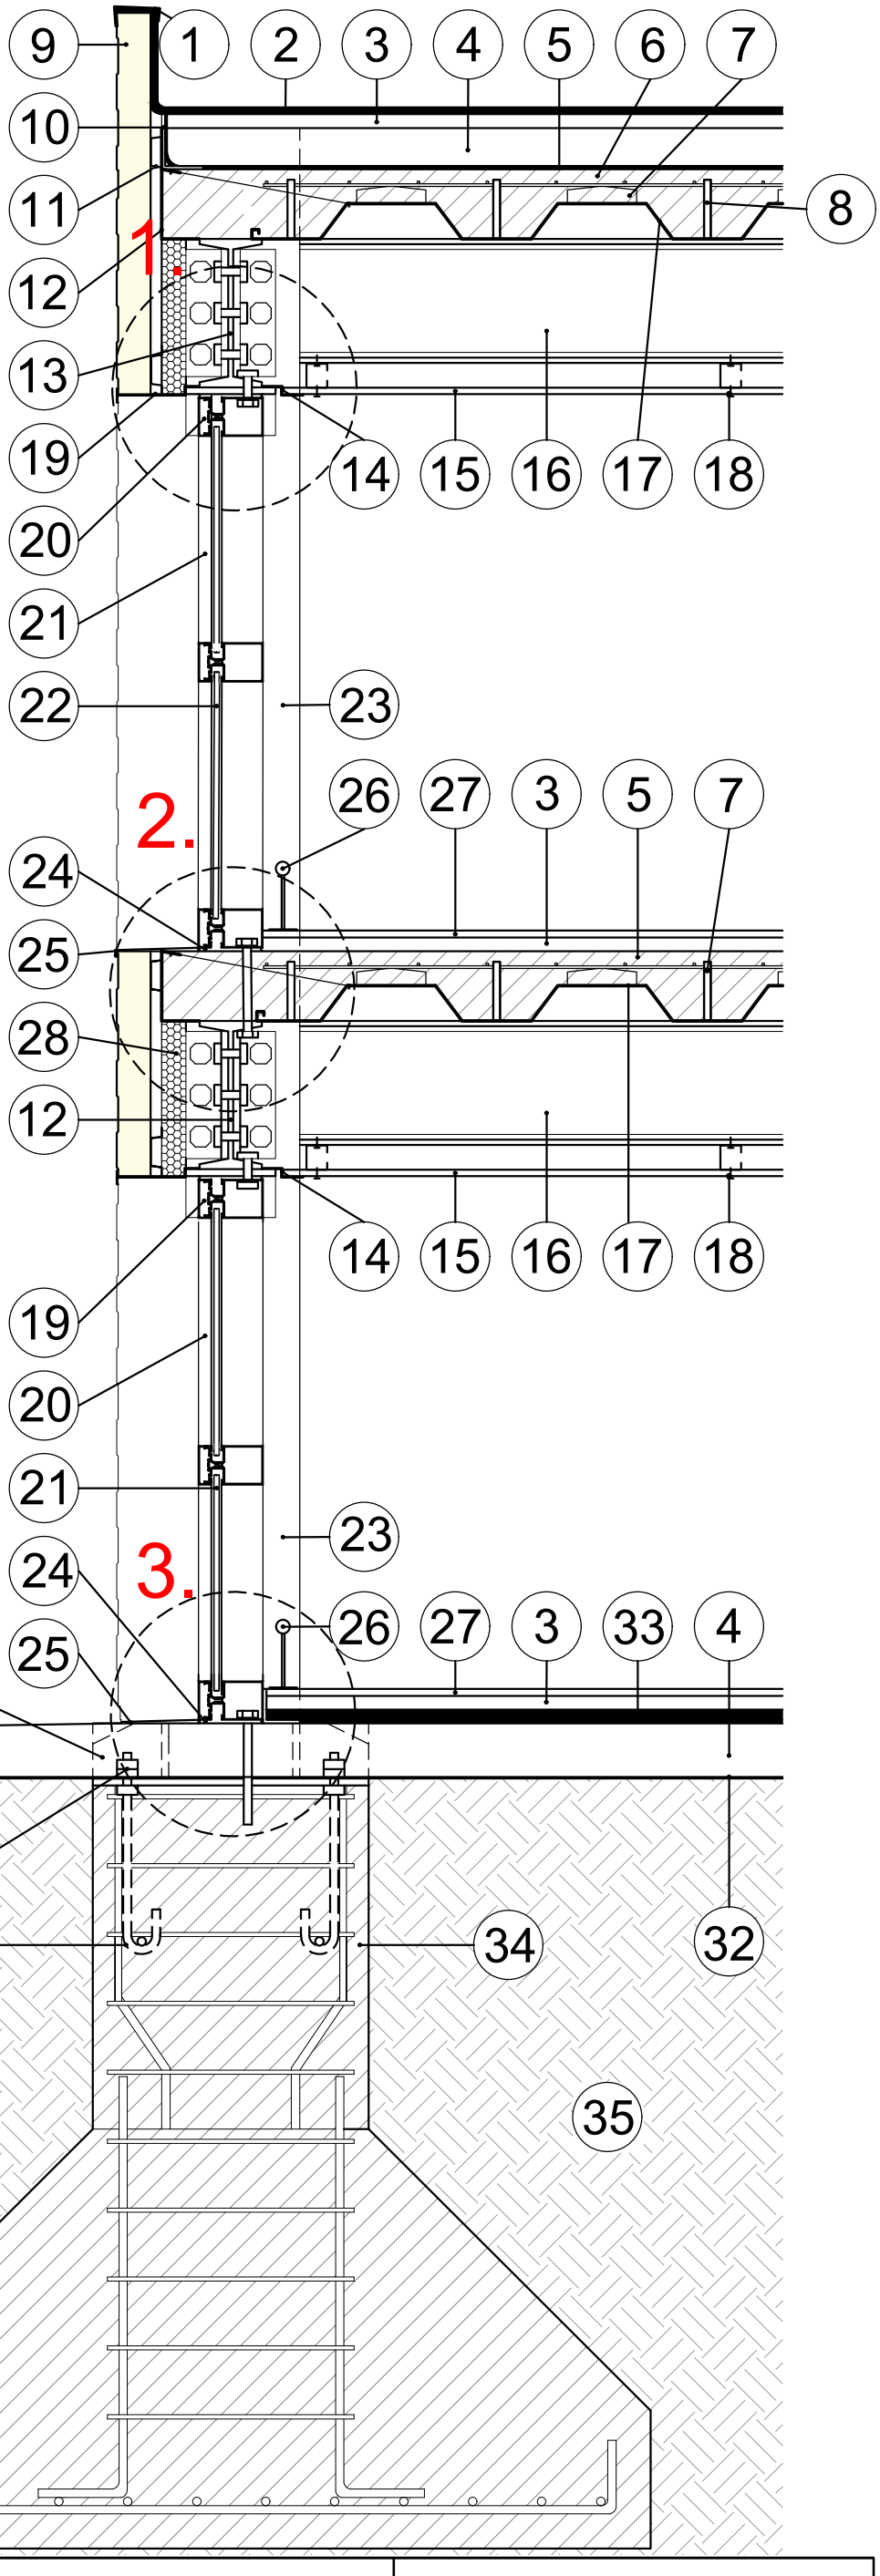

TP N°4 FECHA: 28/09/2026	DOCENTE: ALUMNO: GALDAMES, ABRIL GRUPO: 2	NIVEL: OBS:	CONSTRUCCIONES II CATEDRA: ARQ. TUCCI