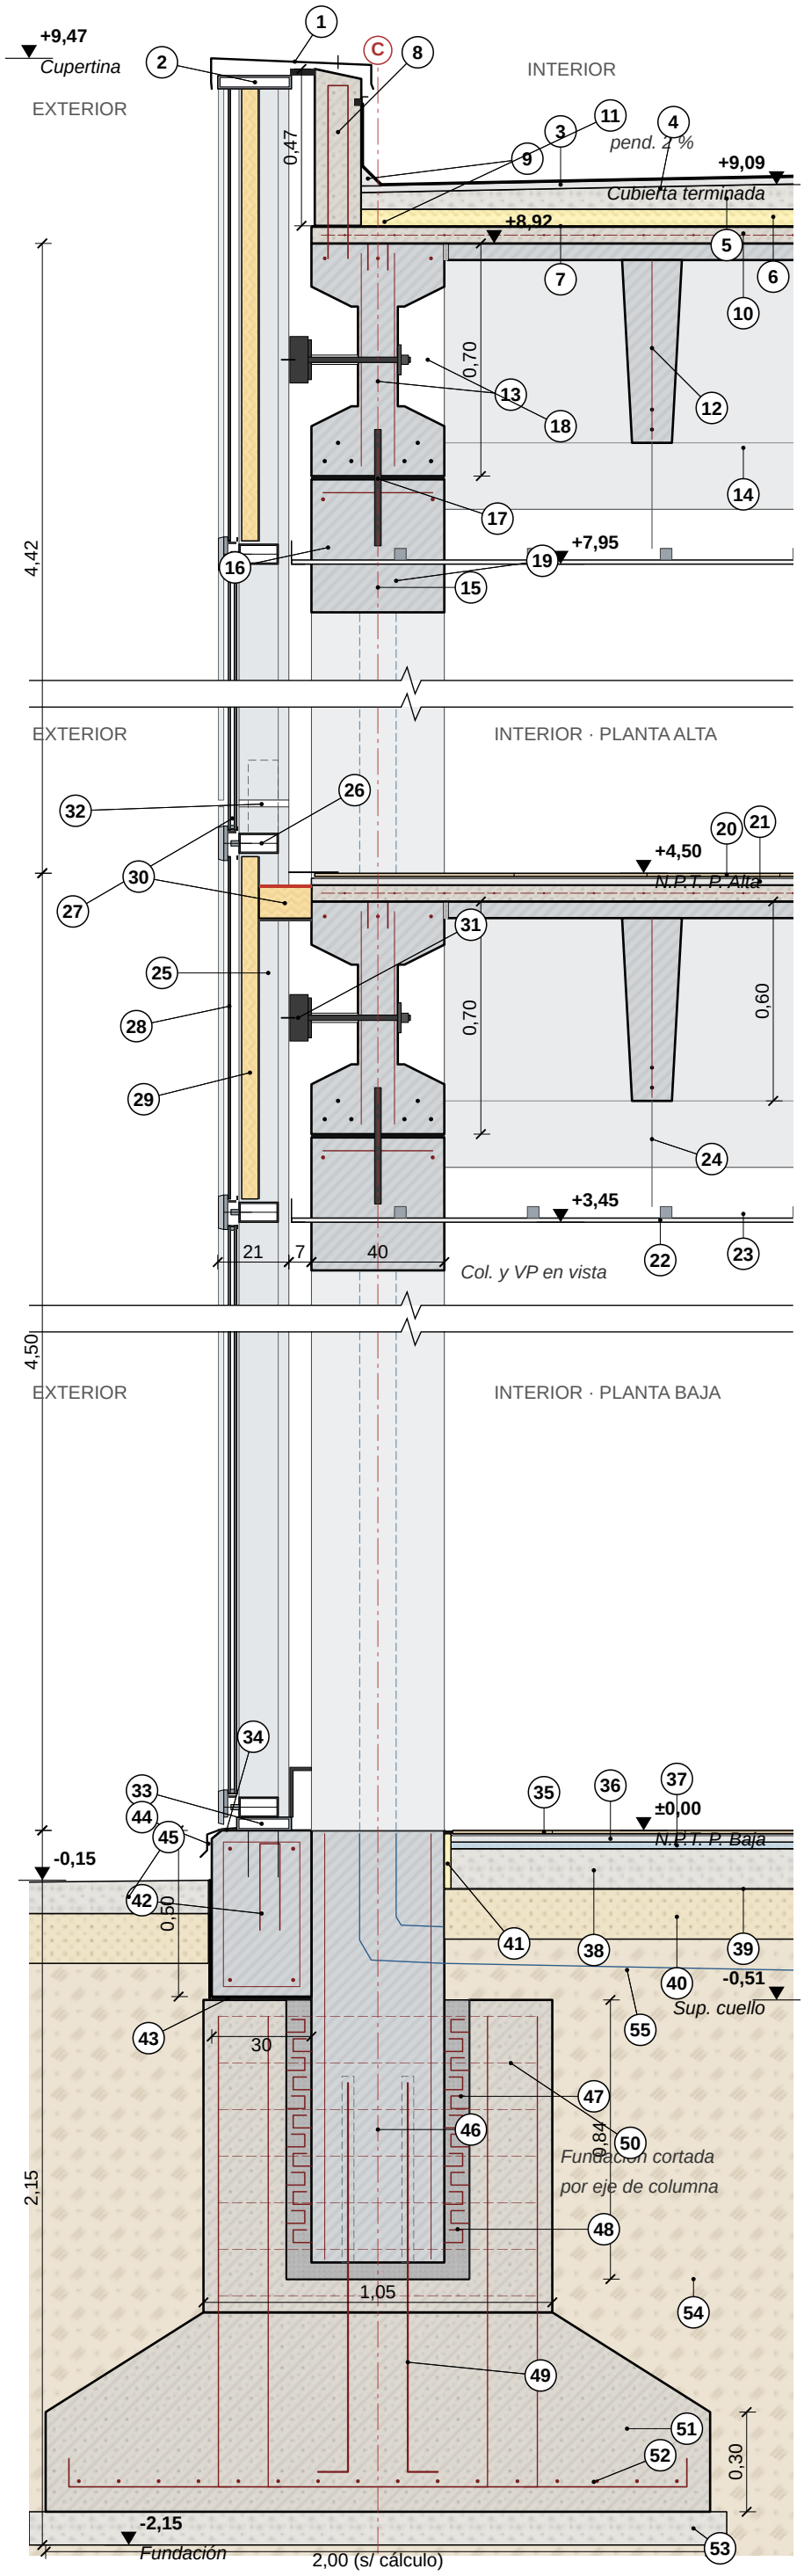


CORTE INTEGRAL — ESC. 1:20

0 50 cm

REFERENCIAS (corte integral y nudos)

CUBIERTA

1 Cupertina chapa galv. N°22 c/ goterones
2 Perfil de cierre sup. muro cortina + sellador
3 Membrana asfáltica 4 mm c/ aluminio + babeta
4 Carpeta 1:3 c/ 10 % hidrófugo, e = 2 cm
5 Contrapiso liviano H° c/ EPS, pend. 2 %
6 Aislación térmica EPS 30 kg/m³, e = 5 cm
7 Barrera de vapor: imprimación + film 200 µ
8 Zócalo sup. H°A° in situ c/ barras de atado
9 Media caña de mortero

ESTRUCTURA PREMOLDEADA (SISTEMA PI)

10 Capa de compresión 5 cm c/ malla Ø6 c/15
11 Estribos salientes de la VL (2Ø10)
12 Panel TT pretensado, apoyado en VP
13 Viga pretensada VL 40x70 (doble T)
14 Viga pretensada VP (en vista)
15 Columna pretensada 40x40 (en vista)
16 Ménsula de columna p/ apoyo de viga
17 Neopreno c/ perno de fijación Ø20
18 Bulón pasante Ø3/4" + arandela Ø90 + sellado
19 Caño pluvial PVC Ø110 en la columna

ENTREPISO Y CIELORRASOS

20 Solado cerámico s/ adhesivo cementicio
21 Carpeta niveladora MHR 1:1/4:3, e = 2 cm
22 Cielorraso placa de roca de yeso 12,5 mm
23 Montantes y soleras chapa galv. 35 mm
24 Gancho / vela a los nervios del panel TT

MURO CORTINA (STICK, MÓDULO 1,25 m)


25 Montante de aluminio 50x150 (en vista)
26 Travesaño + presor + tapa + burletes EPDM
27 DVH 6 templado + 12 + 3+3 laminado PVB
28 Spandrel: vidrio templado 6 mm esmaltado
29 Lana mineral 50 mm + bandeja chapa galv.
30 Barrera cortafuego lana mineral + intumescente
31 Grapa acero galv. regulable + bulón M12 inox
32 Junta de dilatación 20 mm + manguito
33 Perfil de arranque alum. c/ drenaje
34 Sellador silicona neutra s/ fondo de junta

PLANTA BAJA Y FUNDACIÓN

35 Solado cerámico s/ adhesivo cementicio
36 Carpeta niveladora MHR 1:1/4:3
37 Carpeta hidrófuga MCI 1:3
38 Contrapiso de H° pobre, e = 12 cm
39 Film de polietileno 200 µ
40 Tosca compactada, e = 15 cm
41 Junta perimetral EPS 2 cm + sellador
42 Viga perimetral portamuro (VPP) 30x50
43 Banda de neopreno s/ cuello
44 Babeta chapa galv. + aislación hidrófuga
45 Vereda de H° peinado s/ tosca
46 Tronco de columna dentro del cuello
47 Anclaje mecánico húmedo (horquillas)
48 Relleno de H° cementicio cuello/columna
49 Armadura de vinculación fundación–columna
50 Cuello de la base, H°A° in situ
51 Base de H°A° colada in situ (s/ cálculo)
52 Armadura de fundación s/ cálculo
53 H° de limpieza, e = 10 cm
54 Terreno natural
55 Caño pluvial PVC Ø110 a cámara y colectora


NUDO 1 · CUBIERTA

Isométrica esc. 1:15

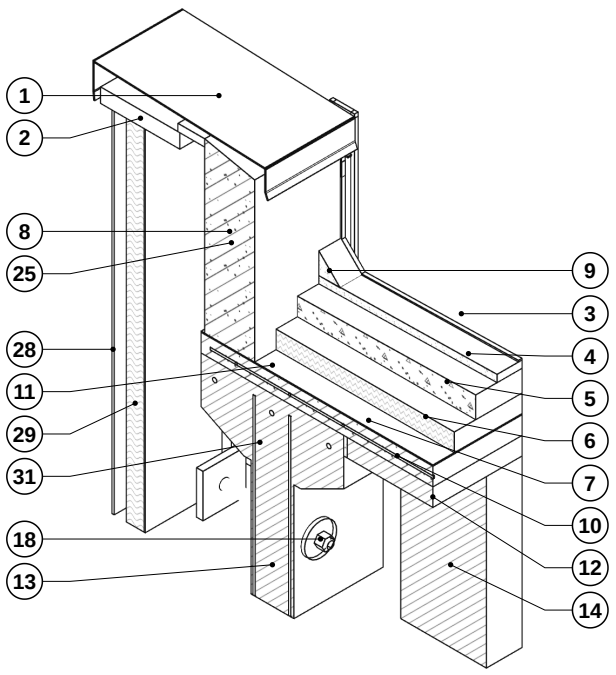


NUDO 2 · ENTREPISO

Isométrica esc. 1:15

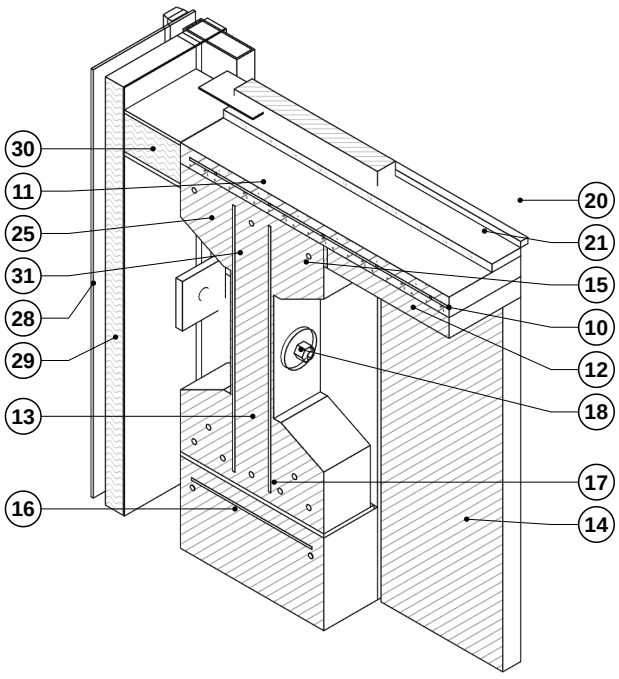

NUDO 3 · PISO S/ TERRENO

Isométrica esc. 1:12,5

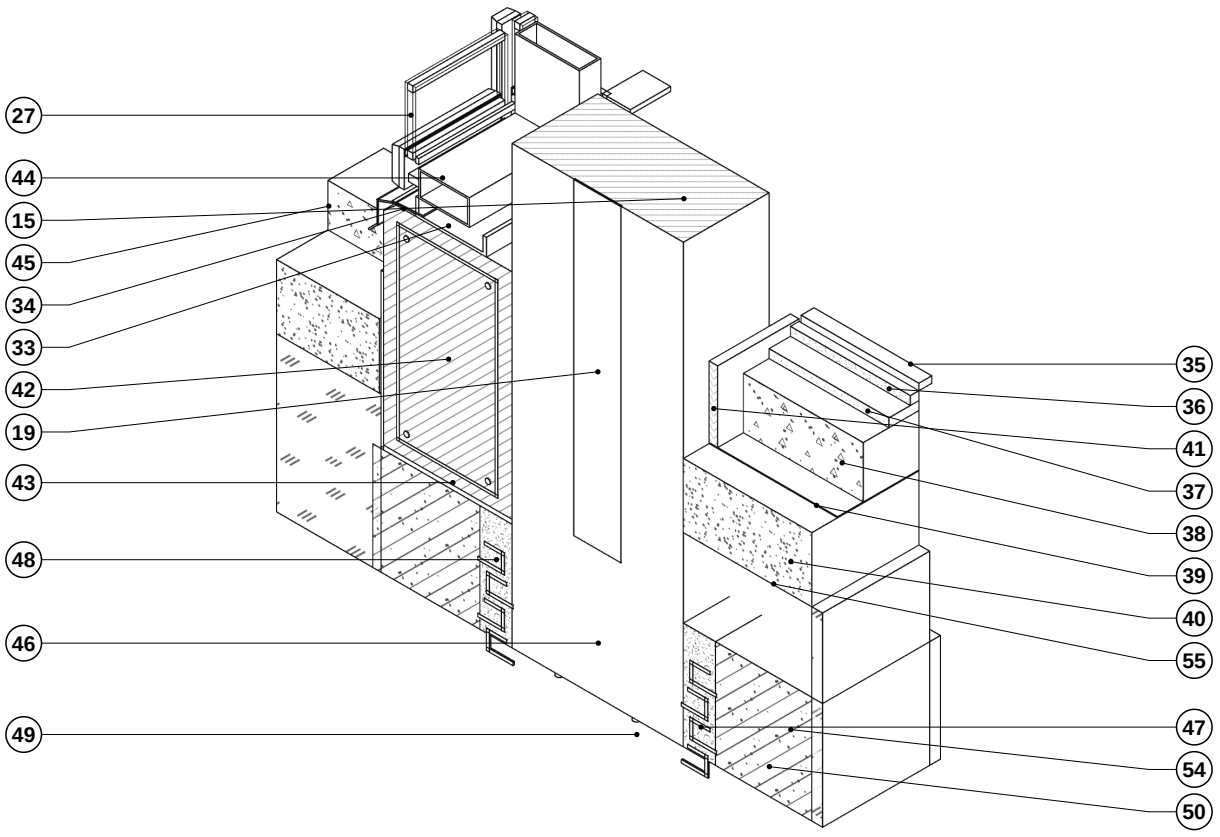

CORTE INTEGRAL 1:20 + NUDOS AXONOMÉTRICOS

H° premoldeado de grandes luces · cerramiento vidriado

MATERIA: Construcciones II
ALUMNO/A: _____
ESCALAS: indicadas
CÁTEDRA: Arq. Tucci
GRUPO: ____
HOJA: A3 · 2026