
1º ELEMENTOS DEL SISTEMA · AXONOMETRÍA

Isométrica 1:250 · módulo 10,00 x 15,00 m · sin parte de la cubierta y sin vidrios para mostrar el armado

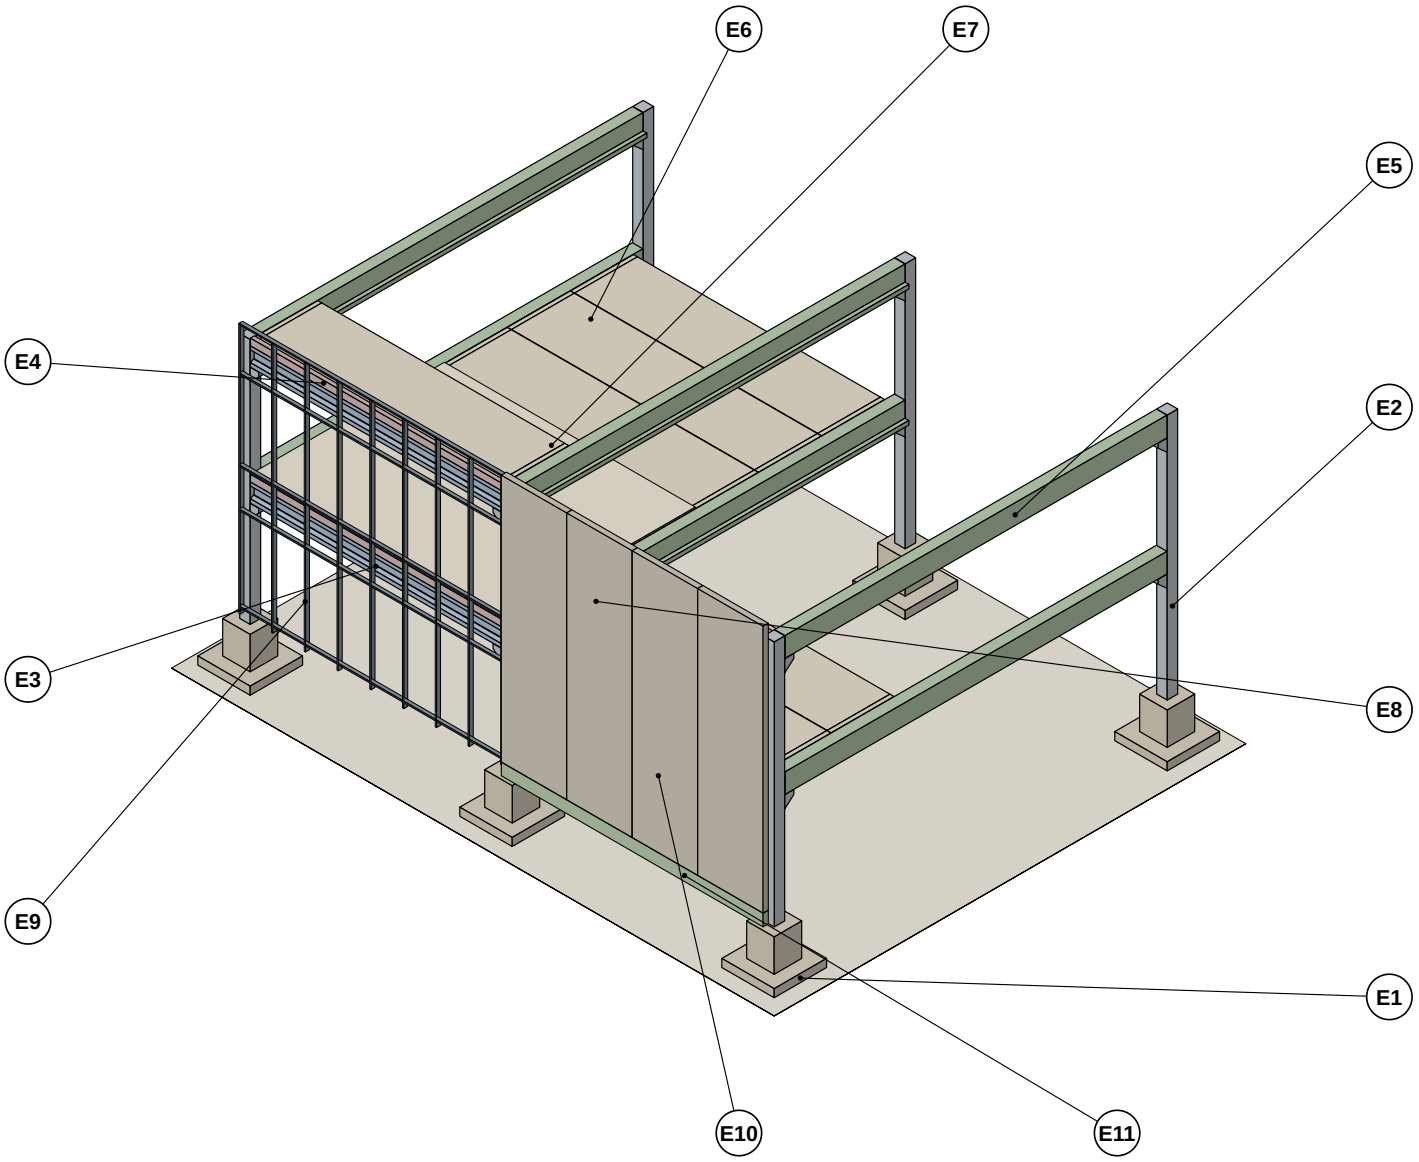

REFERENCIAS · ELEMENTOS DEL SISTEMA

- **E1** Fundación tipo cáliz (base + cuello H°A° in situ)
- **E2** Columna premoldeada pretensada 40x40 c/ ménsulas cortas
- **E3** Viga VL doble T 40x70 pretensada (fachada)
- **E4** Viga L de borde premoldeada (s/ VL, recibe el TT)
- **E5** Viga VP T invertida h 0,75 (portante principal, luz 15 m)
- **E6** Panel TT h 0,65 x 2,40 (entrepiso y cubierta, luz 10 m)
- **E7** Capa de compresión H°A° in situ e = 5 cm c/ malla
- **E8** Apoyos y conectores: neopreno, pernos, grout, riel
- **E9** Muro cortina stick (cerramiento vidriado)
- **E10** Panel sándwich premoldeado e = 20 cm (opaco)
- **E11** Viga portapanel pretensada 20x85 (arranque del panel)

C2 · PRÁCTICA EN CLASE H° premoldeado de grandes luces	DOCENTE: Arq. Tucci y Arq. Cardozo ALUMNA: Candelaria Vitale · GRUPO 13	**CONSTRUCCIONES II** CÁTEDRA: ARQ. TUCCI
SISTEMA · LISTA GRÁFICA DE ELEMENTOS Escalas: axonometría isométrica 1:250 (longitudes verdaderas s/ ejes)		**LÁMINA 02/26** A4 vertical · 22/10/2026