
# 4º CERRAMIENTOS · E10 PANEL SÁNDWICH PREMOLDEADO

Panel de H°A° con aislación incorporada, colgado de la VL con bulones (fija panel) y apoyado en la viga portapanel


## ALZADO (2 paneles)

Vista exterior 1:100

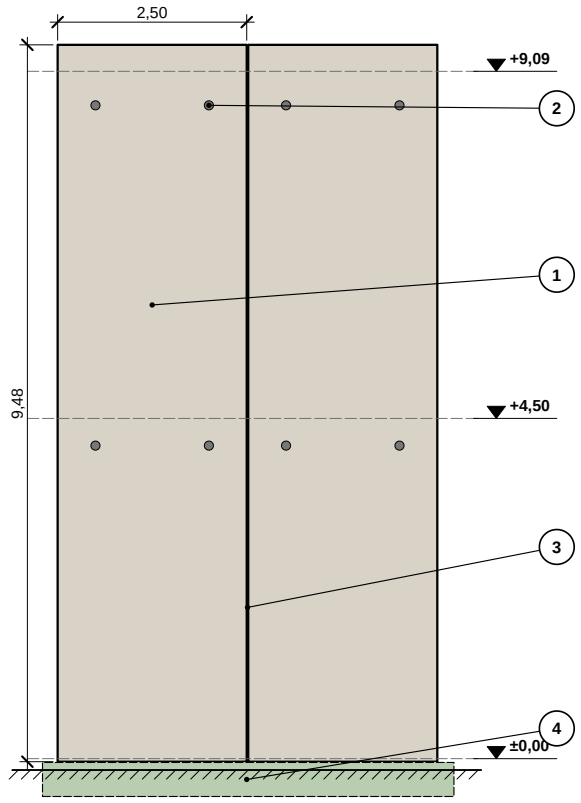


## CORTE


esc. 1:100

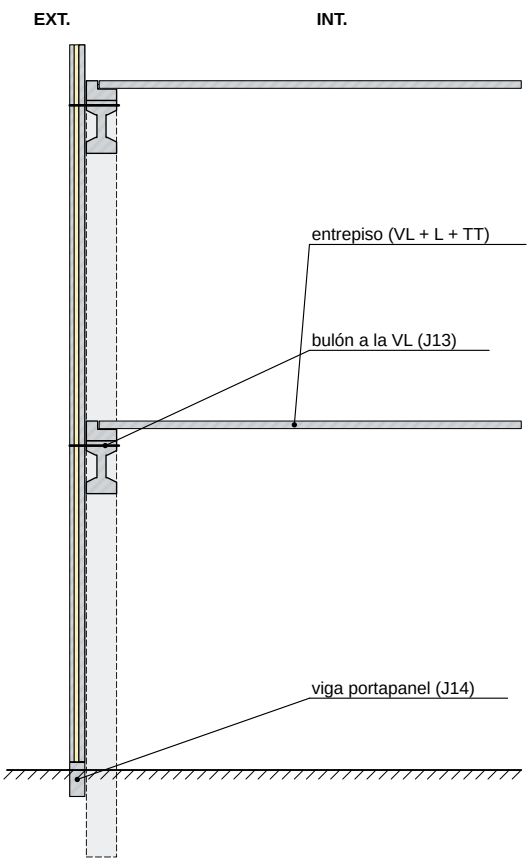


1. Panel sándwich 2,50 x 9,48 x 0,20 m (≈ 8,3 t)
2. Fija panel: bulón M20 (rehundido tapado)
3. Junta vertical 20 mm (J15)
4. Viga portapanel E11 (bajo el nivel de piso)

## SECCIÓN HORIZONTAL DEL PANEL

esc. 1:25 · zona de anclaje maciza y junta entre paneles

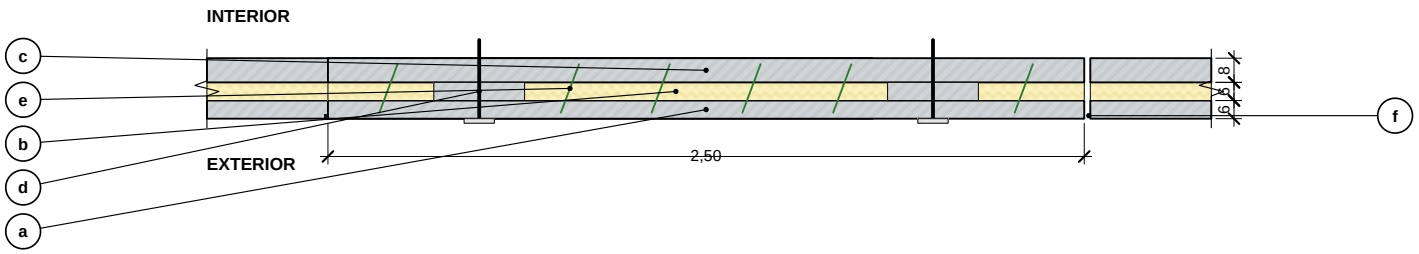


a. Hoja exterior H°A° 6 cm (texturada)
b. Alma EPS 6 cm (20 kg/m³)
c. Hoja interior PORTANTE H°A° 8 cm
d. Zona maciza 30x30 en cada anclaje
e. Conectores de fibra de vidrio
f. Junta 20 mm: cordón + sellador PU

| | | |
|---|---|---|
| **C2 · PRÁCTICA EN CLASE**<br>H° premoldeado de grandes luces | DOCENTE: Arq. Tucci y Arq. Cardozo<br>ALUMNA: Candelaria Vitale · GRUPO 13 | **CONSTRUCCIONES II**<br>CÁTEDRA: ARQ. TUCCI |
| **E10 · PANEL SÁNDWICH · CROQUIS**<br>Escalas: alzado y corte 1:100 · sección del panel 1:25 | | **LÁMINA 23/26**<br>A4 vertical · 22/10/2026 |