
CORTE INTEGRAL
MURO CORTINA


ESCALA 1:20

REFERENCIAS


1 Cupertina chapa galv. N°22 c/ goterones
2 Perfil de cierre sup. muro cortina + sellador
3 Membrana asfáltica 4 mm c/ aluminio + babeta
4 Carpeta de nivelación 1:3 c/ hidrófugo, e = 2 cm
5 Film de polietileno 200 µ (separador)
6 Contrapiso H° c/ EPS alta dens., pend. 2 %
7 Pintura asfáltica (barrera de vapor)
8 Agregado H°A° in situ s/ viga L (borde)
9 Media caña de mortero
10 Babeta chapa galv. + sellador en buña
11 Capa de compresión 5 cm c/ malla Ø6 c/15
12 Estribos salientes viga L (2Ø10)
13 Losa hueca pretensada SHAP h 16 (cortada)
14 Viga L de borde s/ VL (recibe la losa)
15 Viga VL doble T 40x70 pretensada
16 Columna pretensada 40x40 (en vista)
17 Ménsula de columna p/ VL (cortada)
18 Neopreno 10 mm: apoyo VL s/ ménsula
19 Riel de anclaje embutido + bulón T
20 Losa s/ talón viga L: neopreno + grout
21 2 pernos Ø20 en vainas c/ grout (antivuelco)
22 Junta VL / viga L: grout + barras Ø12
23 Viga VP doble T pretensada (en vista)
24 Ménsula + neopreno + perno: apoyo VP (vista)
25 Losa s/ VP: neopreno; juntas c/ grout
26 Perfil L galv. de borde anclado a viga L
27 Solado cerámico s/ adhesivo cementicio
28 Carpeta de nivelación MHR 1:1/4:3, e = 2 cm
29 Contrapiso liviano H° c/ perlita, e = 7 cm
30 Mullion: montante alum. 50x150
31 Travesaño + presor + tapa + burletes EPDM
32 DVH 6 templado + 12 + 3+3 laminado PVB
33 Spandrel: vidrio templado 6 mm esmaltado
34 Aislación: lana 50 mm en bandeja galv.
35 Cortafuego: lana + sellador s/ ángulo galv.
36 Grapa acero galv. regulable + bulón M12 inox
37 Junta de dilatación 20 mm + manguito
38 Perfil guía de arranque (deslizante)
39 Sellador silicona neutra s/ fondo de junta
40 Solado cerámico s/ adhesivo cementicio
41 Carpeta niveladora MHR 1:1/4:3
42 Carpeta hidrófuga MCI 1:3 c/ 10 % aditivo
43 Contrapiso de H° pobre, e = 12 cm
44 Film de polietileno 200 µ
45 Tosca compactada, e = 15 cm
46 Junta de dilatación EPS 2 cm + sellador
47 Contrapiso armado hasta la fachada
48 Montante colgado del entrepiso
49 Babeta chapa galv. + aislación hidrófuga
50 Vereda de H° peinado s/ tosca
51 Tronco de columna dentro del cuello
52 Relleno de H° cementicio cuello/columna
53 Armadura de vinculación base–cuello
54 Cuello de la base, H°A° in situ
55 Zapata de H°A° colada in situ
56 Armadura de zapata: parrilla Ø12 c/15
57 H° de limpieza, e = 10 cm
58 Suelo natural
59 Broca c/ prisionero Ø9,5 x 80 + tuerca

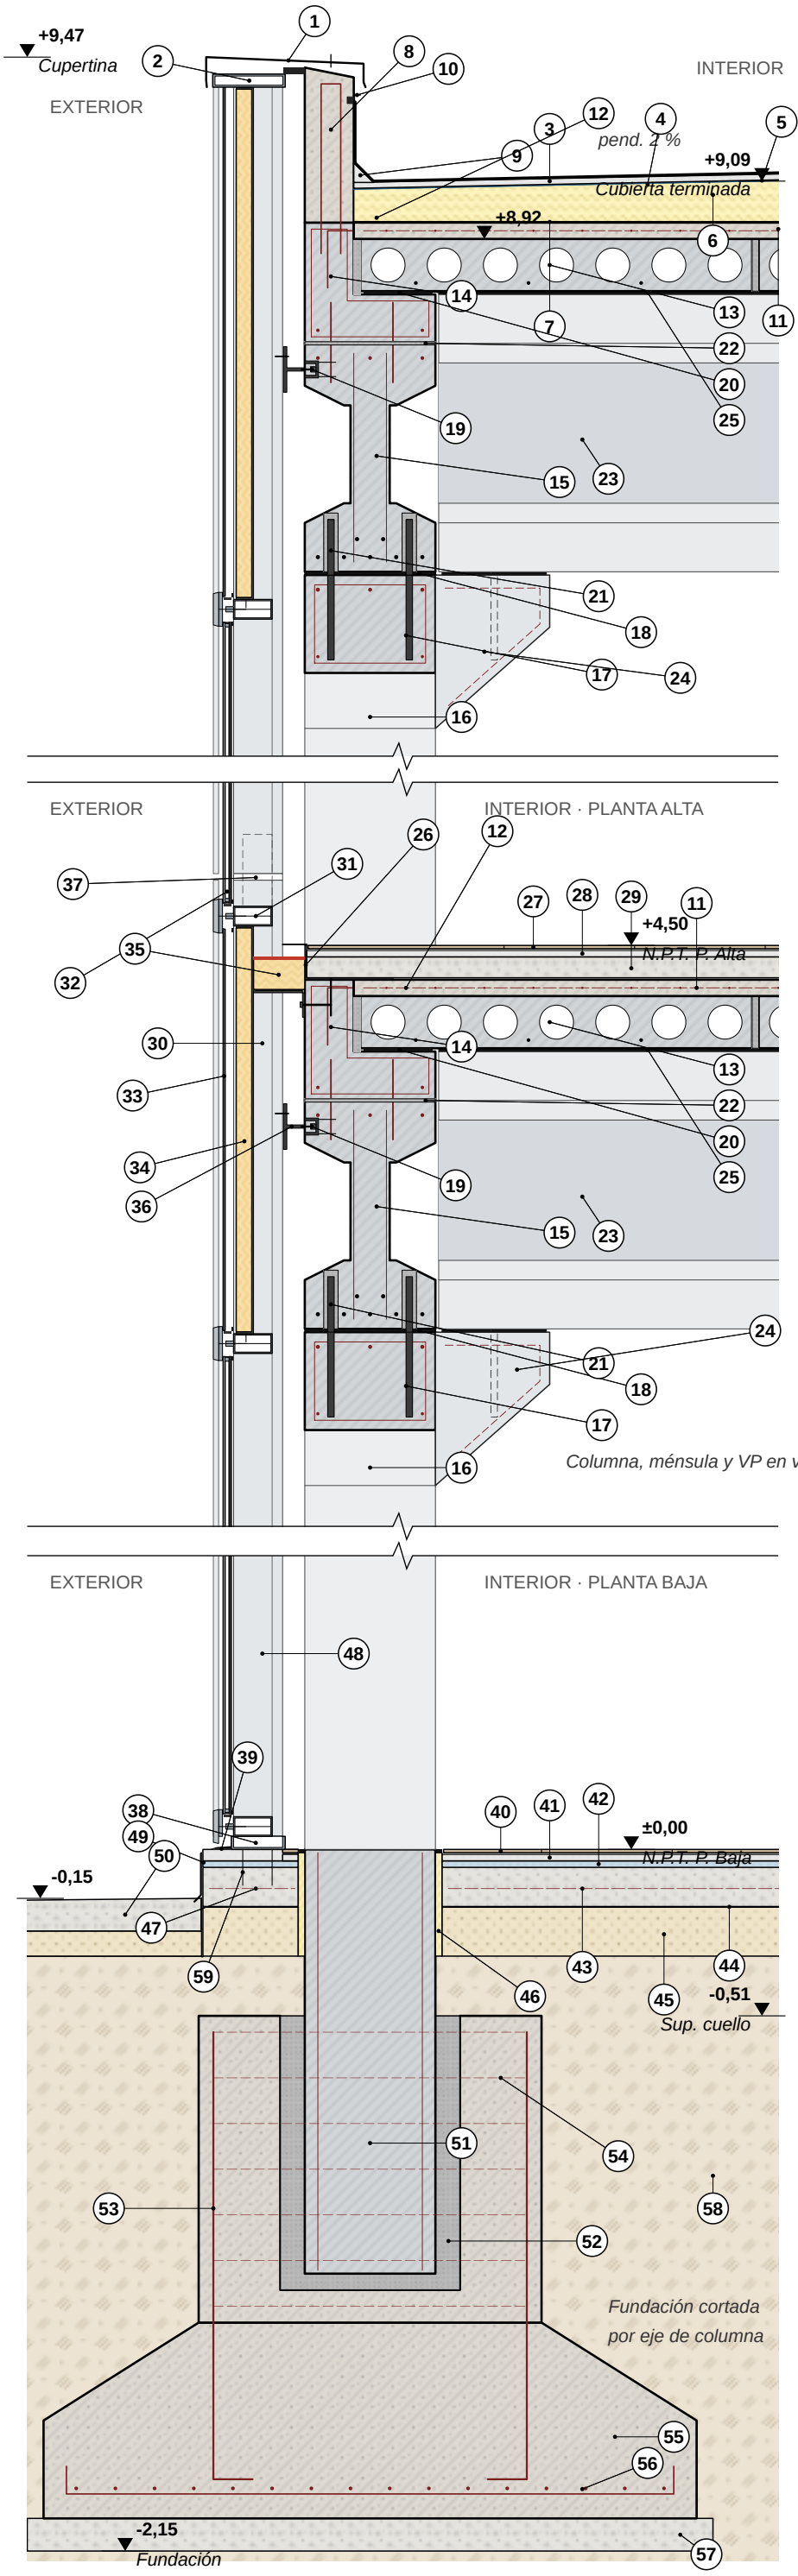


NUDO 1 · BORDE DE CUBIERTA
Isométrica esc. 1:10

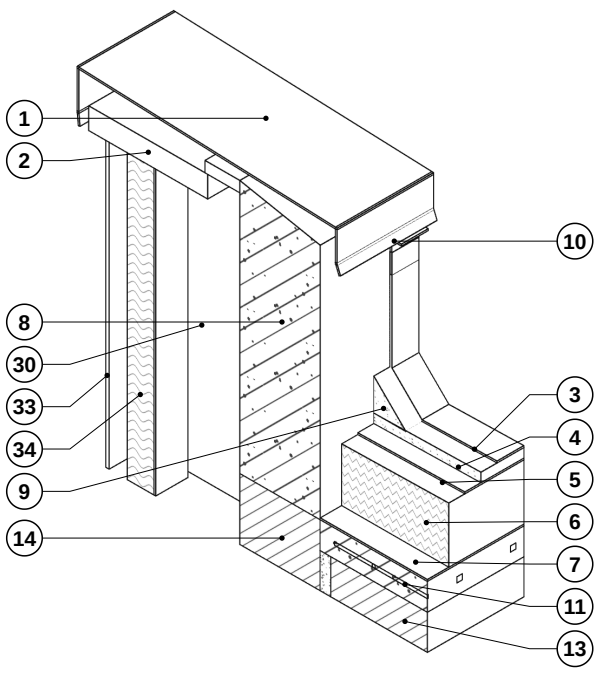

NUDO 3 · ARRANQUE MURO CORTINA
Isométrica esc. 1:10

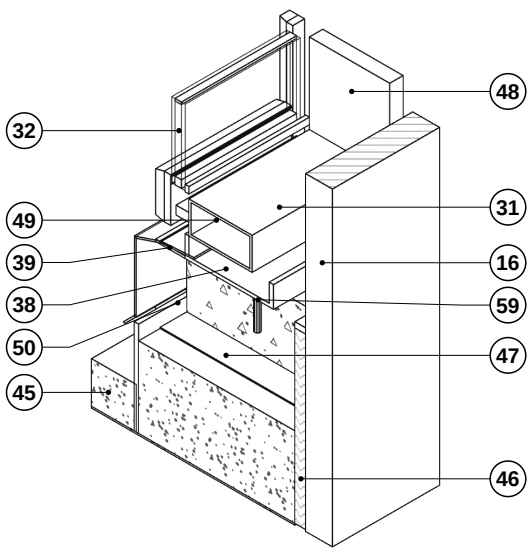

NUDO 2 · BORDE DE ENTREPISO
Isométrica esc. 1:10

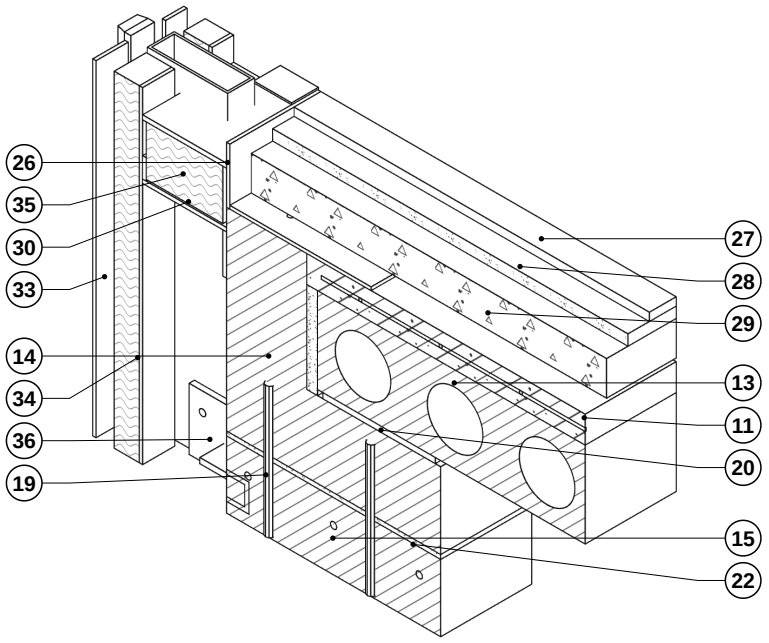

TP FINAL FECHA: 19/10/2026	DOCENTE: Arq. Tucci y Arq. Cardozo ALUMNA: Candelaria Vitale GRUPO: 13	NIVEL: OBS:	CONSTRUCCIONES II CATEDRA: ARQ. TUCCI