
INSTALACIÓN ELÉCTRICA — ESQUEMA UNIFILAR Y DE MONTANTES


EDIFICIO DE VIVIENDAS PB + 4 PISOS (1 DEPARTAMENTO POR PLANTA) · ASCENSOR · 3x380/220 V

1. ESQUEMA DE MONTANTES (CORTE ESQUEMÁTICO)

Distribución vertical: tableros, montantes y alimentaciones

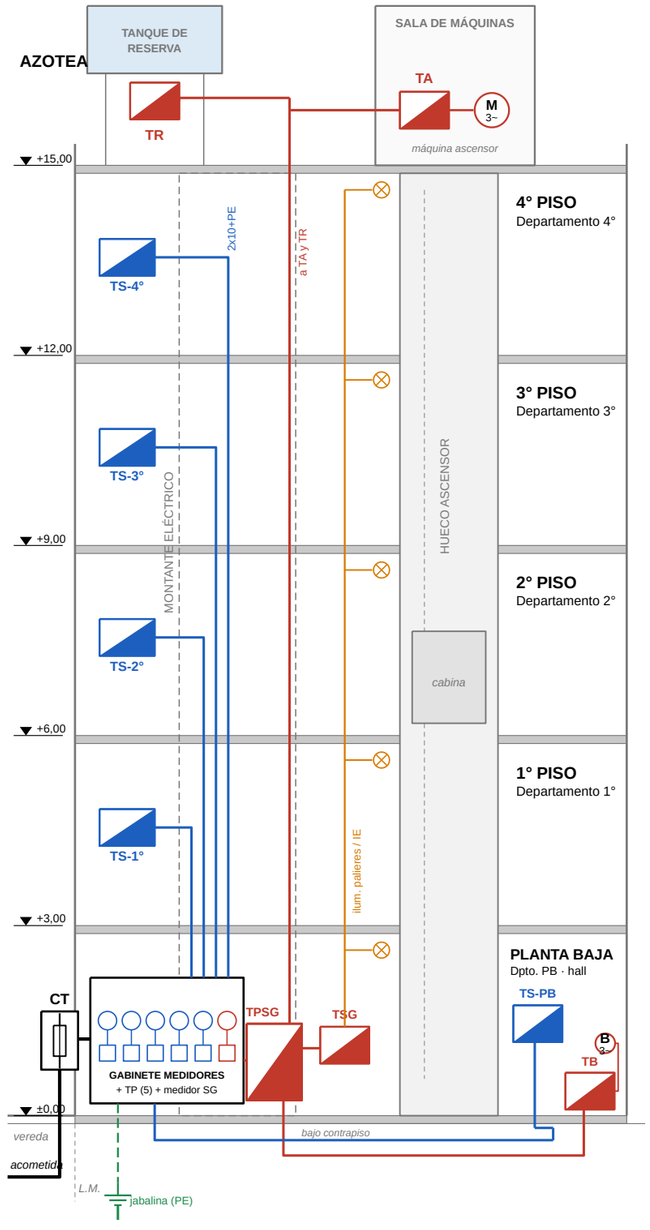

2. ESQUEMA UNIFILAR GENERAL — ACOMETIDA, MEDICIÓN, TP Y TPSG

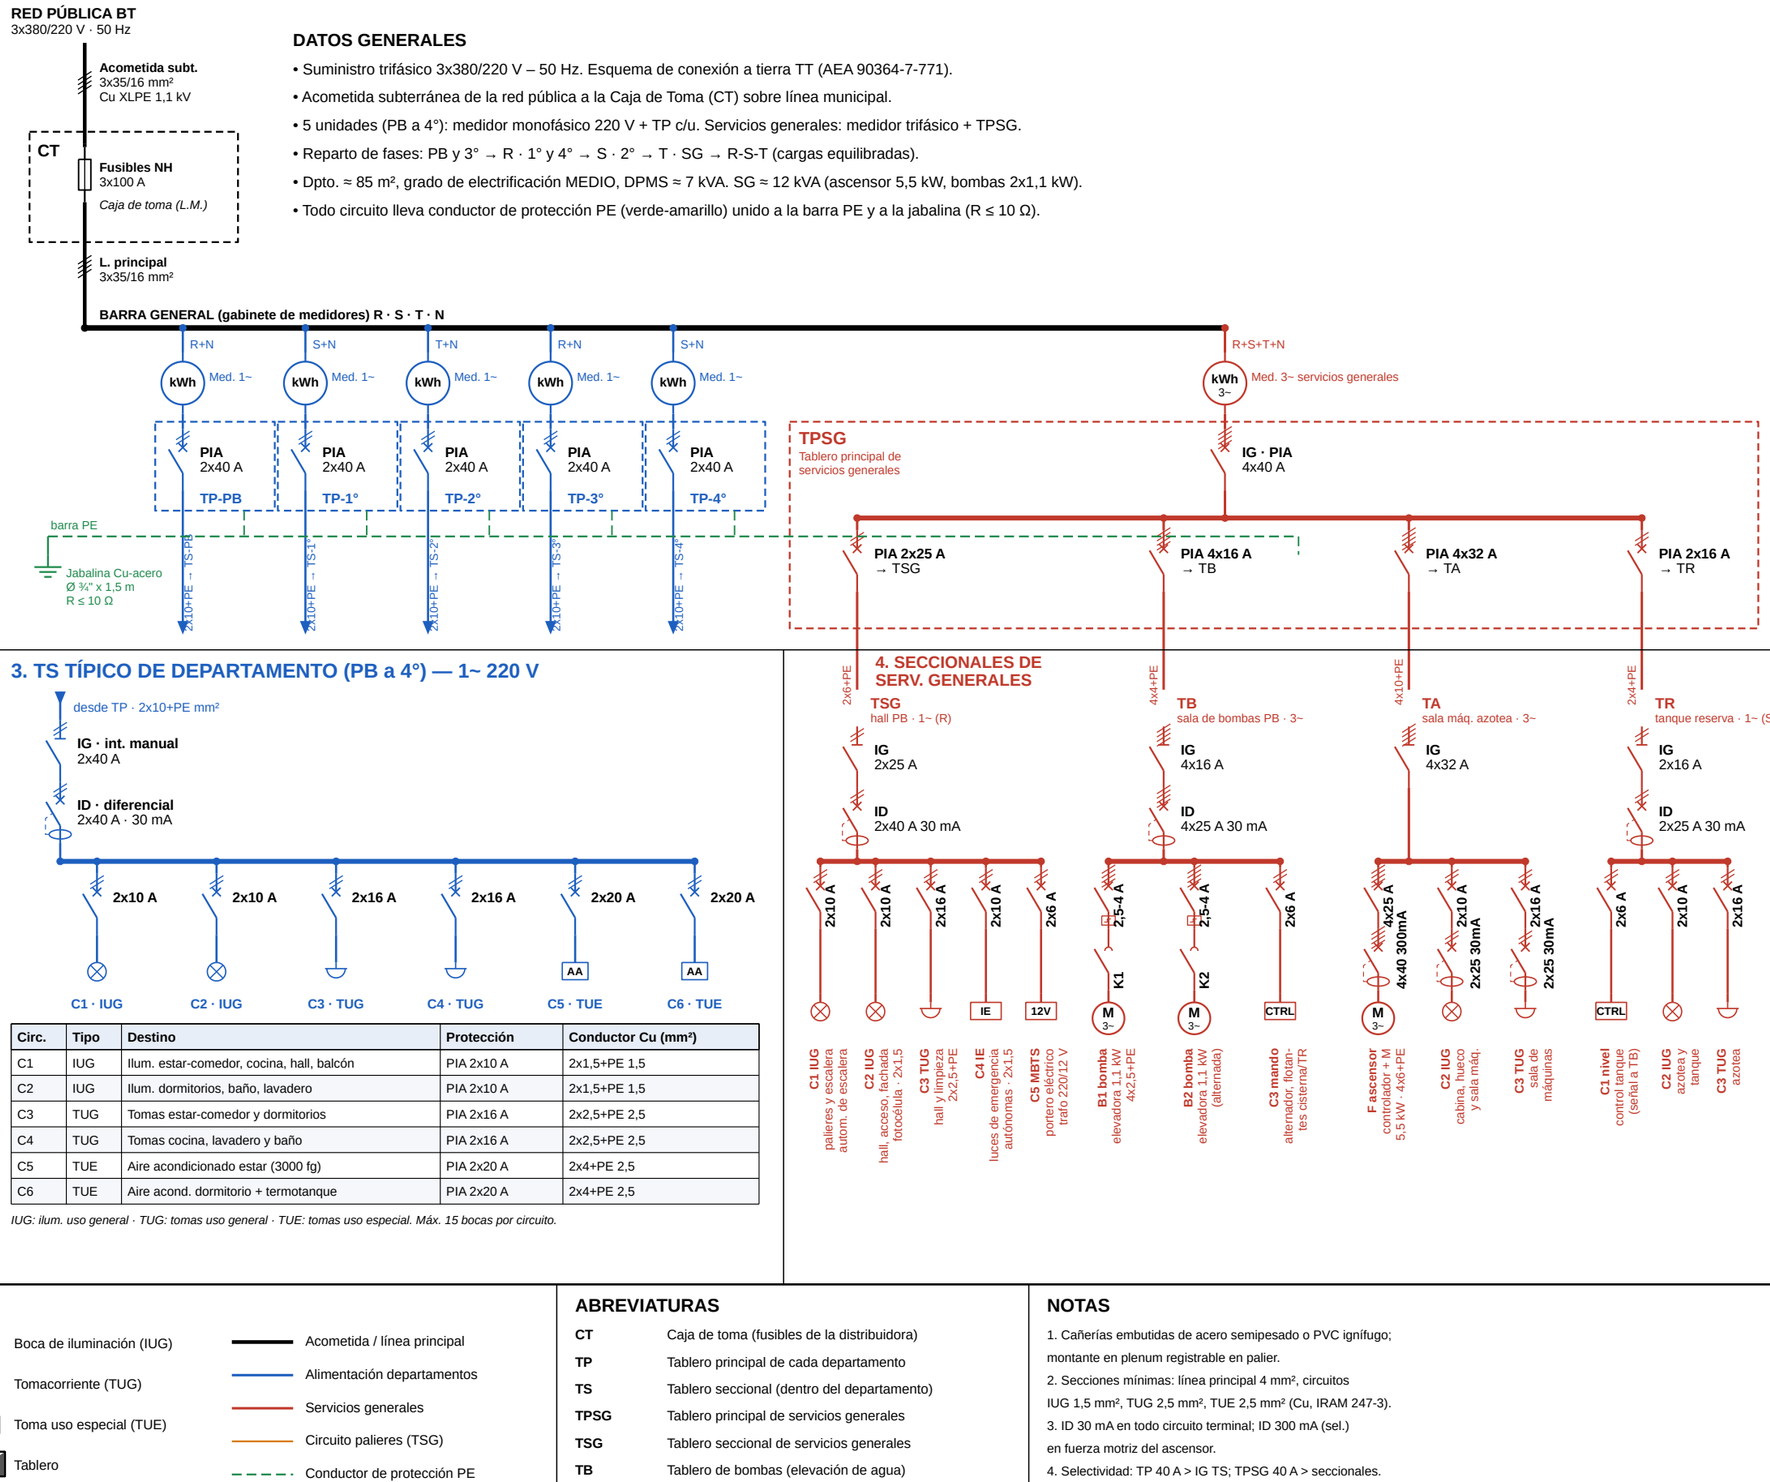

3. TS TÍPICO DE DEPARTAMENTO (PB a 4°) — 1~ 220 V

Circ.	Tipo	Destino	Protección	Conductor Cu (mm²)
C1	IUG	Ilum. estar-comedor, cocina, hall, balcón	PIA 2x10 A	2x1,5+PE 1,5
C2	IUG	Ilum. dormitorios, baño, lavadero	PIA 2x10 A	2x1,5+PE 1,5
C3	TUG	Tomas estar-comedor y dormitorios	PIA 2x16 A	2x2,5+PE 2,5
C4	TUG	Tomas cocina, lavadero y baño	PIA 2x16 A	2x2,5+PE 2,5
C5	TUE	Aire acondicionado estar (3000 fg)	PIA 2x20 A	2x4+PE 2,5
C6	TUE	Aire acond. dormitorio + termotanque	PIA 2x20 A	2x4+PE 2,5

IUG: ilum. uso general · TUG: tomas uso general · TUE: tomas uso especial. Máx. 15 bocas por circuito.

4. SECCIONALES DE SERV. GENERALES

REFERENCIAS — SÍMBOLOS

- Interruptor termomagnético (PIA)
- Interruptor diferencial (ID)
- Interruptor manual / seccionador
- Guardamotor (magnetotérmico)
- Contactor
- Fusible NH (caja de toma)
- Medidor de energía (kWh)
- Motor trifásico (bomba / ascensor)
- Boca de iluminación (IUG)
- Tomacorriente (TUG)
- Toma uso especial (TUE)
- Tablero
- Puesta a tierra / jabalina
- Acometida / línea principal
- Alimentación departamentos
- Servicios generales
- Circuito palieres (TSG)
- Conductor de protección PE
- Barra de tablero
- N° de polos (trazos)
- Límite de tablero

ABREVIATURAS

CT	Caja de toma (fusibles de la distribuidora)
TP	Tablero principal de cada departamento
TS	Tablero seccional (dentro del departamento)
TPSG	Tablero principal de servicios generales
TSG	Tablero seccional de servicios generales
TB	Tablero de bombas (elevación de agua)
TA	Tablero de ascensor (sala de máquinas)
TR	Tablero del tanque de reserva (azotea)
IG / ID	Interruptor general / diferencial
IE / MBTS	Ilum. emergencia / muy baja tensión
DPMS	Demanda de potencia máx. simultánea

NOTAS

1. Cañerías embutidas de acero semipesado o PVC ignífugo; montante en plenum registrable en palier.
2. Secciones mínimas: línea principal 4 mm², circuitos IUG 1,5 mm², TUG 2,5 mm², TUE 2,5 mm² (Cu, IRAM 247-3).
3. ID 30 mA en todo circuito terminal; ID 300 mA (sel.) en fuerza motriz del ascensor.
4. Selectividad: TP 40 A > IG TS; TPSG 40 A > seccionales.
5. Montante de SG alimenta TA y TR (azotea); TB y TSG en PB. El control de nivel del TR comanda las bombas.

INSTALACIONES — ELECTRICIDAD

Esquema unifilar · edificio PB + 4 pisos

Lámina: E-01 | Escala: S/E

Hoja: A3 apaisada | Fecha: 11/11/2026

Norma: AEA 90364-7-771