
CORTE INTEGRAL
MURO CORTINA

ESCALA 1:20


REFERENCIAS

1 Cupertina chapa galv. N°22 c/ goterones
2 Perfil de cierre sup. muro cortina + sellador
3 Membrana asfáltica 4 mm c/ aluminio + babeta
4 Carpeta 1:3 c/ 10 % hidrófugo, e = 2 cm
5 Contrapiso liviano H° c/ EPS (aislante), pend. 2 %
6 Babeta chapa galv. + sellador en buña
7 Barrera de vapor: imprimación + film 200 µ
8 Zócalo sup. H°A° in situ c/ barras a viga L
9 Media caña de mortero
10 Embudo c/ rejilla parabólica (en vista)
11 Capa de compresión 5 cm c/ malla Ø6 c/15
12 Estribos salientes viga L (2Ø10)
13 Panel TT h 0,65: ala y nervios cortados
14 Viga L de borde s/ VL (recibe el TT)
15 Viga VL doble T 40x70 pretensada
16 Columna pretensada 40x40 (en vista)
17 Ménsula de columna p/ VL (cortada)
18 Neopreno 10 mm: apoyo VL s/ ménsula
19 Riel de anclaje embutido + bulón T
20 Ala TT s/ talón viga L: neopreno + grout
21 2 pernos Ø20 en vainas c/ grout (antivuelco)
22 Junta VL / viga L: grout + barras Ø12
23 Viga VP T invertida (en vista)
24 Ménsula + neopreno + perno: apoyo VP (vista)
25 Nervio TT s/ talón VP + neopreno
26 Solado cerámico s/ adhesivo cementicio
27 Carpeta niveladora MHR 1:1/4:3, e = 2 cm
28 Cielorraso placa de roca de yeso 12,5 mm
29 Montantes y soleras chapa galv. 35 mm
30 Gancho / vela a los nervios del panel TT
31 Mullion: montante alum. 50x150
32 Travesaño + presor + tapa + burletes EPDM
33 DVH 6 templado + 12 + 3+3 laminado PVB
34 Spandrel: vidrio templado 6 mm esmaltado
35 Lana 50 mm en bandeja galv. atornillada
36 Cortafuego: lana + sellador s/ ángulo galv.
37 Grapa acero galv. regulable + bulón M12 inox
38 Junta de dilatación 20 mm + manguito
39 Perfil guía de arranque (deslizante)
40 Sellador silicona neutra s/ fondo de junta
41 Solado cerámico s/ adhesivo cementicio
42 Carpeta niveladora MHR 1:1/4:3
43 Carpeta hidrófuga MCI 1:3
44 Contrapiso de H° pobre, e = 12 cm
45 Film de polietileno 200 µ
46 Tosca compactada, e = 15 cm
47 Junta de dilatación EPS 2 cm + sellador
48 Contrapiso armado hasta la fachada
49 Montante colgado del entrepiso
50 Babeta chapa galv. + aislación hidrófuga
51 Vereda de H° peinado s/ tosca
52 Tronco de columna dentro del cuello
53 Anclaje mecánico húmedo (horquillas)
54 Relleno de H° cementicio cuello/columna
55 Armadura de vinculación fundación–columna
56 Cuello de la base, H°A° in situ
57 Base de H°A° colada in situ (s/ cálculo)
58 Armadura de fundación s/ cálculo
59 H° de limpieza, e = 10 cm
60 Terreno natural
61 Broca c/ prisionero Ø9,5 x 80 + tuerca


NUDO 1 · CUBIERTA
Isométrica esc. 1:20

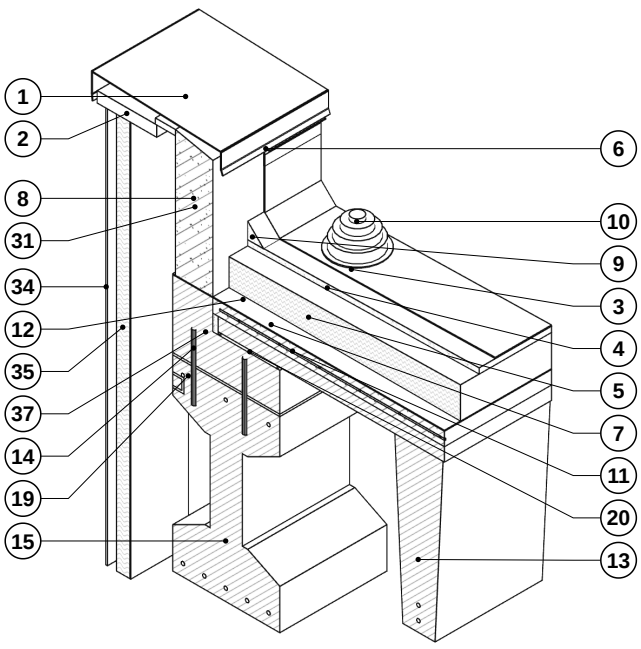


NUDO 2 · ENTREPISO
Isométrica esc. 1:20

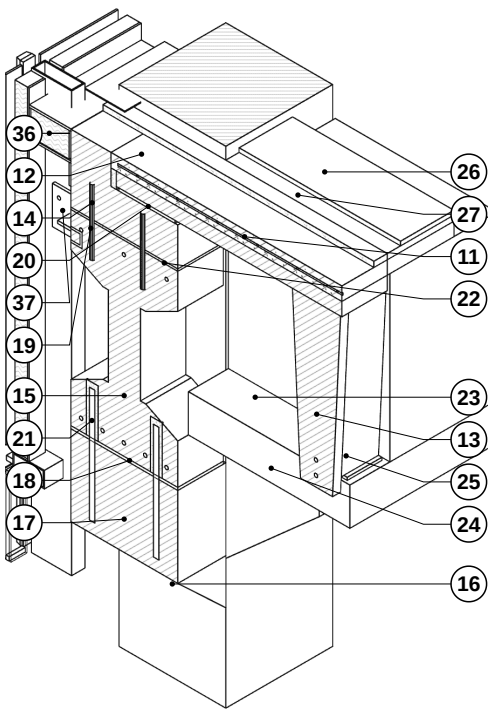

NUDO 3 · PISO
Isométrica esc. 1:15

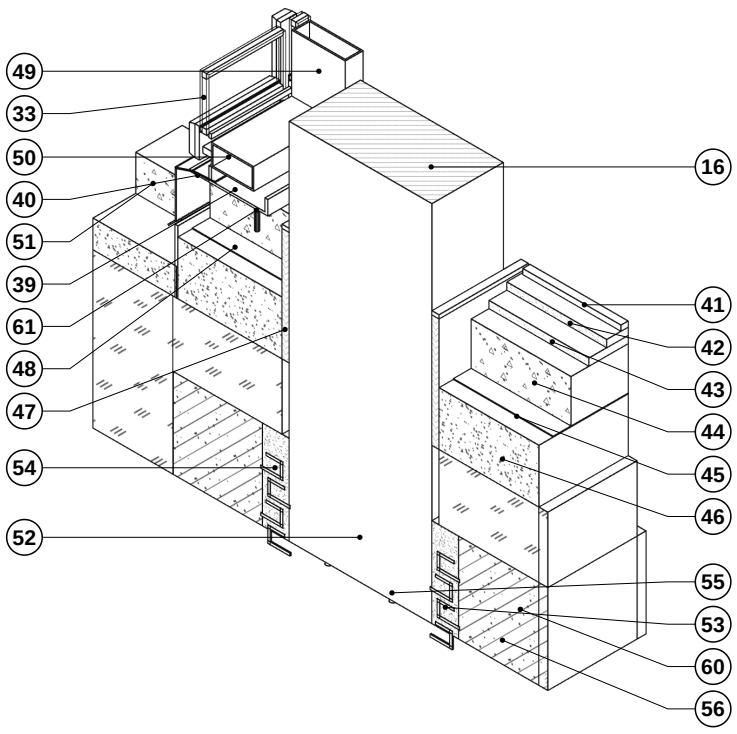

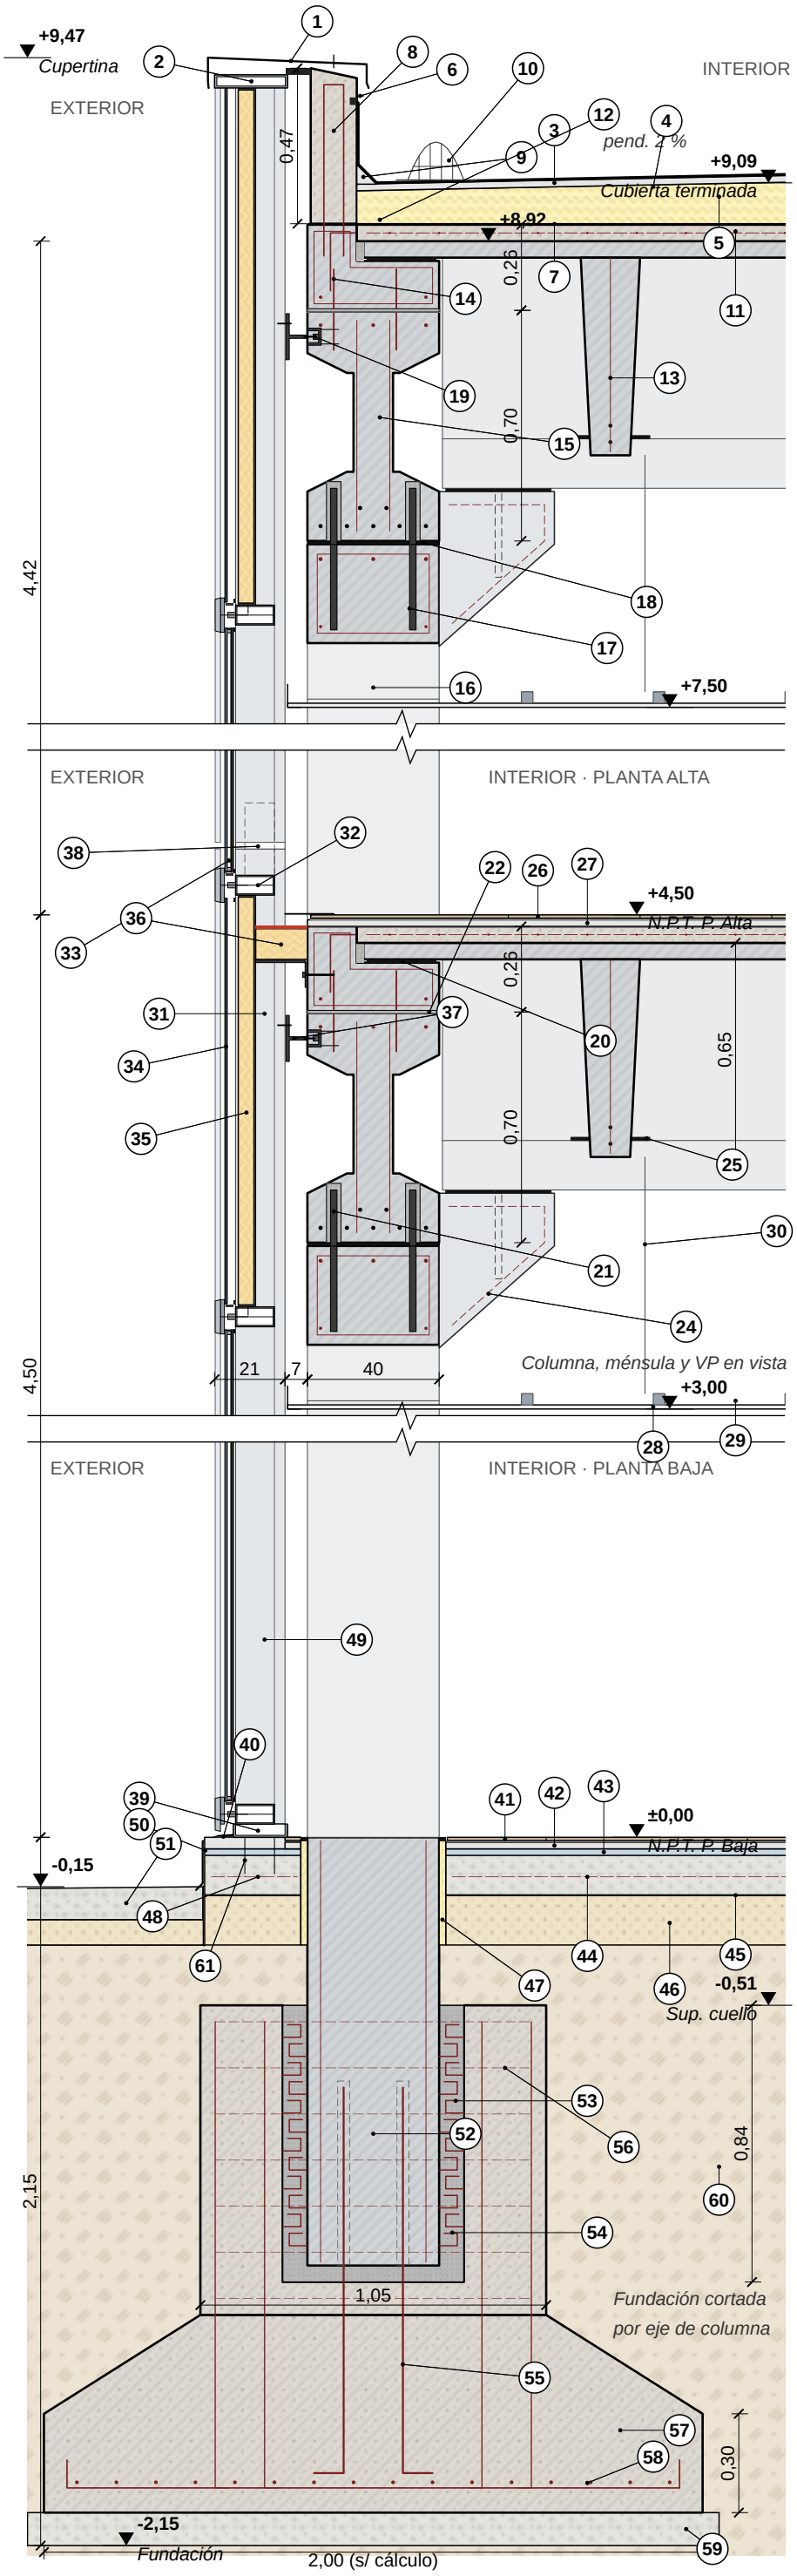

TP FINAL FECHA: 19/10/2026	DOCENTE: Arq. Tucci y Arq. Cardozo ALUMNA: Candelaria Vitale GRUPO: 13	NIVEL: OBS:	CONSTRUCCIONES II CATEDRA: ARQ. TUCCI