
1º ELEMENTOS DEL SISTEMA · AXONOMETRÍA

Isométrica 1:250 · módulo 10,00 x 15,00 m · sin parte de la cubierta y sin vidrios para mostrar el armado

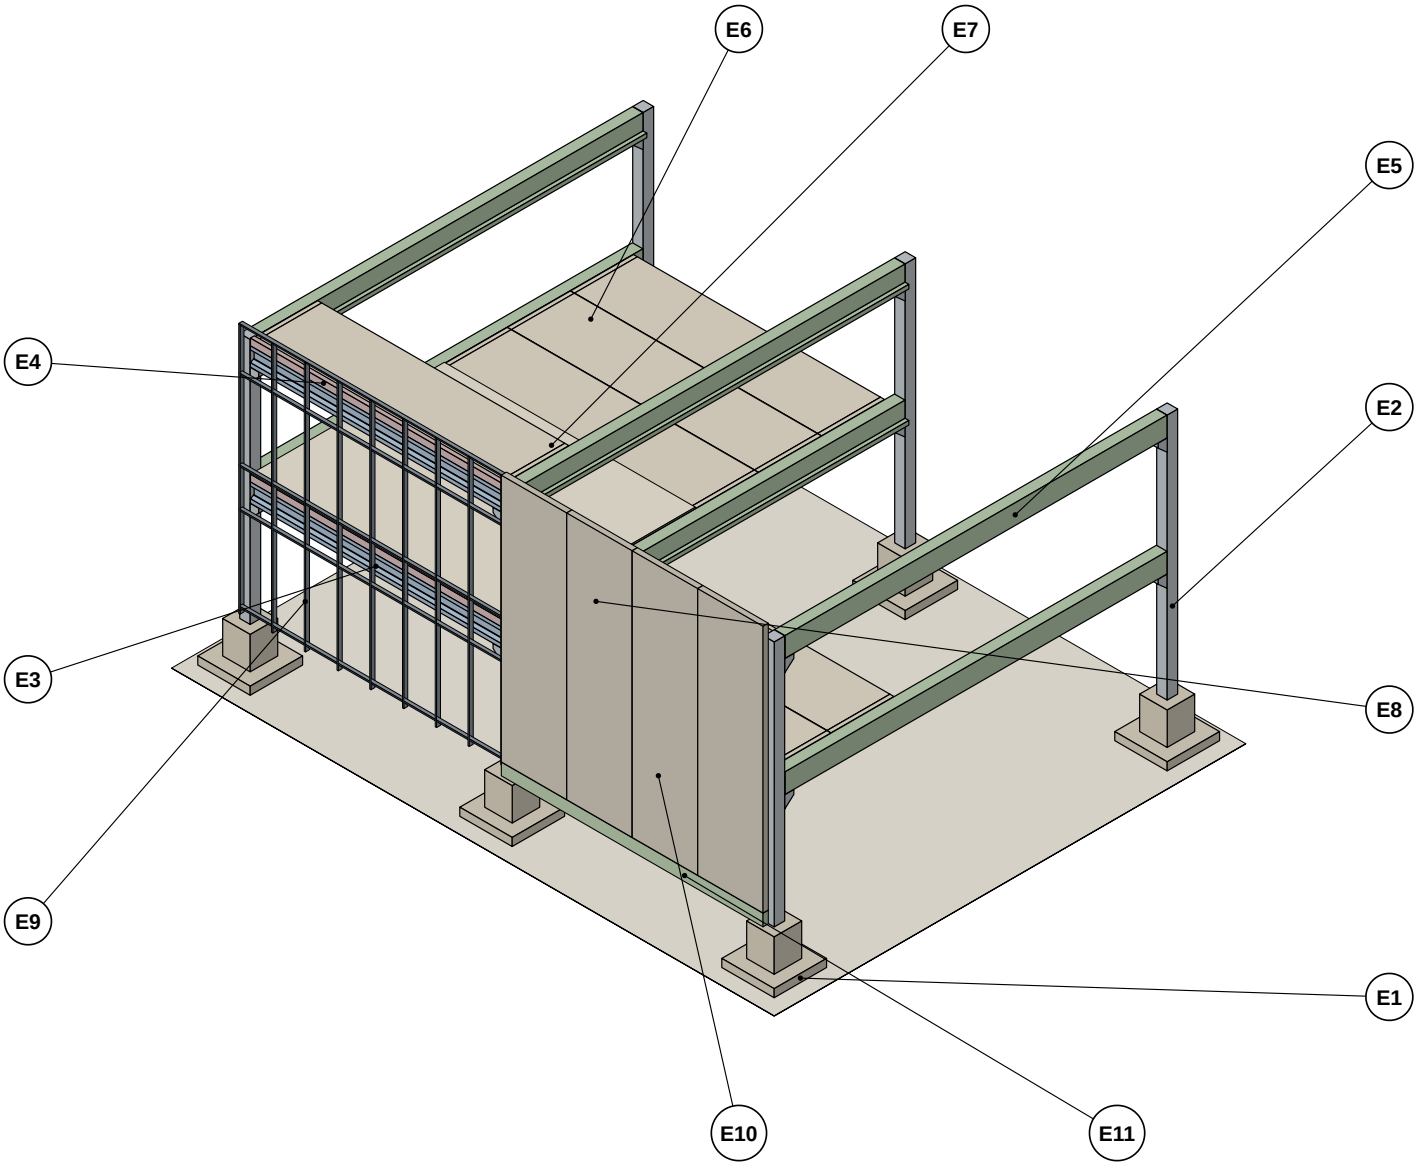

REFERENCIAS · ELEMENTOS DEL SISTEMA

- **E1** Fundación tipo cáliz (base + cuello H°A° in situ)
- **E2** Columna premoldeada pretensada 40x40 c/ ménsulas cortas
- **E3** Viga VL doble T 40x70 pretensada (fachada)
- **E4** Viga L de borde premoldeada (s/ VL, recibe el TT)
- **E5** Viga VP T invertida h 0,75 (portante principal, luz 15 m)
- **E6** Panel TT h 0,65 x 2,40 (entrepiso y cubierta, luz 10 m)
- **E7** Capa de compresión H°A° in situ e = 5 cm c/ malla
- **E8** Apoyos y conectores: neopreno, pernos, grout, riel
- **E9** Muro cortina stick (cerramiento vidriado)
- **E10** Panel sándwich premoldeado e = 20 cm (opaco)
- **E11** Viga portapanel pretensada 20x85 (arranque del panel)

PARA ESTUDIAR · IDEAS CLAVE

- El sistema se arma como un mecano: piezas fabricadas en planta (columnas, vigas, paneles) que en obra sólo se apoyan y se vinculan.
- Recorrido de cargas: panel TT → viga VP (o viga L) → ménsula → columna → cáliz → suelo.
- Las vigas apoyan ARTICULADAS (neopreno); la estabilidad la dan las columnas EMPOTRADAS en el cáliz y la capa de compresión, que convierte el piso en un diafragma rígido.
- Los cerramientos (muro cortina y panel sándwich) no son estructura: cuelgan de la viga perimetral VL.