
4º CERRAMIENTOS · E10 PANEL SÁNDWICH PREMOLDEADO

Panel de H°A° con aislación incorporada, colgado de la VL con bulones (fija panel) y apoyado en la viga portapanel


ALZADO (2 paneles)

Vista exterior 1:100

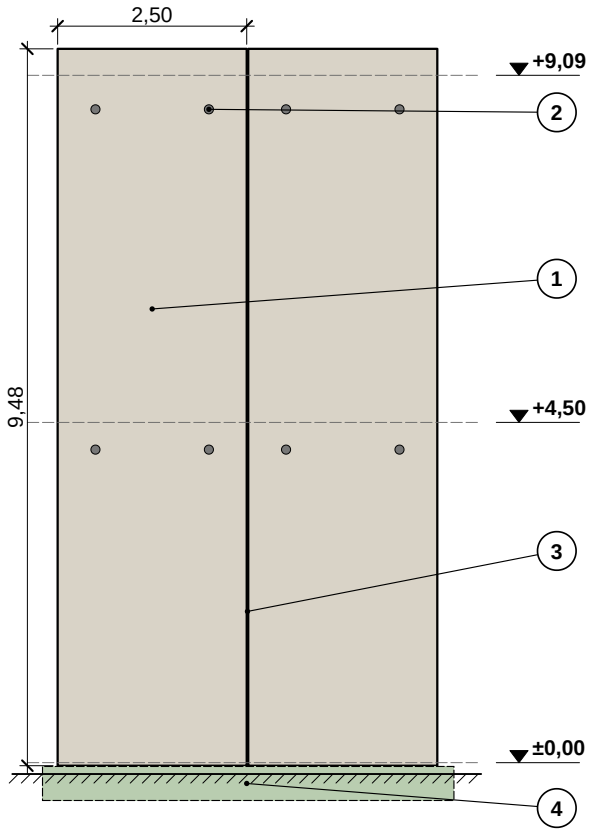

CORTE


esc. 1:100

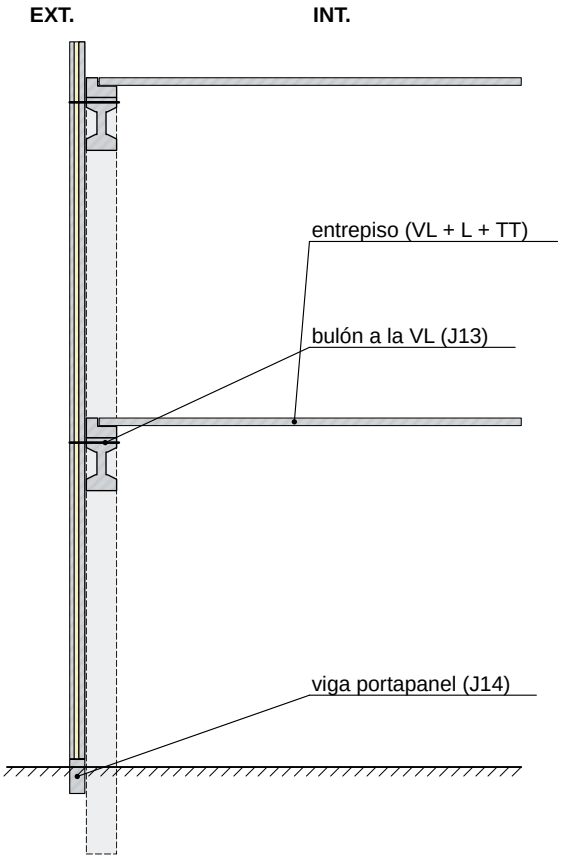

1. Panel sándwich 2,50 x 9,48 x 0,20 m (≈ 8,3 t)
2. Fija panel: bulón M20 (rehundido tapado)
3. Junta vertical 20 mm (J15)
4. Viga portapanel E11 (bajo el nivel de piso)

SECCIÓN HORIZONTAL DEL PANEL

esc. 1:20 · zona de anclaje maciza y junta entre paneles (se muestra 1 panel y la junta)

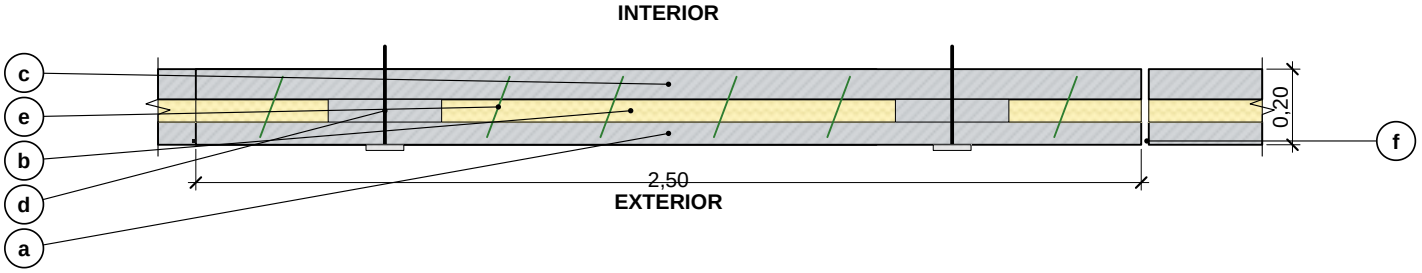

- a Hoja exterior H°A° 6 cm (texturada)
- b Alma EPS 6 cm (20 kg/m³)
- c Hoja interior PORTANTE H°A° 8 cm
- d Zona maciza 30x30 en cada anclaje
- e Conectores de fibra de vidrio
- f Junta 20 mm: cordón + sellador PU