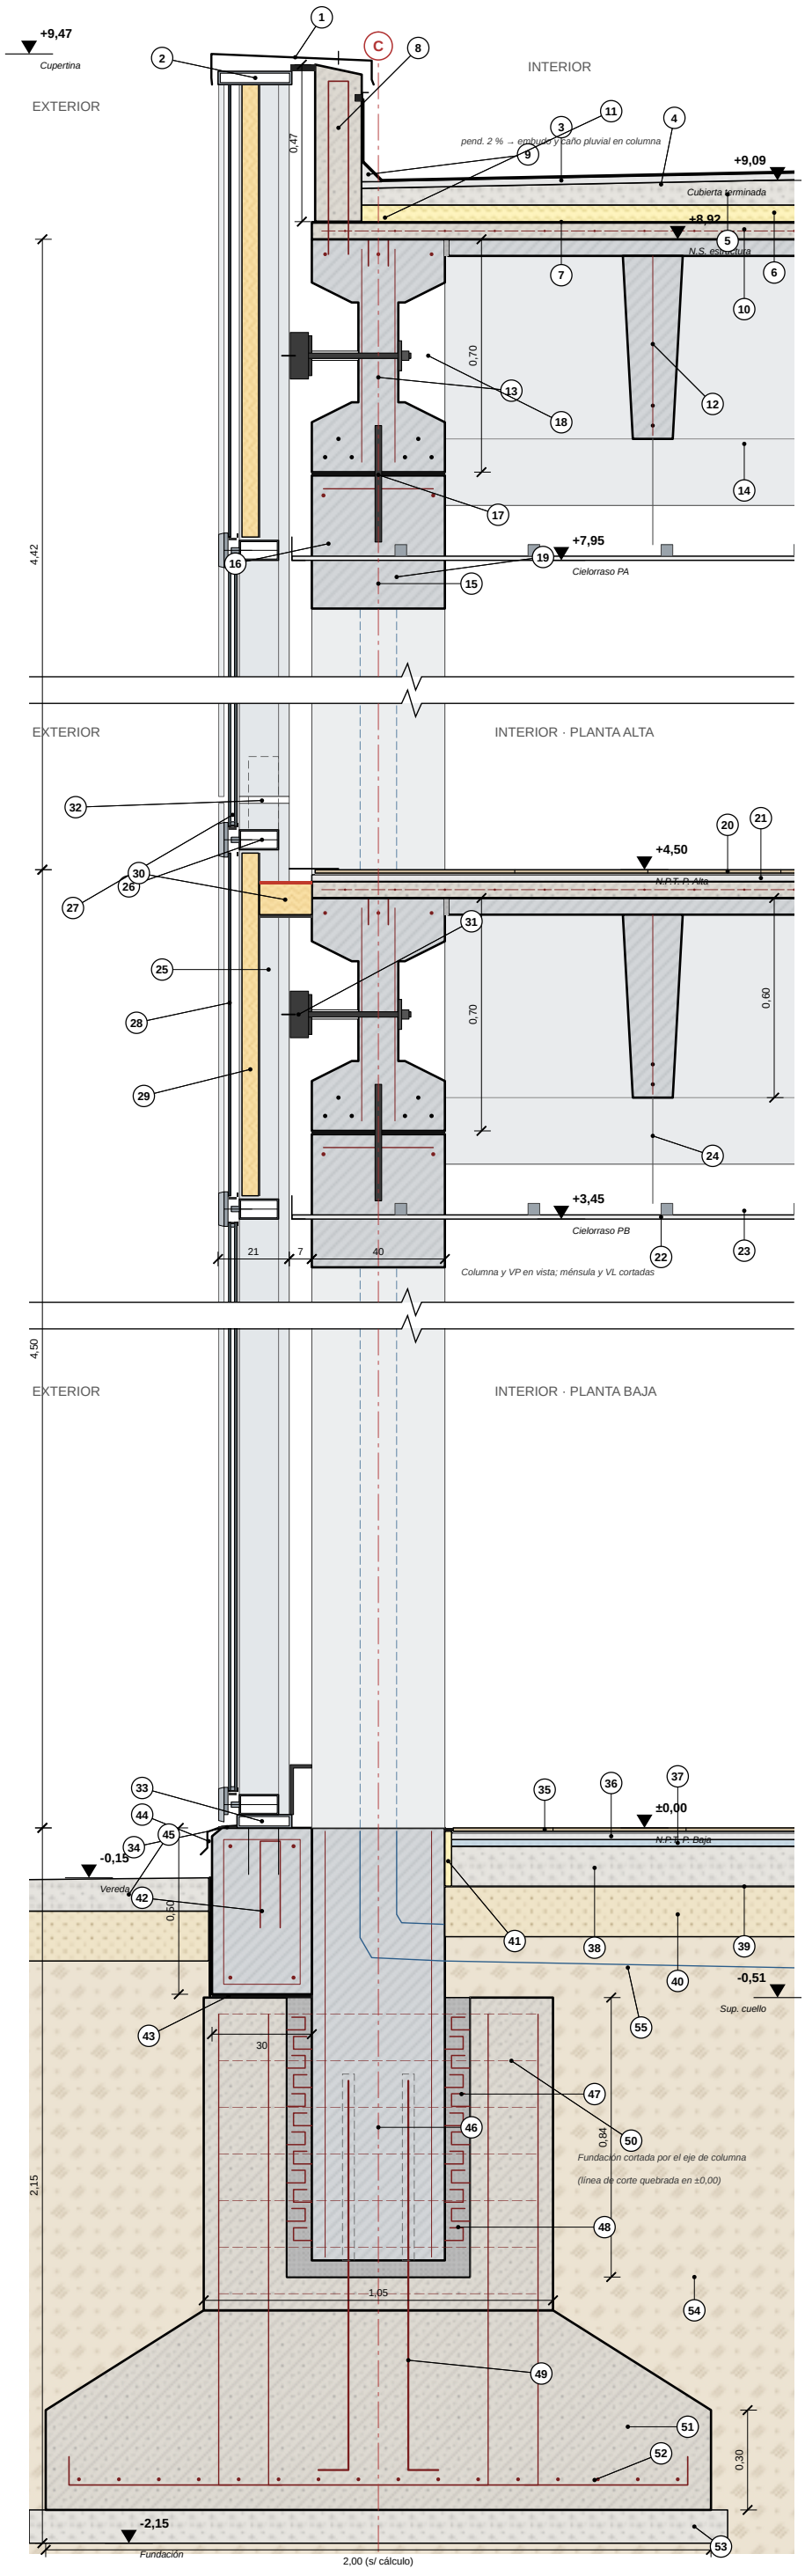


ESC. 1:20 — corte por apoyo de VL / ménsula; fundación por eje de columna (corte quebrado en ±0,00)

0 50 cm

REFERENCIAS (corte integral y nudos)

CUBIERTA

1 Cupertina chapa galv. N°22 plegada c/ goterones, tornillos y sellador.
2 Perfil de cierre superior del muro cortina + sellador de silicona.
3 Membrana asfáltica 4 mm c/ aluminio; babeta en buña + perfil + sellador.
4 Carpeta niveladora 1:3 c/ 10 % de hidrófugo, e = 2 cm.
5 Contrapiso liviano H° c/ EPS 1:6, pend. 2 % (mín. 5 cm).
6 Aislación térmica EPS 30 kg/m³, e = 5 cm (IRAM 11605).
7 Barrera de vapor: imprimación asfáltica + film 200 µ.
8 Zócalo superior H°A° in situ c/ barras de atado a la VL.
9 Media caña de mortero.

ESTRUCTURA PREMOLDEADA (SISTEMA PI)

10 Capa de compresión H° e = 5 cm c/ malla electrosoldada Ø6 c/15.
11 Estribos salientes de la VL (2Ø10) p/ vinculación c/ capa de compresión.
12 Panel TT pretensado (corte transversal), apoyado en VP.
13 Viga pretensada VL 40x70 (doble T), perimetral.
14 Viga pretensada VP (en vista), apoyo de paneles TT.
15 Columna pretensada 40x40 c/ caño pluvial (en vista).
16 Ménsula de columna p/ apoyo de viga.
17 Apoyo de neopreno c/ perno de fijación Ø20.
18 Bulón pasante Ø3/4" c/ tuerca y arandela Ø90 + sellado c/ masilla (anclaje).
19 Caño de desagüe pluvial PVC Ø110 embutido en la columna.

ENTREPISO Y CIELORRASOS

20 Solado cerámico s/ adhesivo cementicio.
21 Carpeta niveladora MHR 1:1/4:3, e = 2 cm.
22 Cielorraso suspendido placa de roca de yeso 12,5 mm.
23 Montantes y soleras de chapa galv. 35 mm.
24 Gancho / vela de fijación a los nervios del panel TT.

MURO CORTINA (STICK, MÓDULO 1,25 m)


25 Montante de aluminio 50x150 (en vista).
26 Travesaño de aluminio + presor + tapa + burletes EPDM.
27 DVH: 6 templado + cámara 12 + 3+3 laminado PVB.
28 Spandrel: vidrio templado 6 mm esmaltado.
29 Lana mineral 50 mm + bandeja de chapa galv.
30 Barrera cortafuego: lana mineral 100 kg/m³ + sellador intumescente.
31 Grapa de acero galv. regulable (colisos) + bulón M12 inox.
32 Junta de dilatación del montante 20 mm + manguito.
33 Perfil de arranque alum. c/ drenaje + tarugos a la VPP.
34 Sellador de silicona neutra s/ fondo de junta.

PLANTA BAJA Y FUNDACIÓN

35 Solado cerámico s/ adhesivo cementicio.
36 Carpeta niveladora MHR 1:1/4:3.
37 Carpeta hidrófuga MCI 1:3 c/ aditivo hidrófugo.
38 Contrapiso de H° pobre e = 12 cm.
39 Separador de suelos: film de polietileno 200 µ.
40 Tosca compactada e = 15 cm.
41 Junta de dilatación perimetral EPS 2 cm + sellador.
42 Viga perimetral portamuro (VPP) premoldeada 30x50.
43 Banda de neopreno s/ cuello p/ apoyo de la VPP.
44 Babeta/goterón chapa galv. + aislación hidrófuga vertical.
45 Vereda de H° peinado s/ tosca + junta c/ sellador.
46 Tronco de columna dentro del cuello.
47 Anclaje mecánico húmedo: horquillas entrelazadas columna/cuello.
48 Relleno de H° cementicio entre cuello y columna.
49 Armadura de vinculación fundación–columna.
50 Cuello de la base, H°A° colado in situ.
51 Base de H°A° colada in situ (s/ cálculo).
52 Armadura de fundación s/ cálculo estructural.
53 H° de limpieza (hidráulico pobre) e = 10 cm.
54 Terreno natural.
55 Caño pluvial PVC Ø110 a cámara de inspección y colectora.


NUDO 1 · CUBIERTA

Isométrica esc. 1:12,5 (ajustada de 1:10) · VL + TT + cubierta + zócalo in situ + cupertina

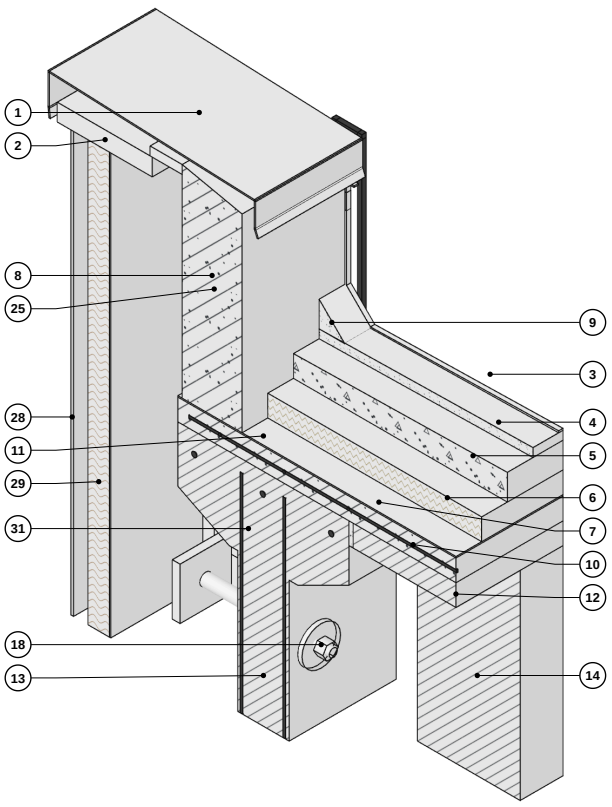


NUDO 2 · ENTREPISO

Isométrica esc. 1:12,5 (ajustada de 1:10) · Ménsula + perno + VL + bulón pasante + spandrel

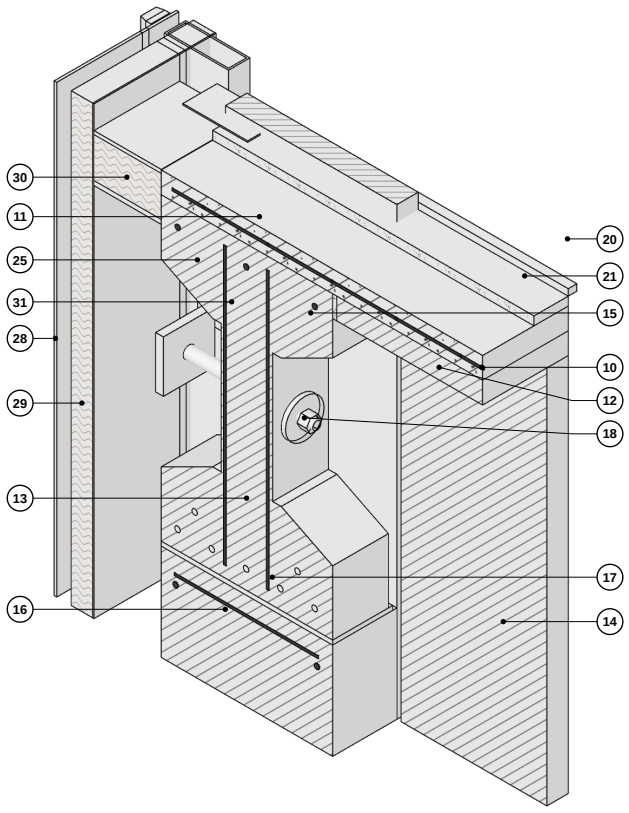

NUDO 3 · CERRAMIENTO Y PISO S/ TERRENO

Isométrica esc. 1:10 · Cuello + anclaje mecánico húmedo + VPP + arranque del muro cortina + piso

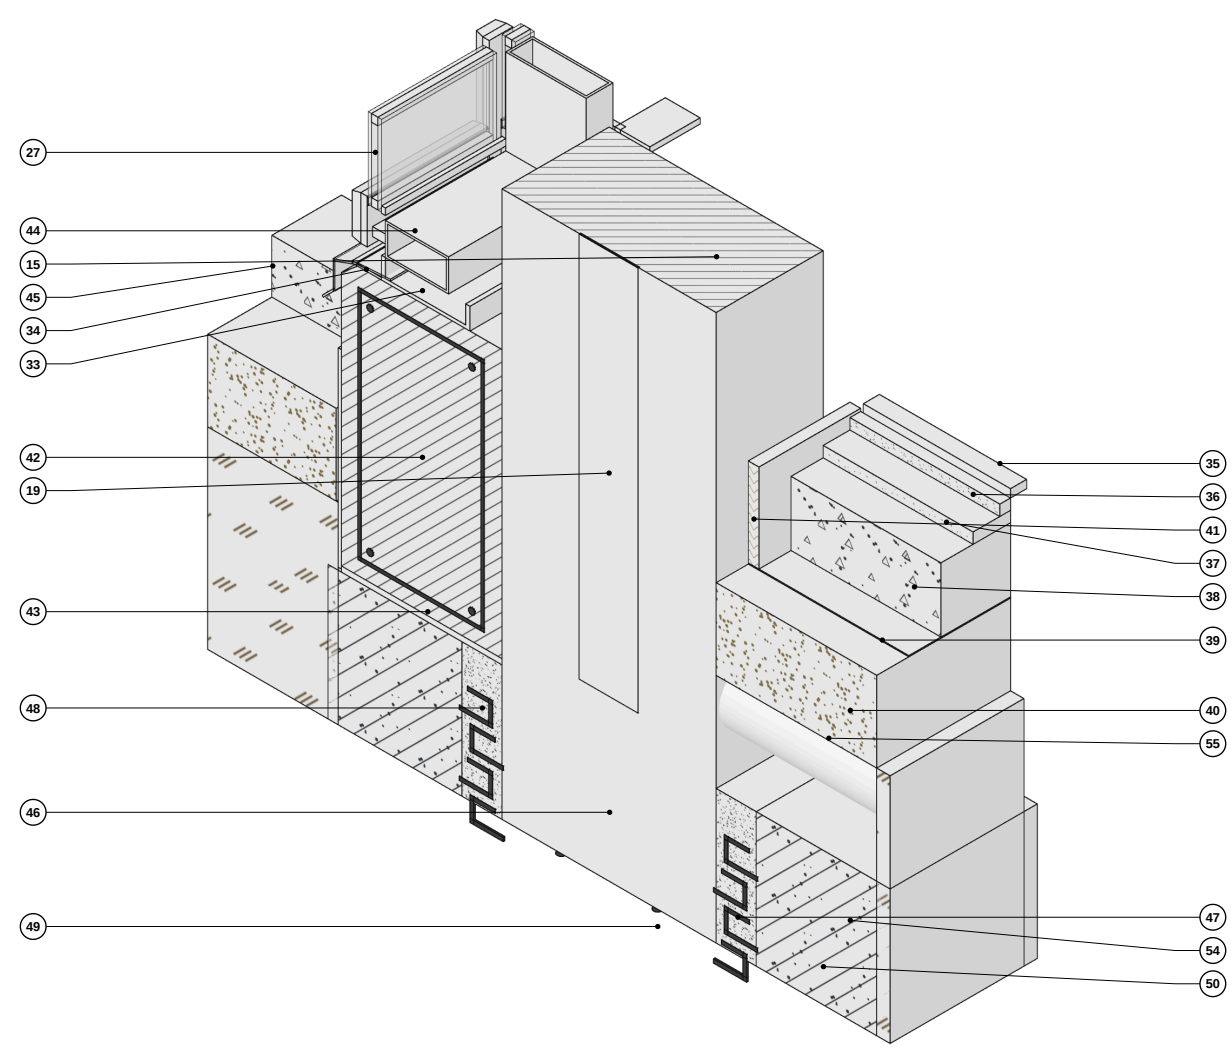

CORTE INTEGRAL 1:20 + NUDOS AXONOMÉTRICOS — VIDRIADO

Hormigón premoldeado de grandes luces (sistema Pi) · cerramiento vidriado – muro cortina

MATERIA	Construcciones II	**CÁTEDRA**	Arq. Tucci	**ALUMNO/A**	_____
GRUPO	____	**ESCALAS**	Corte 1:20 · Nudos 1:12,5	**HOJA**	A3 · 2026