
CORTE INTEGRAL
MURO CORTINA


ESCALA 1:20

REFERENCIAS


1 Cupertina chapa galv. N°22 c/ goterones
2 Perfil de cierre sup. muro cortina + sellador
3 Membrana asfáltica 4 mm c/ aluminio + babeta
4 Carpeta 1:3 c/ 10 % hidrófugo, e = 2 cm
5 Contrapiso liviano H° c/ EPS (aislante), pend. 2 %
6 Babeta chapa galv. + sellador en buña
7 Barrera de vapor: imprimación + film 200 µ
8 Zócalo sup. H°A° in situ c/ barras a viga L
9 Media caña de mortero
10 Capa de compresión 5 cm c/ malla Ø6 c/15
11 Estribos salientes viga L (2Ø10)
12 Panel TT h 0,65: ala y nervios cortados
13 Viga L de borde s/ VL (recibe el TT)
14 Viga VL doble T 40x70 pretensada
15 Columna pretensada 40x40 (en vista)
16 Ménsula de columna p/ VL (cortada)
17 Neopreno 10 mm: apoyo VL s/ ménsula
18 Riel de anclaje embutido + bulón T
19 Ala TT s/ talón viga L: neopreno + grout
20 Perno Ø20 en vaina rellena c/ grout
21 Junta VL / viga L: grout + barras Ø12
22 Viga VP T invertida (en vista)
23 Ménsula + neopreno + perno: apoyo VP (vista)
24 Nervio TT s/ talón VP + neopreno
25 Solado cerámico s/ adhesivo cementicio
26 Carpeta niveladora MHR 1:1/4:3, e = 2 cm
27 Cielorraso placa de roca de yeso 12,5 mm
28 Montantes y soleras chapa galv. 35 mm
29 Gancho / vela a los nervios del panel TT
30 Mullion: montante alum. 50x150
31 Travesaño + presor + tapa + burletes EPDM
32 DVH 6 templado + 12 + 3+3 laminado PVB
33 Spandrel: vidrio templado 6 mm esmaltado
34 Lana mineral 50 mm + bandeja chapa galv.
35 Barrera cortafuego lana mineral + intumescente
36 Grapa acero galv. regulable + bulón M12 inox
37 Junta de dilatación 20 mm + manguito
38 Perfil guía de arranque (deslizante)
39 Sellador silicona neutra s/ fondo de junta
40 Solado cerámico s/ adhesivo cementicio
41 Carpeta niveladora MHR 1:1/4:3
42 Carpeta hidrófuga MCI 1:3
43 Contrapiso de H° pobre, e = 12 cm
44 Film de polietileno 200 µ
45 Tosca compactada, e = 15 cm
46 Junta de dilatación EPS 2 cm + sellador
47 Contrapiso armado hasta la fachada
48 Montante colgado del entrepiso
49 Babeta chapa galv. + aislación hidrófuga
50 Vereda de H° peinado s/ tosca
51 Tronco de columna dentro del cuello
52 Anclaje mecánico húmedo (horquillas)
53 Relleno de H° cementicio cuello/columna
54 Armadura de vinculación fundación–columna
55 Cuello de la base, H°A° in situ
56 Base de H°A° colada in situ (s/ cálculo)
57 Armadura de fundación s/ cálculo
58 H° de limpieza, e = 10 cm
59 Terreno natural
60 Broca c/ prisionero Ø9,5 x 80 + tuerca

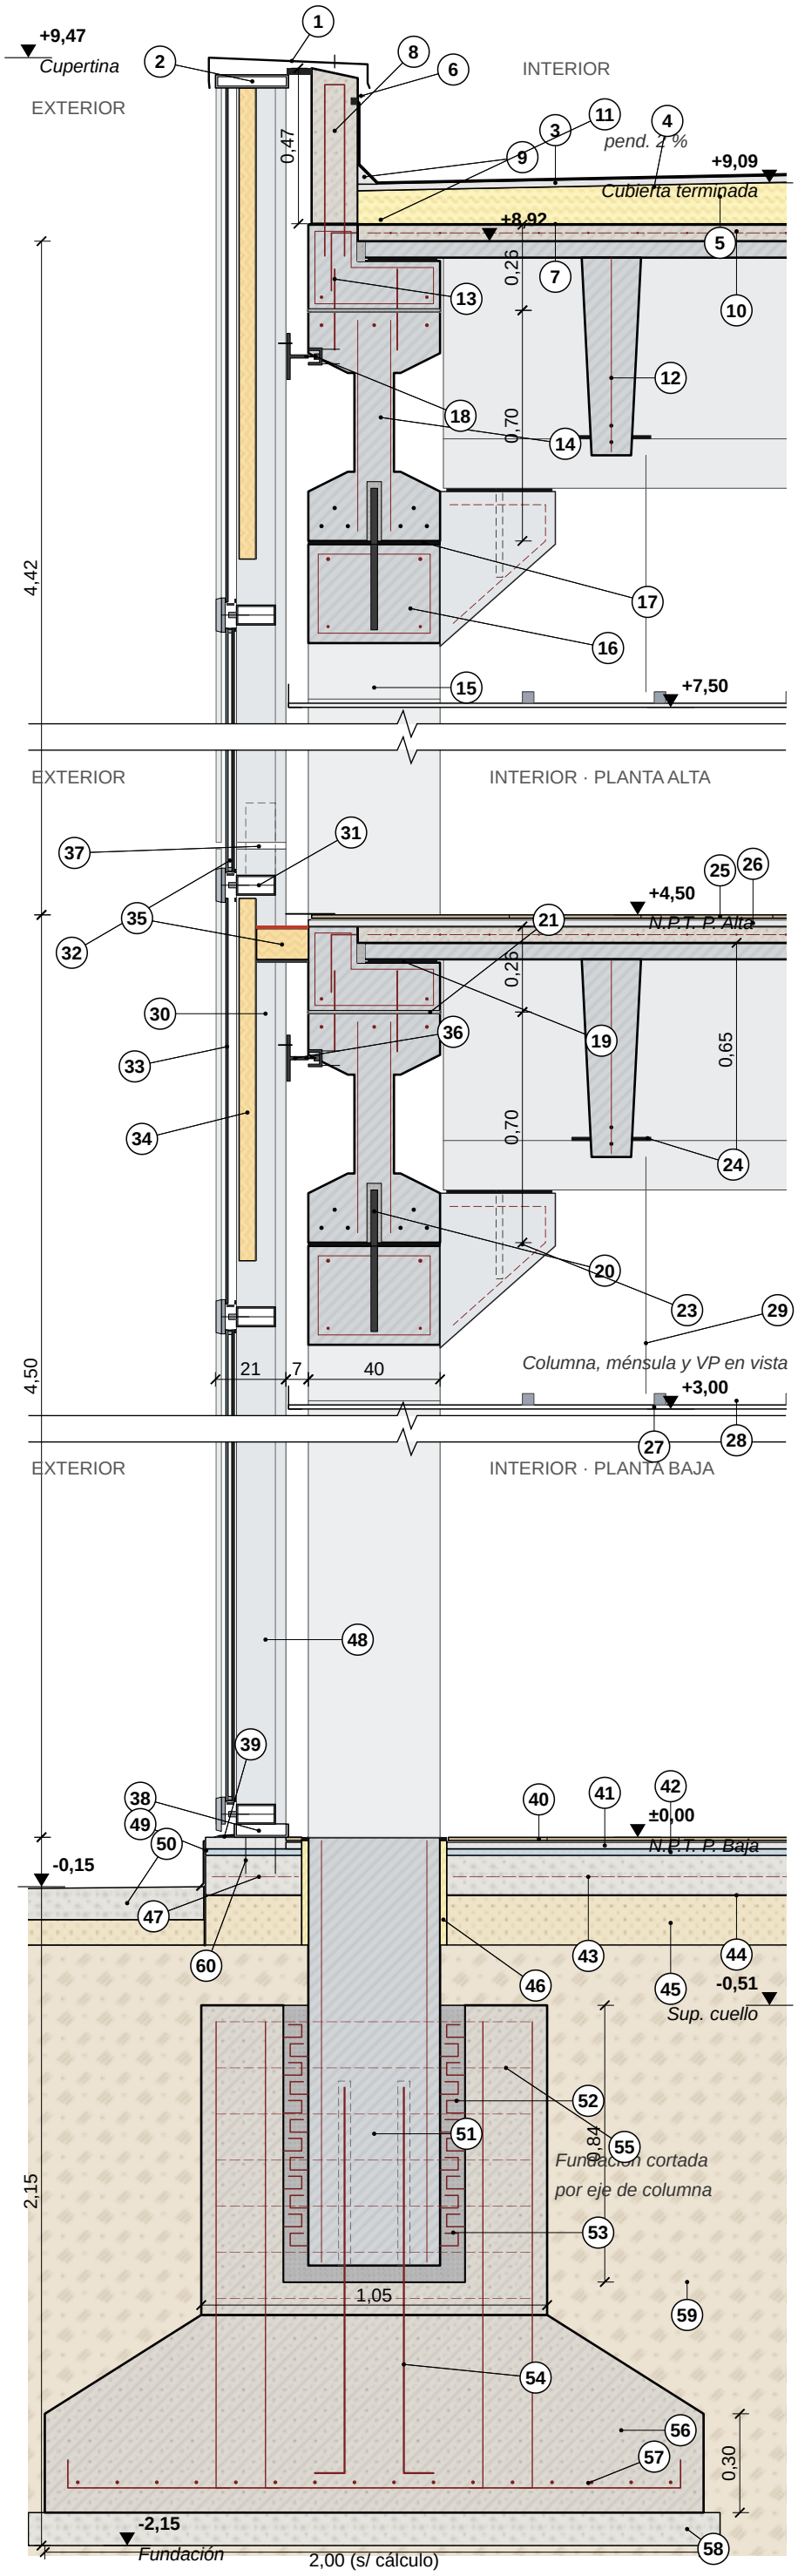


NUDO 1 · CUBIERTA
Isométrica esc. 1:17,5

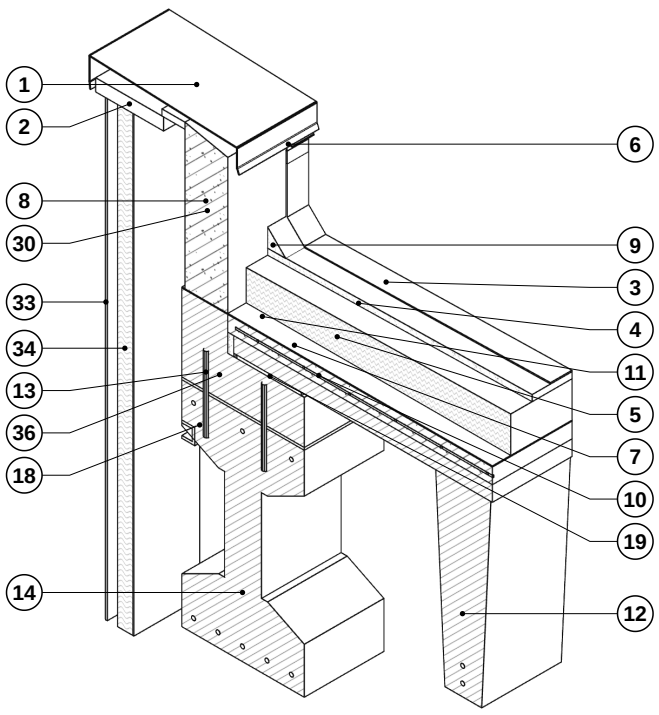

NUDO 2 · ENTREPISO
Isométrica esc. 1:20

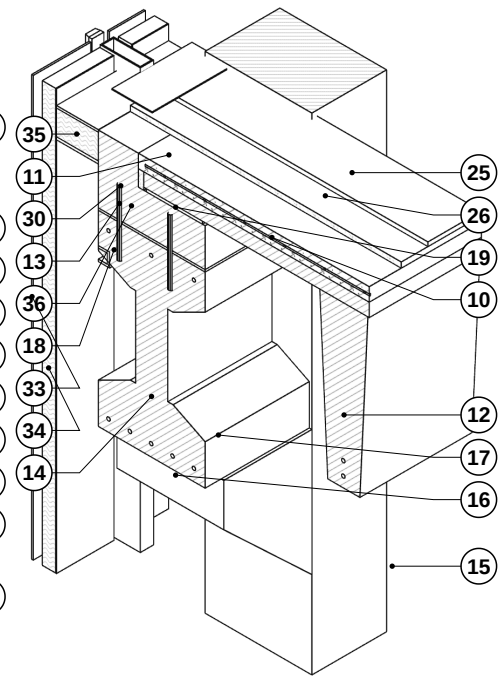

NUDO 3 · PISO
Isométrica esc. 1:15

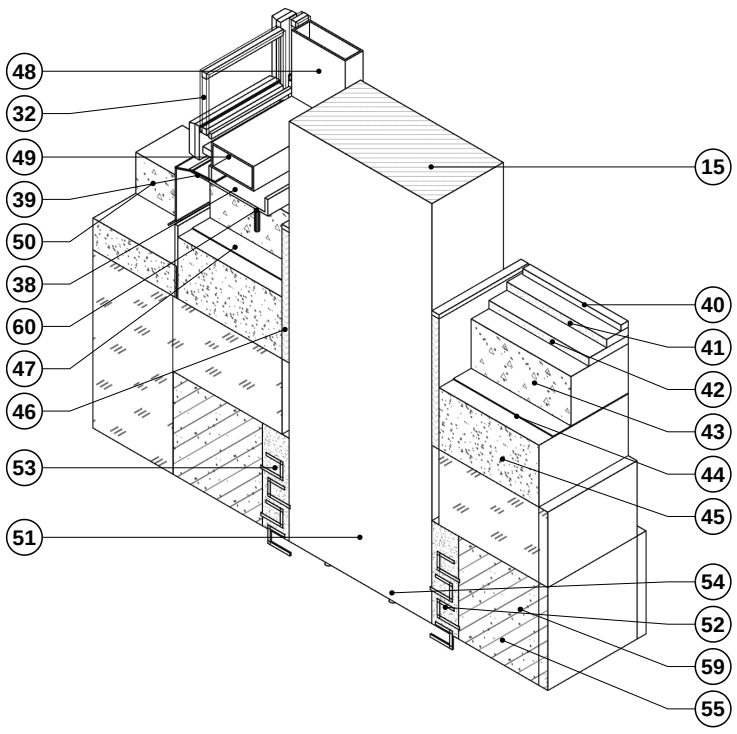

TP FINAL FECHA: 19/10/2026	DOCENTE: Arq. Tucci y Arq. Cardozo ALUMNA: Candelaria Vitale GRUPO: 13	NIVEL: OBS:	CONSTRUCCIONES II CATEDRA: ARQ. TUCCI