CORTE INTEGRAL
CERRAMIENTO VIDRIADO

ESCALA 1:20

REFERENCIAS

NUDO: FUNDACION ZAPATA AISLADA DE H°A° Y CERRAMIENTO VERTICAL OPACO


1 Suelo tosca compactada
2 As inferior de la base
3 H° de limpieza e: 0.05m
4 As de tronco de base
5 Tronco de base H°A° IN SITU
6 Armadura principal de cabezal.
7 Estribos Ø10 s/calculo
8 Perchas Ø10 s/calculo
9 Cabezal H°A° h: 0.80m
10 Mortero fluido para anclajes tipo "Grout" e: 0.03m
11 Perno roscado de anclaje
12 Placa de anclaje de base columna metalica e: 0.012m
13 Doble tuerca roscada y contra tuerca con arandela
14 Cartelas metalicas soldadas.
15 Columna metalica HEB 400 s/corte.
16 Film de polietileno 200u.
17 Contrapiso de H° pobre de cascote e: 0.08m
18 Carpeta hidrofuga MCI e: 0.02m
19 Carpeta niveladora e: 0.02m
20 Adhesivo cementicio para porcelanato e: 0.01m
21 Mortero de junta e: 0.01m
22 Solado de terminacion: porcelanato 60x60cm e: 0.01m
23 Carpeta niveladora MHR
24 Contrapiso HRP 1:1/4:3:6 e: 0.08m
25 Remate inferior de panel en fachada (Acero prelacado) e: 0.06cm

NUDO: ENTREPISO STEEL DECK Y CERRAMIENTO SISTEMA PANEL SANDWICH


26 Viga metalica HEB400 (40X30cm) Luz: 6.00mts
27 Cartela angular vinculacion viga–columna
28 Perno conector de corte Steel Deck (placa colaborante) h: 0.13mts
29 Tuerca abulonada para vinculacion viga–columna
30 Moldura frontera ALCOR de borde "L" galvanizada + sujetador de borde
31 Solado de terminacion: porcelanato 60x60cm e: 0.01m
32 Carpeta MHR 1:1/4:3 e: 0.02m
33 Contrapiso liviano EPS e: 0.04m
34 Malla electrosoldada c/0.15m s/calculo
35 Capa de compresion H°A° e: 0.03m
36 Placa colaborante Steel Deck ALCOR h: 0.11m
37 Viga entrepiso secundaria HEB300 (30x30cm) Luz: 6.00m
38 Angulo "L" perimetral para cierre de cielorraso tecnico
39 Placa roca yeso para cielorraso tecnico e: 0.02m
40 Perfil larguero
41 Perfil travesaño
42 Placa soldada a viga para fijacion de cielorraso tecnico
43 Cuelgue de esctructura de cielorraso tecnico
44 Perfil PGU 100
45 Tornillo de union perfil PGU–Columna metalica
46 Lamina interior de acero galvanizado
47 Aislacion termica: panel poliuretano (PUR) e: 80mm
48 Lamina exterior de acero galvanizado
49 Tornillo autoperforante de union oculta entre Paneles y PGU
50 Encuentro entre paneles con fijacion oculta y encastre
51 Cerramiento integral en muro panel sandwich

NUDO: CUBIERTA PLANA Y CERRAMIENTO PANEL SANDWICH


52 Barrera de vapor: pintura asfaltica
53 Contrapiso liviano EPS con pendiente e: 0.04mts
54 Mortero impermeable MCI e: 0.05mts
55 Carpeta niveladora
56 Membrana asfaltica de aluminio
57 Losa de H°A° sobre encofrado perdido h: 0.11mts
58 Malla de reparticion
59 Tornillo autoperforante para fijaciones cupertina
60 Aislacion termica EPS para cierre superior
61 Cupertina de chapa galvanizada
62 Moldura tapa ALCOR
63 Soporte de Malla

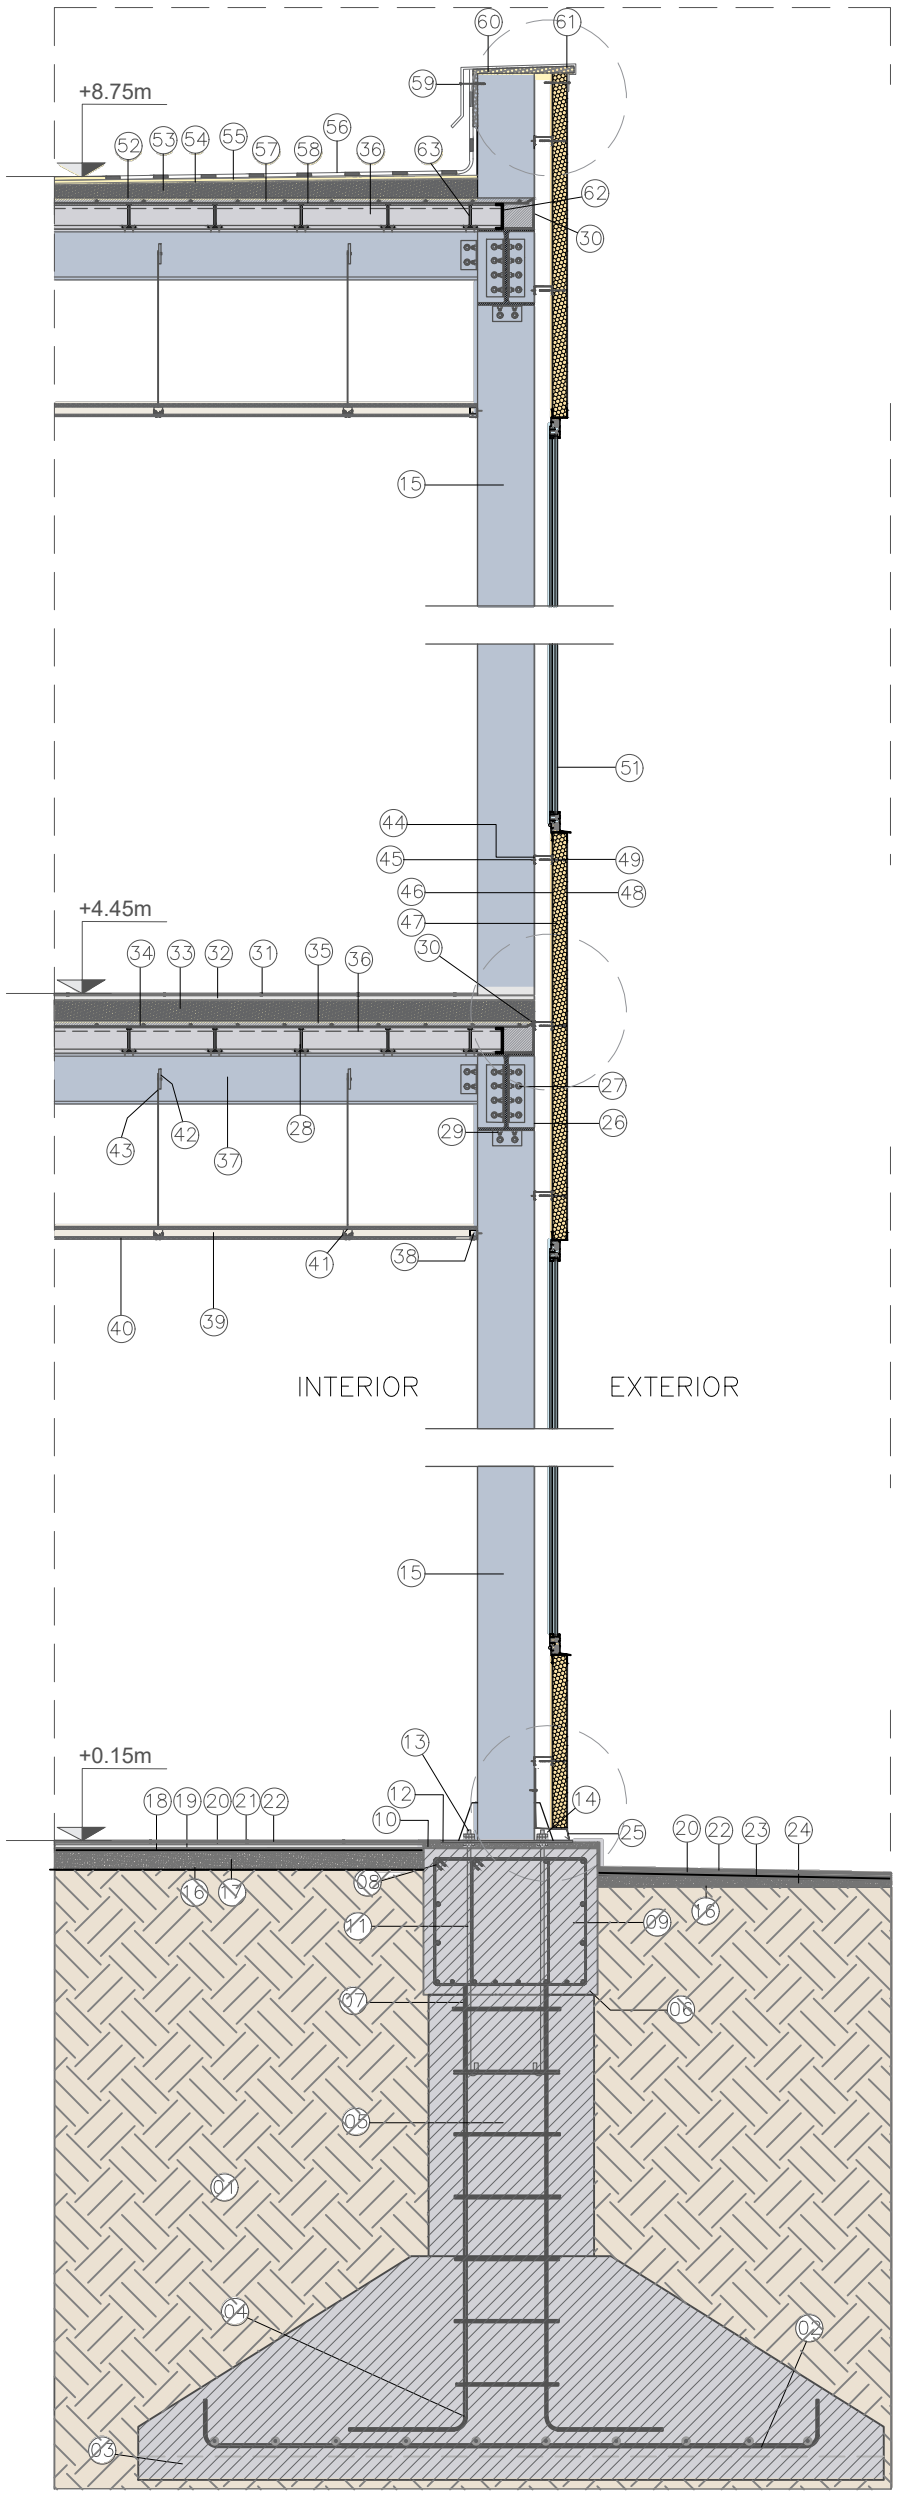


DETALLE 1 · CUBIERTA Y PANEL SANDWICH

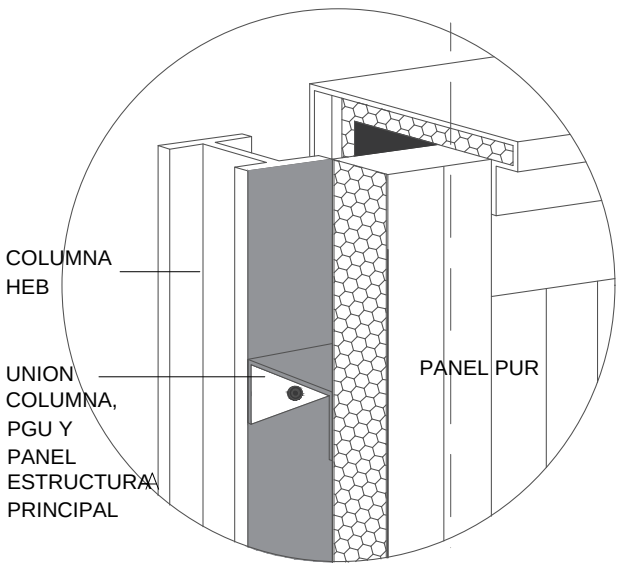

DETALLE 2 · ENTREPISO Y PANEL SANDWICH

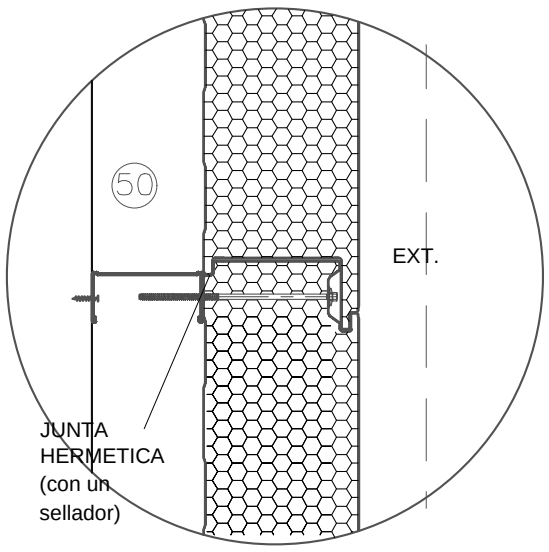

DETALLE 3 · FUNDACIÓN Y REMATE DE FACHADA

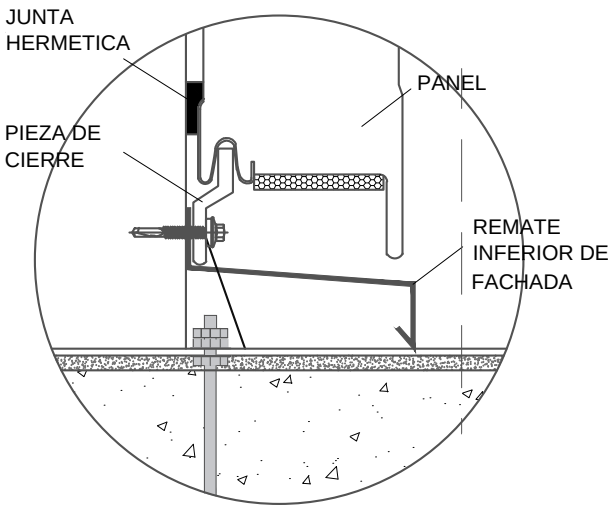

TP N°6 FECHA:19/10/26	DOCENTE: Arq. Tucci y Arq. Cardozo ALUMNOS: Gómez Karen GRUPO: 13	NIVEL: OBS:	CONSTRUCCIONES II CATEDRA: ARQ. TUCCI