CORTE INTEGRAL
ACERO (OPACO)

REFERENCIAS

1- ZINGUERIA CUPERTINA

2- AILACION HIDROFUGA MEMBRANA CON ALUMINIO

3- CARPETA HIDROFUGA MCI 1:3: + 10% ADITIVO HIDROFUGO

4- CONTRAPISO LIVIANO H° EPS 1:6 CON PENDIENTE 2%

5- MALLA ELECTROSOLDADA

6- CAPA DE COMPRESION

7- CHAPA COLABORANTE

8- FIJACION CON TORNILLO

9- VIGA PERFIL IPN 200

10- COLUMNA IPN 300

11- PLANCHUELA "L"

12- SOLADO + ZOCALO CERAMICO CON ADHESIVO CEMENTICIO

13- CARPETA DE NIVELACION MHR 1/ 14:3

14- CONTRAPISO LIVIANO SOBRE LOSA H° EPS 1:6

15- CARPETA A LA CAL MHR 1:1/ 4:3

16- AISLACION HIDROFUGA MCI 1:3 + 10% ADHTIVO HIDROFUGO

17- CONTRAPISO S/ TERRENO NATURAL H° EPS 1:6

18- SEPARADOR DE SUELO FILM DE POLIETILENO 200 M

19- CONTRAPISO HHRP 1:1/ 4:4:8 CON PENDIENTE

20- ANCLJE / BULONES, TUERCA + CONTRA TUERCA

21- FUNDACION BASE H° A°

22- HORMIGON POBRE DE LIMPIEZA 5CM

23- TOSCA COMPACTAD

24- PANEL OPACO

25- JUNTA DE DILATACION

26- PLACA DE BORDE, MOLDURA

27- MENSULA


28- VIGA PORTAPANEL

29- TENSOR CON TORNILLO

30- VIGA ESTRUCTURAL 30CM X 30CM
SOLADO A COLUMNA, CON SELLADO DE SILICONA + TORNILLO AUTOPERFORANTE


31- PLATABANDA

32- ALA IPN 300 CON SOLDURA A COLUMNA

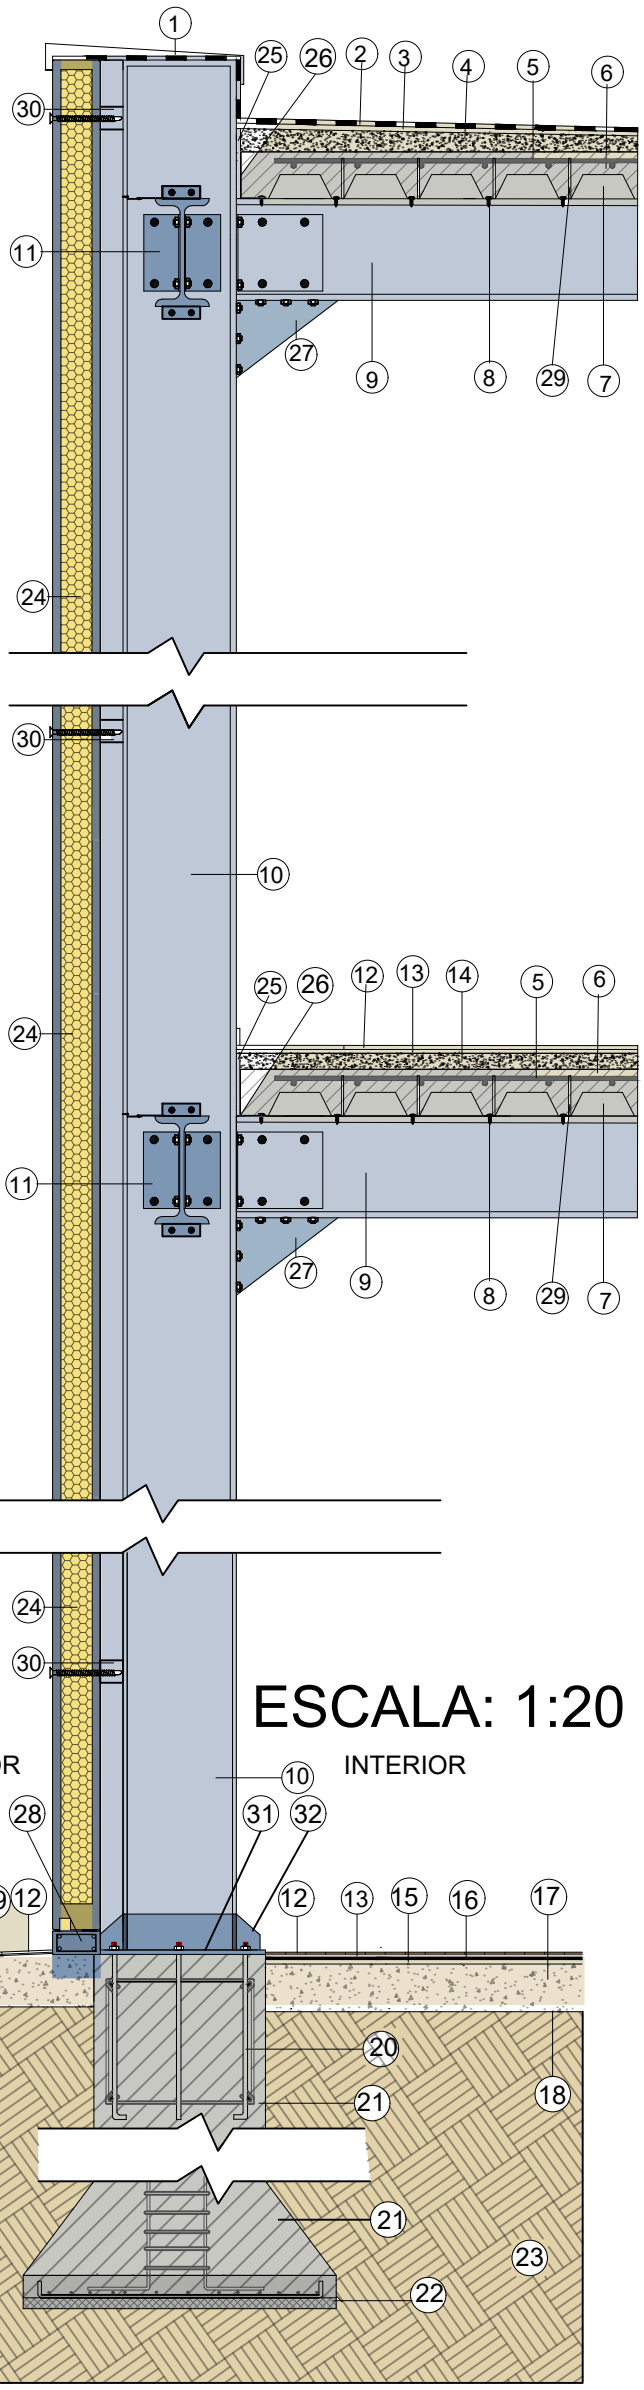


ESCALA: 1:10 DETALLES


DETALLE 1:
DE JUNTAS

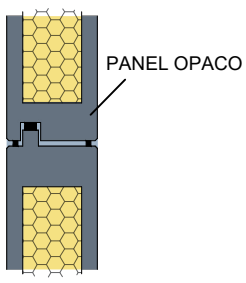

DETALLE 2:
COLUMNA Y FUNDACION

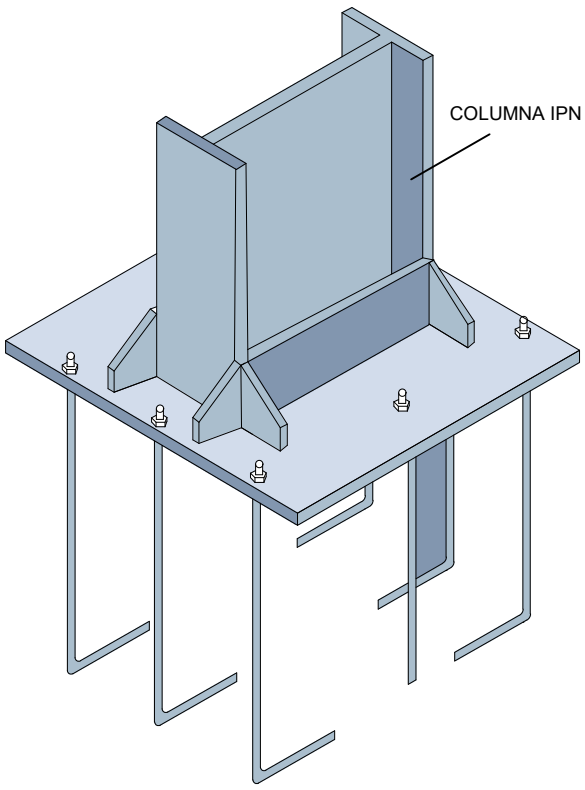

DETALLE 3:
COLUMNA Y VIGA

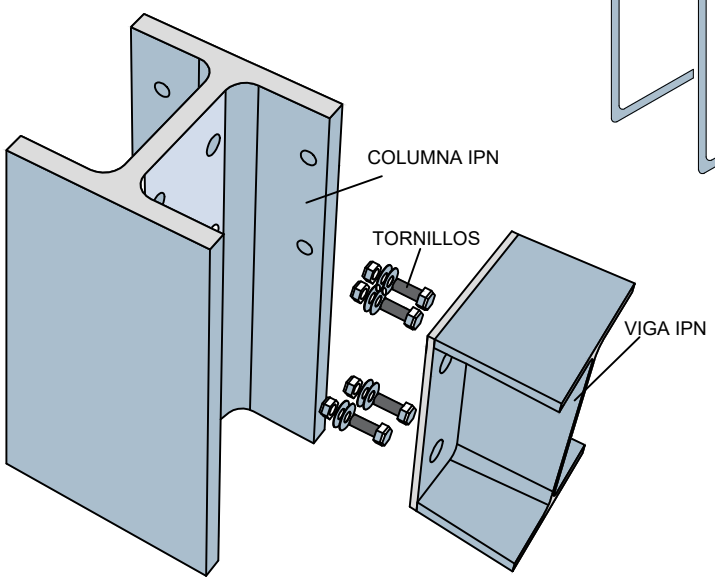

ESCALA: 1:20

TP FINAL FECHA:05/11/26	DOCENTE: Arq. Tucci y Arq. Cardozo ALUMNA: Azcona Karina GRUPO: 13	NIVEL: OBS:	CONSTRUCCIONES II CATEDRA: ARQ. TUCCI